| 会签栏 | | | | | | | | |
|---|---|---|---|---|---|---|---|---|
| | 建　筑 | 宋延勇 | | | 暖　通 | 陈少玲 | | |
| | 结　构 | 邓艳青 | | | | | | |
| | 给排水 | 甘兆麟 | | | | | | |
| | 电　气 | 蔡泽炯 | | | | | | |

注：1.厅门、对重、梯井、轿厢、电梯机房的预埋件及预留孔尺寸、层显及按钮预留孔以电梯厂商提供为准。
2.设置电梯井道中的圈梁时如与结构梁有冲突，需保证圈梁的间距，可与结构梁结合设置。
3.如圈梁如与召唤箱留孔有冲突，圈梁可向上移至梁底平留孔顶。
4、电梯层门的耐火极限不应低于1.00h。

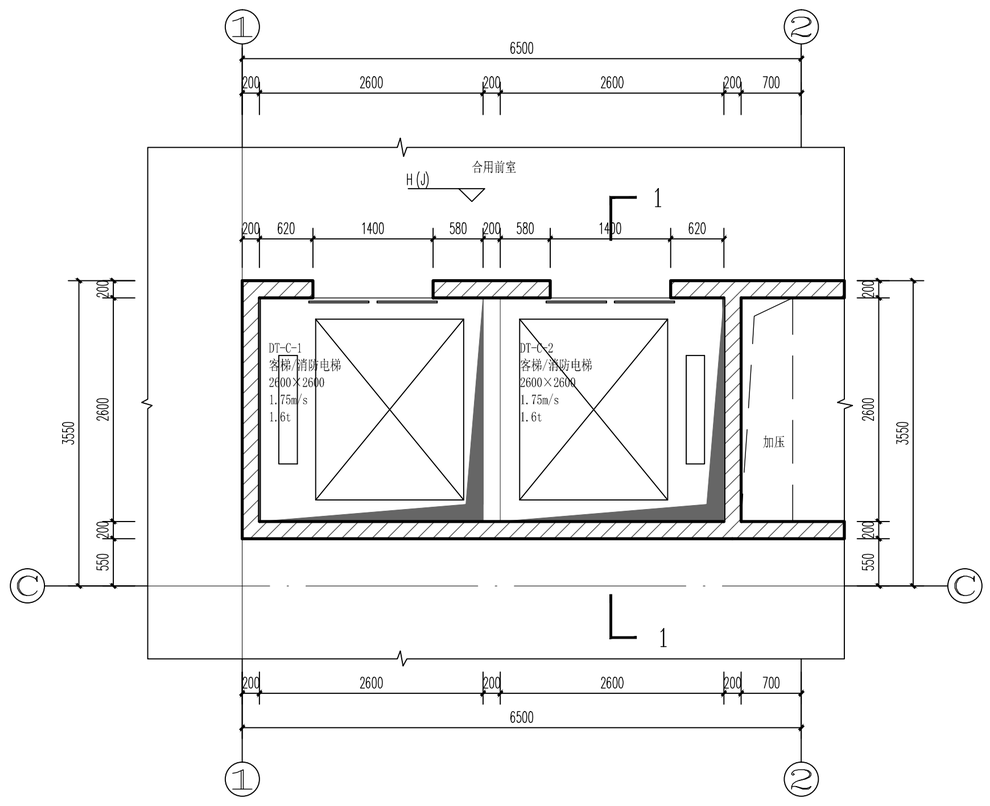


| 楼层 | 层高 | 建筑标高（J）H | 结构标高(G) |
|---|---|---|---|
| 3F | 5500 | 13.500 | 13.450 |
| 2F | 5500 | 8.000 | 7.920 |
| 1F | 8000 | 0.000 | -0.080 |
| -1F | 6050 | -6.650 | -6.750 |
| -2F | 4100 | -10.150 | -10.250 |
| -3F | 3600 | -13.850 | -14.000 |

| 比例 | DC-C-1~2　地下二层~二层平面 |
|---|---|
| 1:50 | |

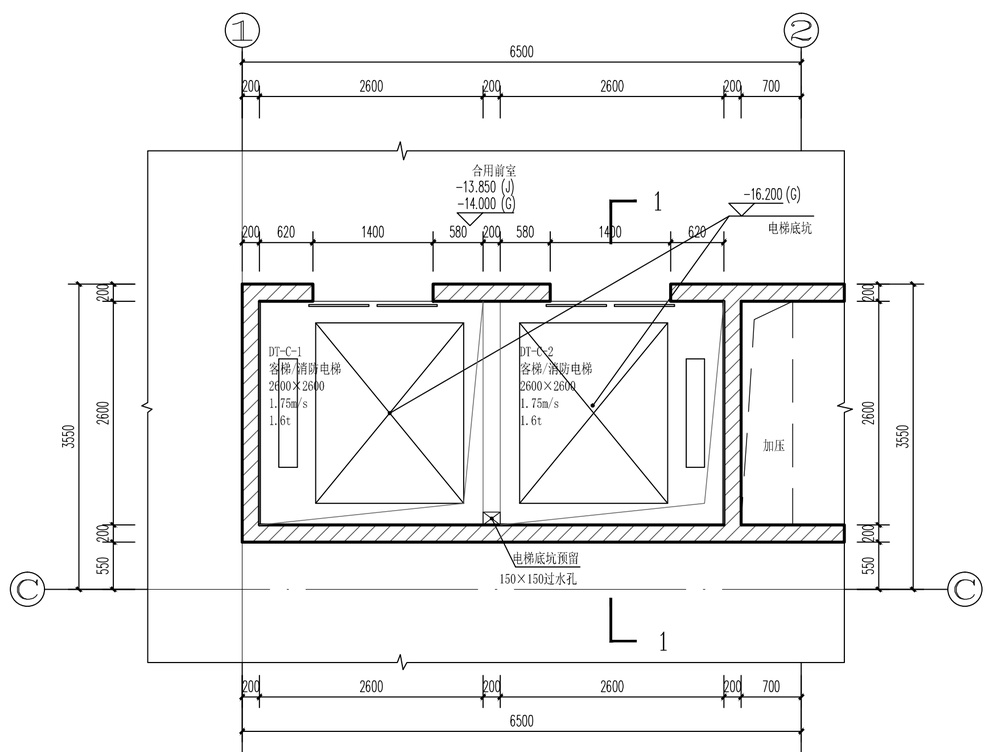


| 比例 | DC-C-1~2　地下三层平面 |
|---|---|
| 1:50 | |

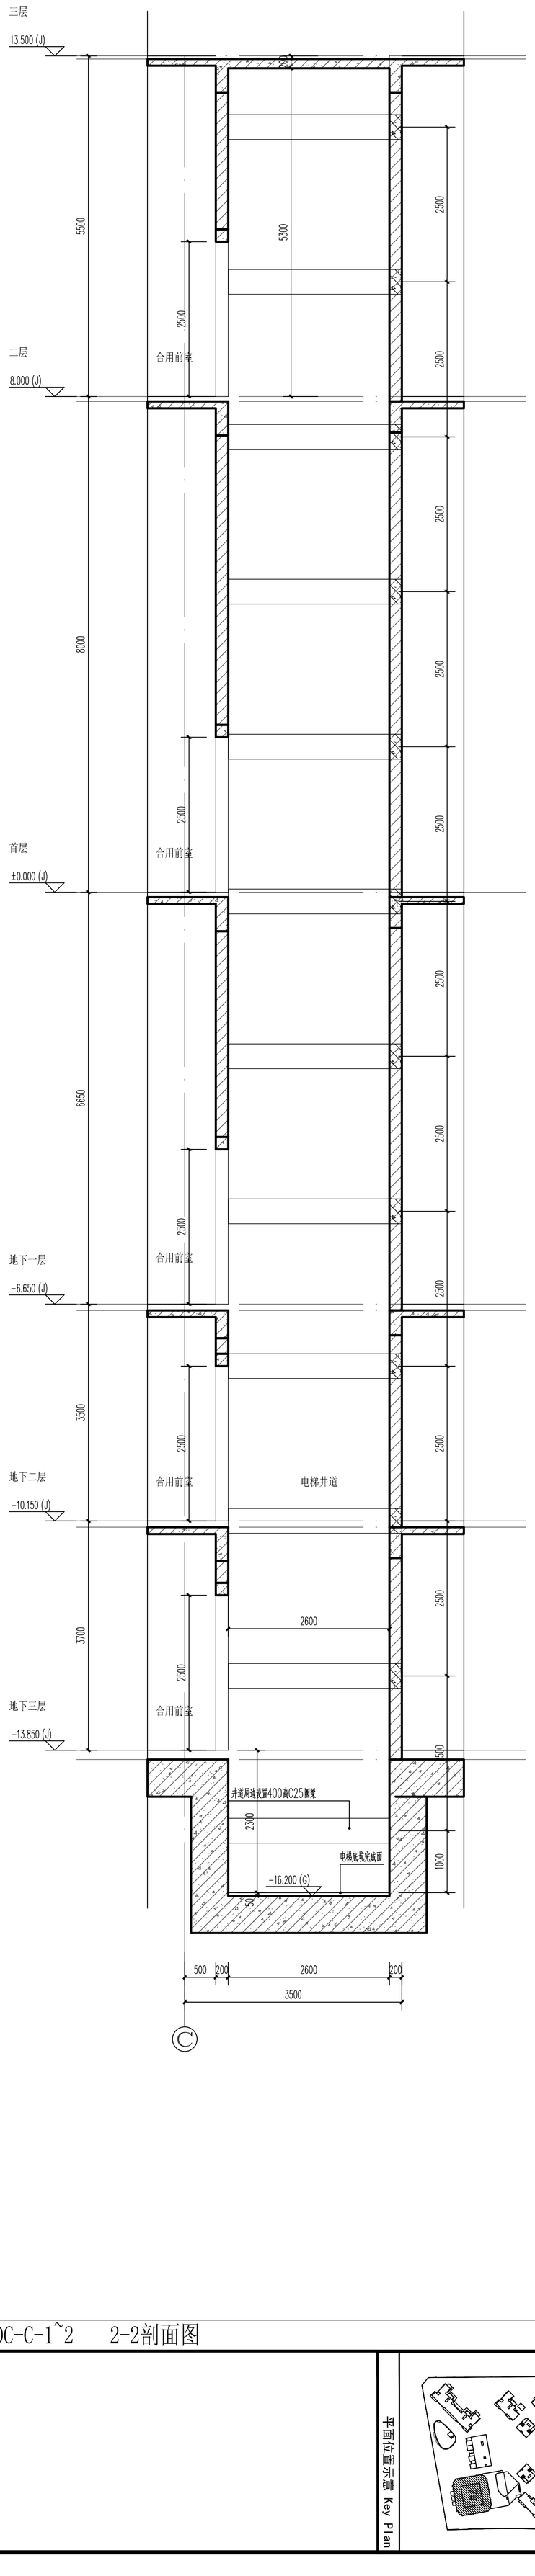


| 比例 | DC-C-1~2　2-2剖面图 |
|---|---|
| 1:50 | |

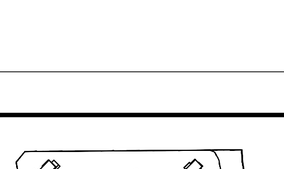

平面位置示意 Key Plan

| 版本号 | 日期 | 修改内容 | 修订者 |
|---|---|---|---|
| | | | |

图纸条码

| 院总工程师 | 赵松林 | |
|---|---|---|
| 审定 | 黄孝颖 | |
| 审核 | 张林汉 | |
| 设总负责人 | 黄孝颖 | |
| 专业负责人 | 张林汉 | |
| | 宋延勇 | |
| 校核 | 石昊洋 | |
| 设计 | 胡伟航 | |

| 建设单位 | 佛山市禅城区保宸置业有限公司 | | |
|---|---|---|---|
| 工程名称 | 保利天珺秀台7# | | |
| 业务号 | 21-347 | 专业 | 建筑 |
| 设计阶段 | 施工图 | | |
| 图纸名称 | DC-C-1~2 电梯大样图 | | |
| 图号 | J-1-DT07 | 版本号 | |
| 出图日期 | 2023.08.02 | 序号 | |

版权所有，不得复制、套用或公开。
ALL RIGHTS RESERVED.

广州市设计院集团有限公司
GUANGZHOU DESIGN INSTITUTE GROUP CO.,LTD.
工程设计甲级资质证书编号：A244007378
工程勘察甲级资质证书编号：B244007378