会签栏								
	建　筑	宋延勇			暖　通	陈少玲		
	结　构	邓艳青						
	给排水	甘兆麟						
	电　气	蔡泽炯						

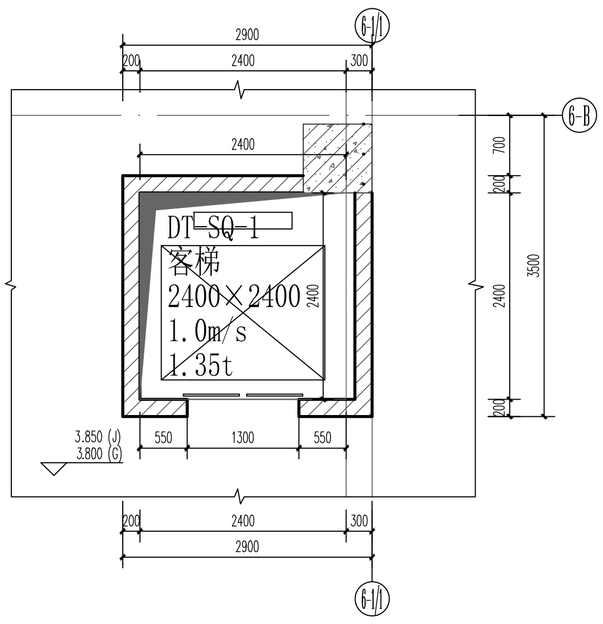

比例 1:50　DT-SQ-1　首层夹层平面

1

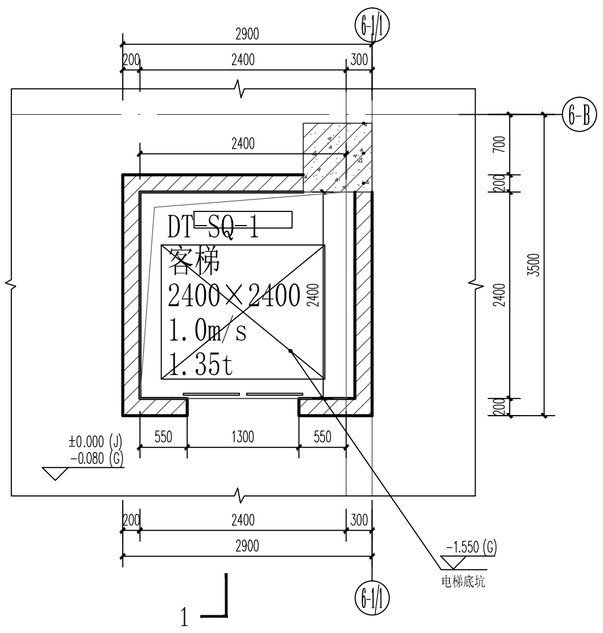

1

比例 1:50　DT-SQ-1　首层平面

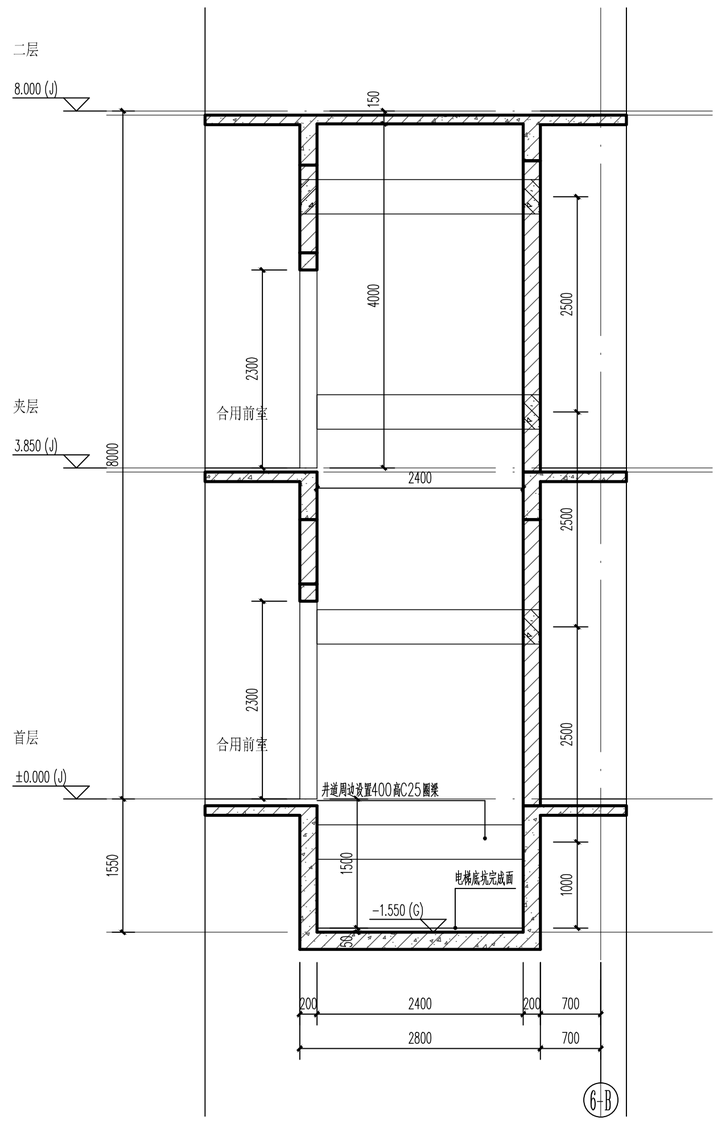

比例 1:50　DT-SQ-1　1-1剖面

广州市设计院集团有限公司
GUANGZHOU DESIGN INSTITUTE GROUP CO.,LTD.
工程设计甲级资质证书编号：A244007278
工程勘察甲级资质证书编号：B244007378

平面位置示意 Key Plan

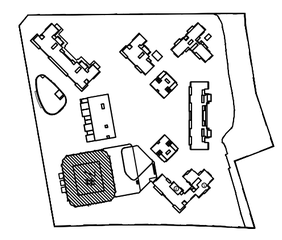

版本号	日期	修改内容	修订者

图纸条码

院总工程师	赵松林	赵松林
审定	黄孝颖	黄孝颖
审核	张林汉	张林汉
设计总负责人	黄孝颖	黄孝颖
专业负责人	宋延勇	宋延勇
校核	石昊洋	石昊洋
设计	胡伟航	胡伟航

建设单位	佛山市禅城区保宸置业有限公司
工程名称	保利天珺秀台7#
业务号	21-347
专业	建筑
设计阶段	施工图
图纸名称	DT-SQ-1 电梯大样图
图号	J-1-DT08
版本号	
出图日期	2023.08.02
序号	

版权所有，不得复制、套用或公开。
ALL RIGHTS RESERVED.