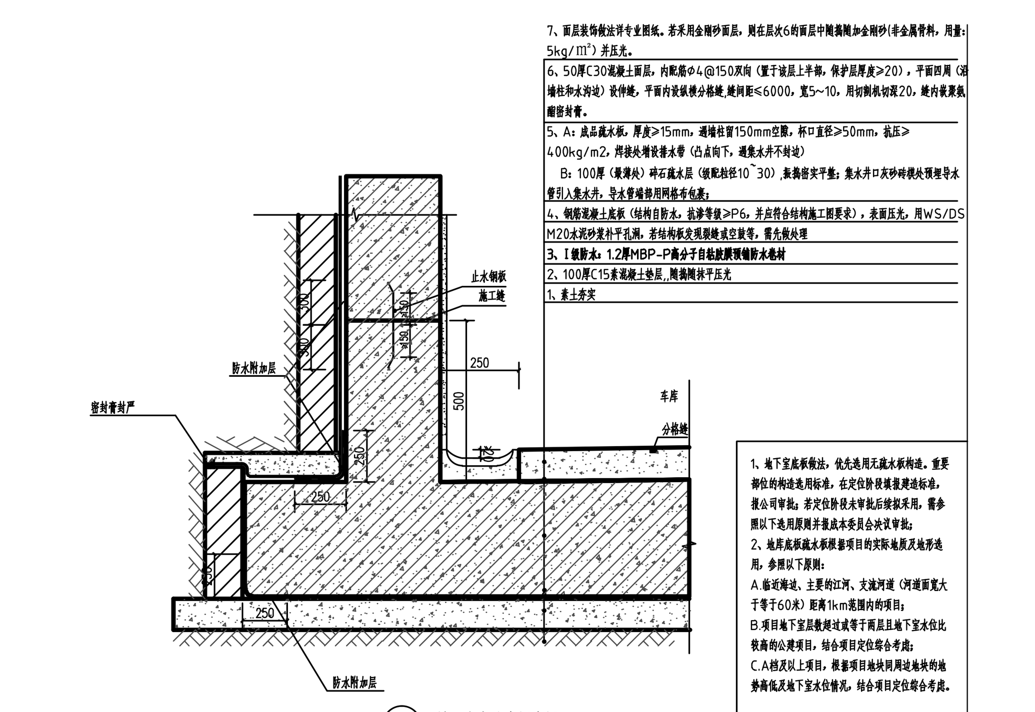

① 地下室有疏水板底板

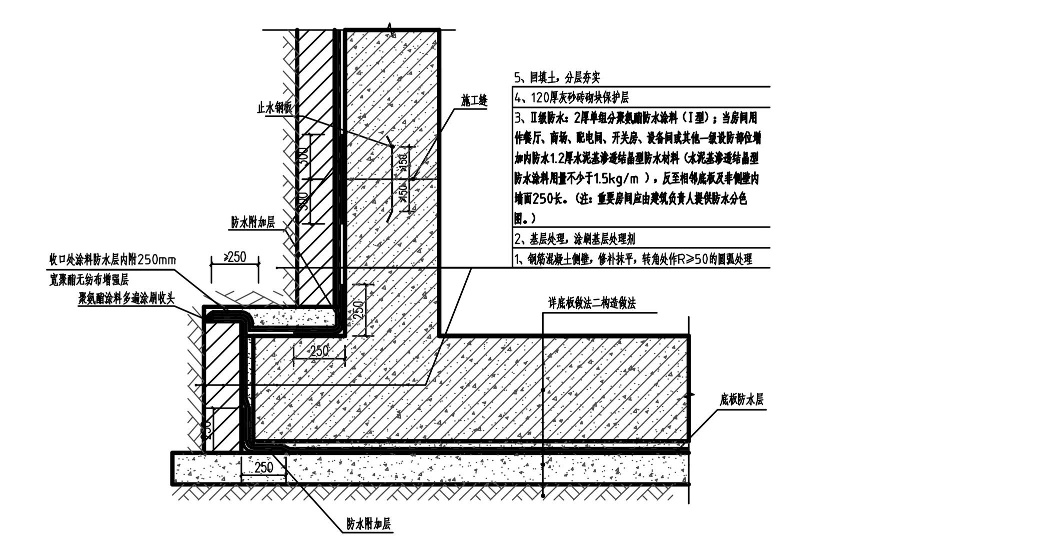

② 地下室侧壁

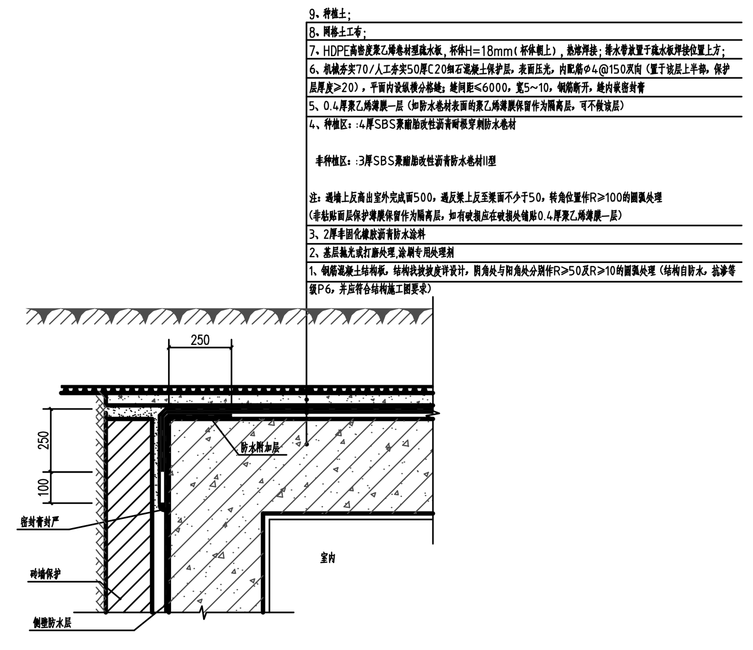

③ 地下室底板

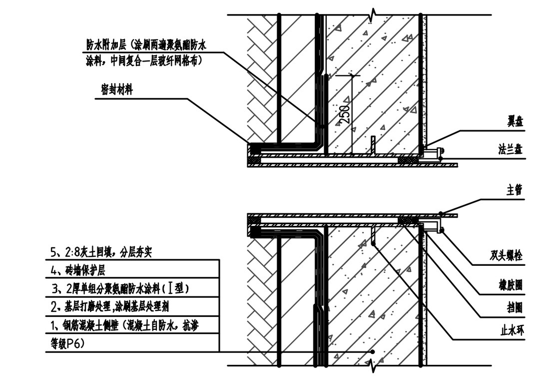

④ 侧墙穿出管

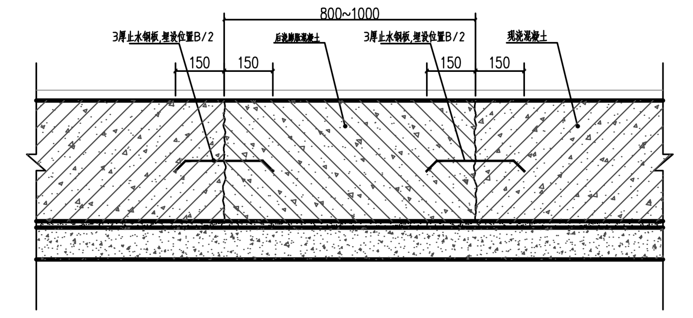

⑤ 地下室底板后浇带

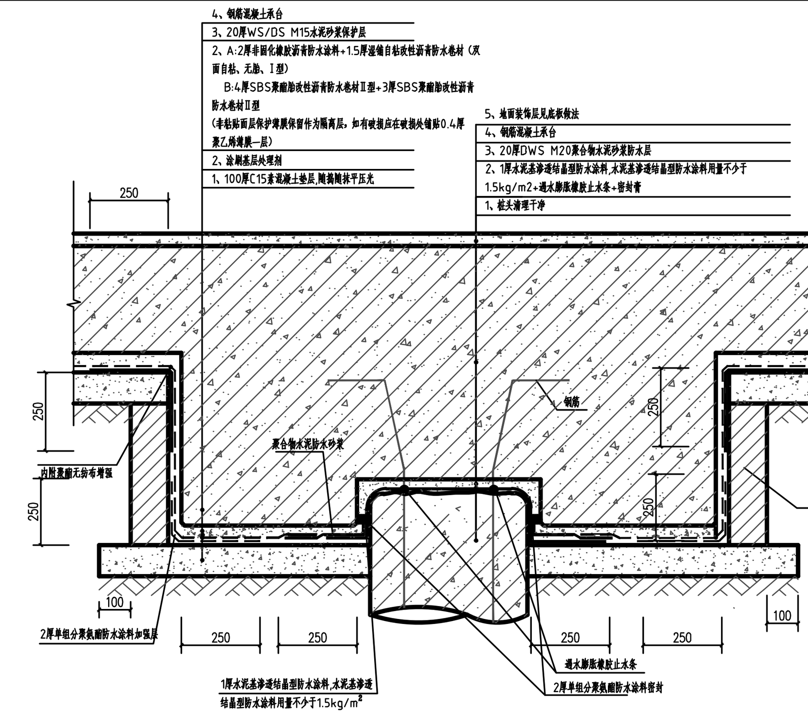

⑥ 桩头、承台

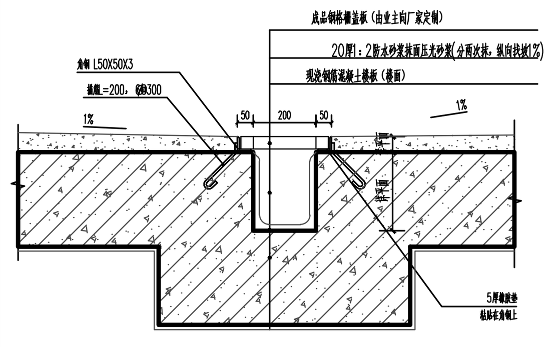

⑦ 卸货区截水沟大样 1:15

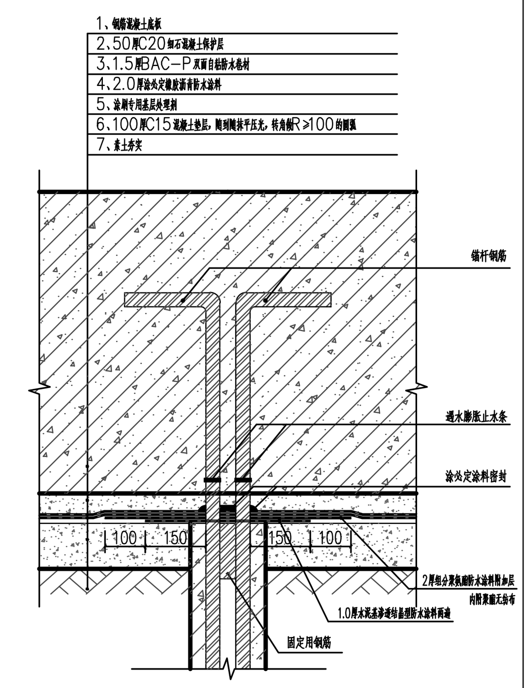

⑫ 抗拔锚杆 1:15

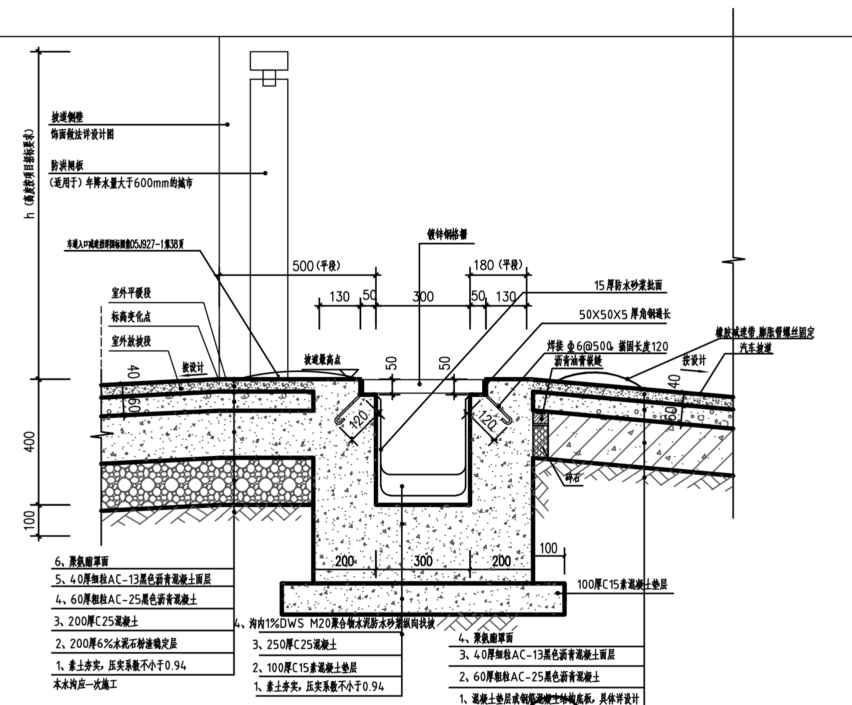

⑧ 汽车库出入口水沟 节点大样图 1:15

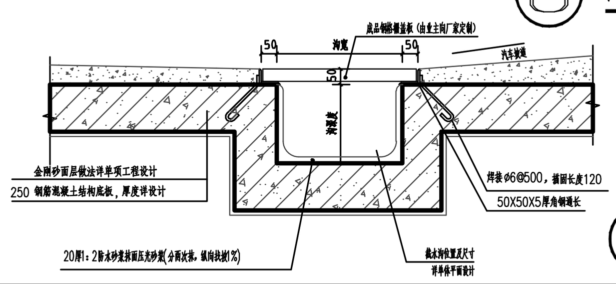

⑨ 坡道通用截水沟大样 1:15

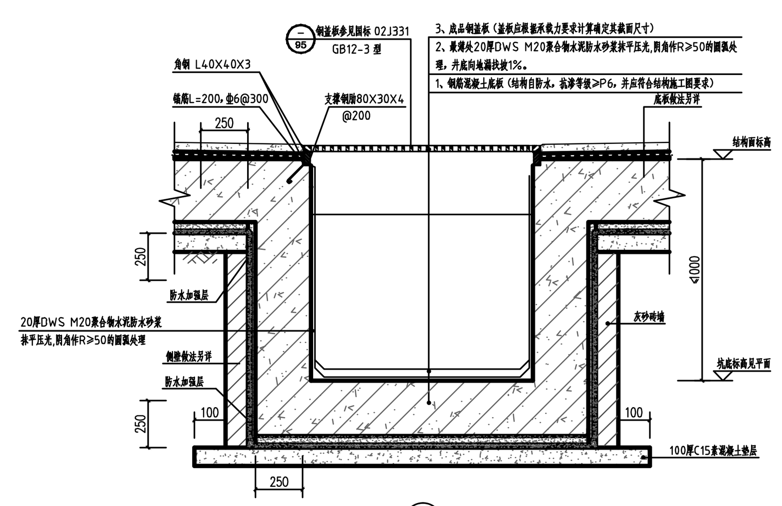

⑩ 集水井3(有疏水板)

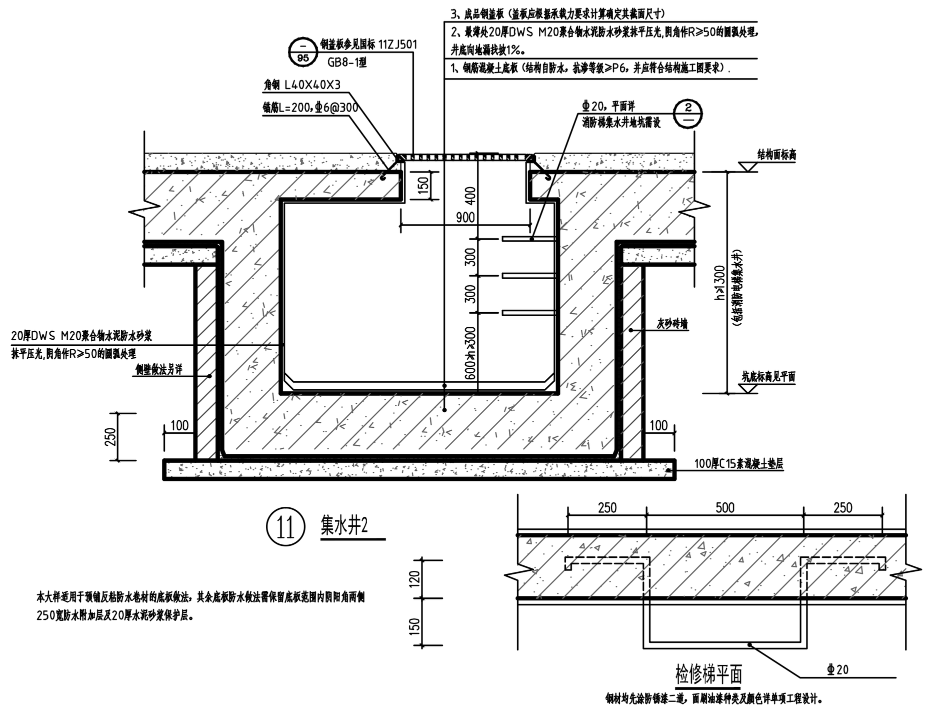

⑪ 集水井2

检修梯平面

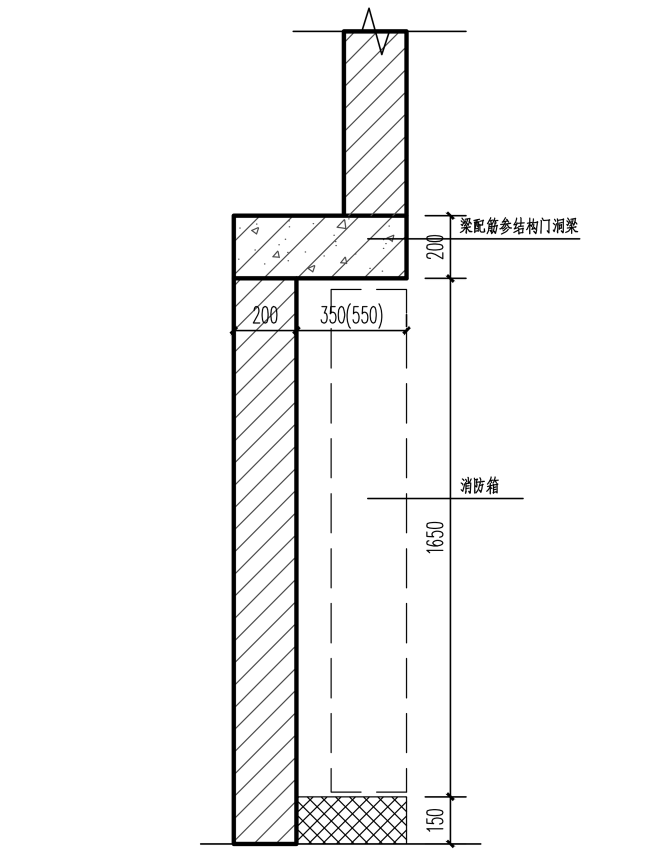

a-a剖面图

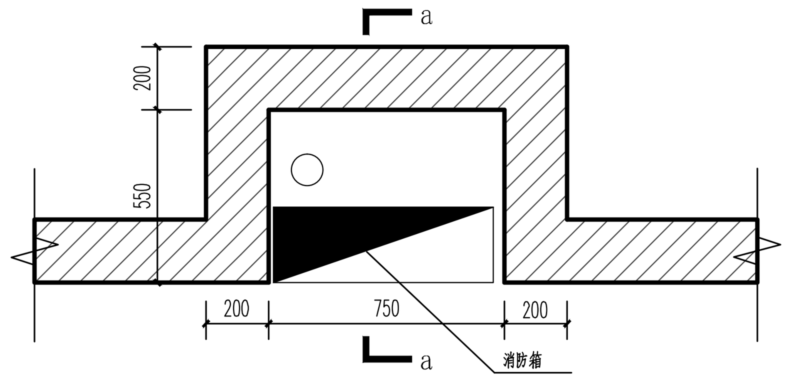

消防栓背部封堵详图
（背面进水）

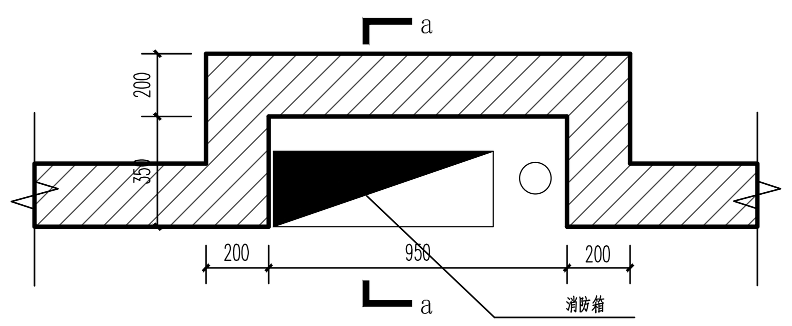

消防栓背部封堵详图
（侧面进水）

广州市设计院集团有限公司
GUANGZHOU DESIGN INSTITUTE GROUP CO., LTD.

工程设计甲级资质证书编号：A244007378
工程勘察甲级资质证书编号：B244007378

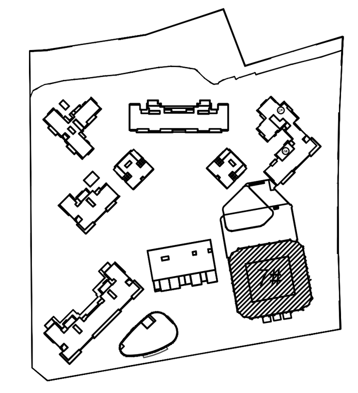

平面位置示意 Key Plan

版本号	日期	修改内容	修订者
		修订栏	

图纸条码

院总工程师	赵松林	
审定	黄孝颖	
审核	张林汉	
设计总负责人	黄孝颖	
	张林汉	
专业负责人	宋延勇	
校核	石昊洋	
设计	胡伟航	

建设单位	佛山市禅城区保宸置业有限公司
工程名称	保利天珺秀台7#
业务号	21-347 专业 建筑
设计阶段	施工图
图纸名称	构造详图
图号	J-1-GZ01
出图日期	2023.08.02

版权所有，不得复制、套用或公开。
ALL RIGHTS RESERVED.