


会签栏								
	建　筑	宋延勇			暖　通	陈少玲		
	结　构	邓艳青						
	给排水	甘兆麟						
	电　气	蔡泽洞						

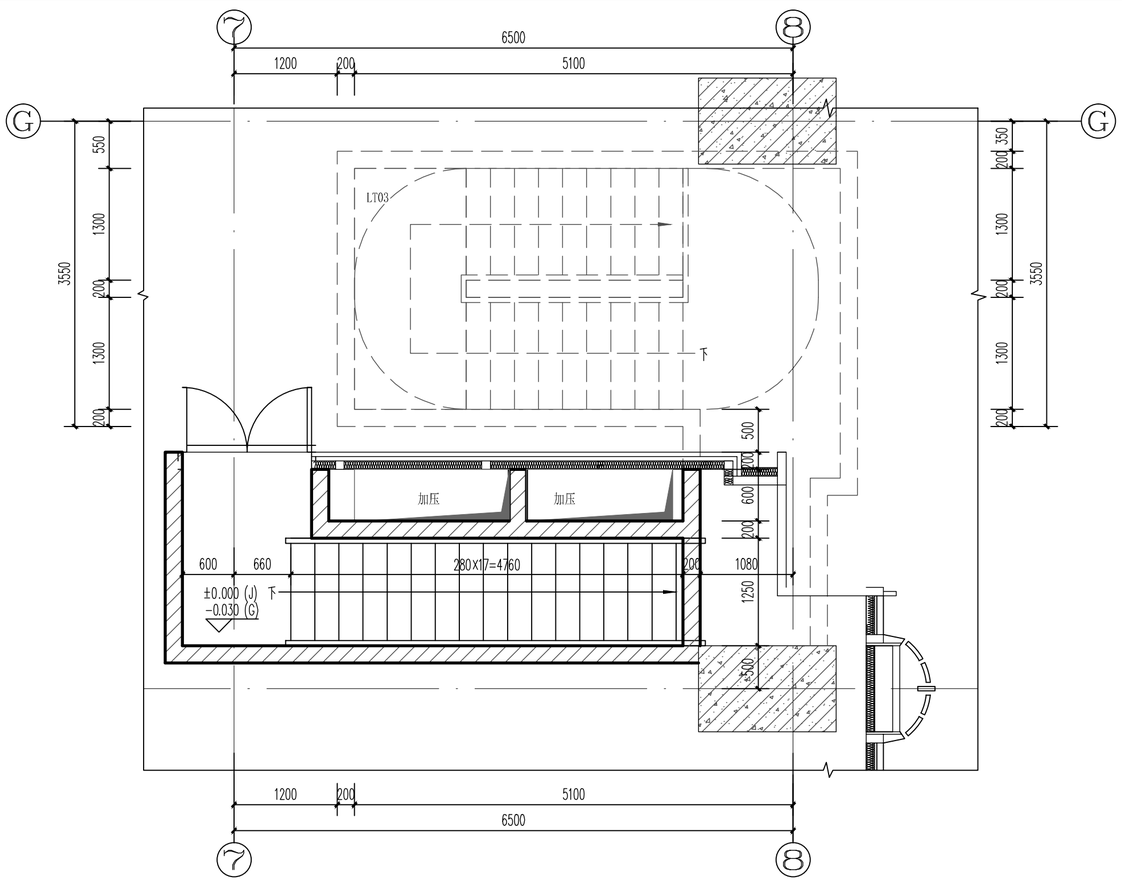


比例 1:50　LT03　首层平面

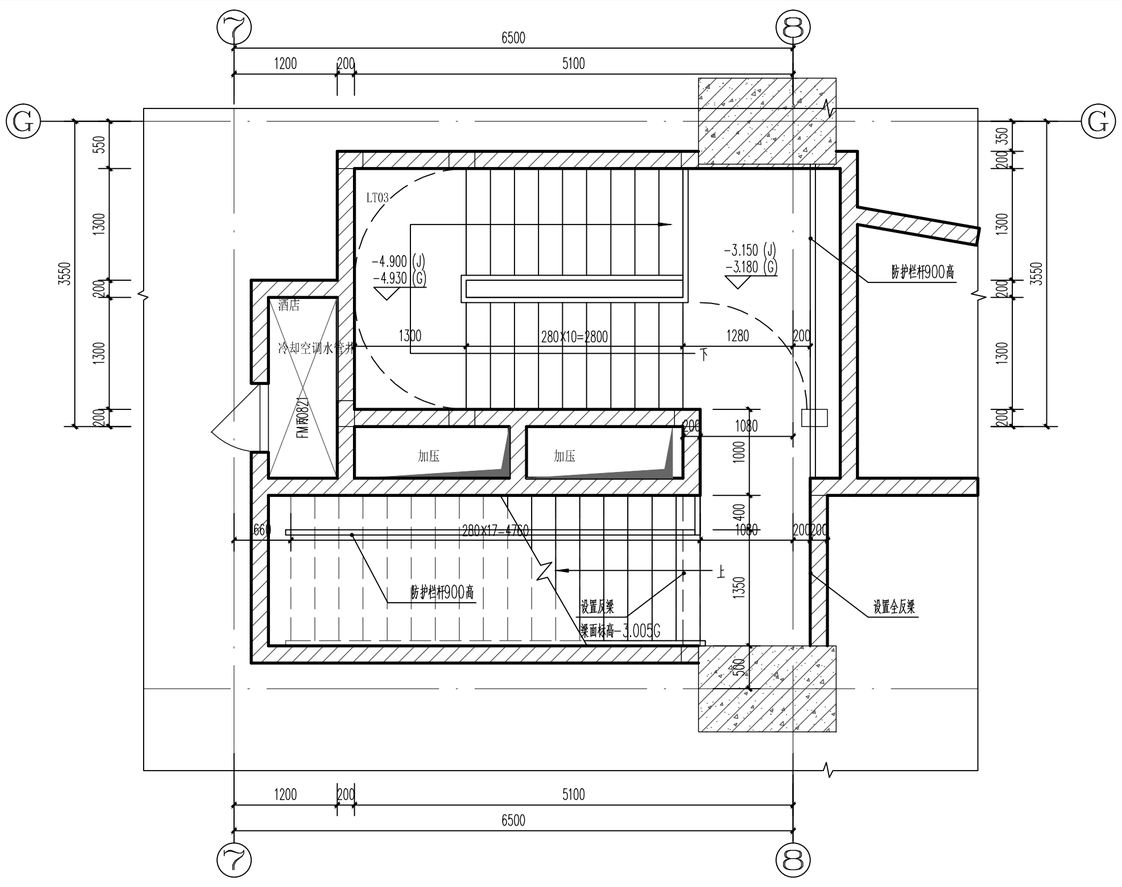


比例 1:50　LT03　-3.150标高平面

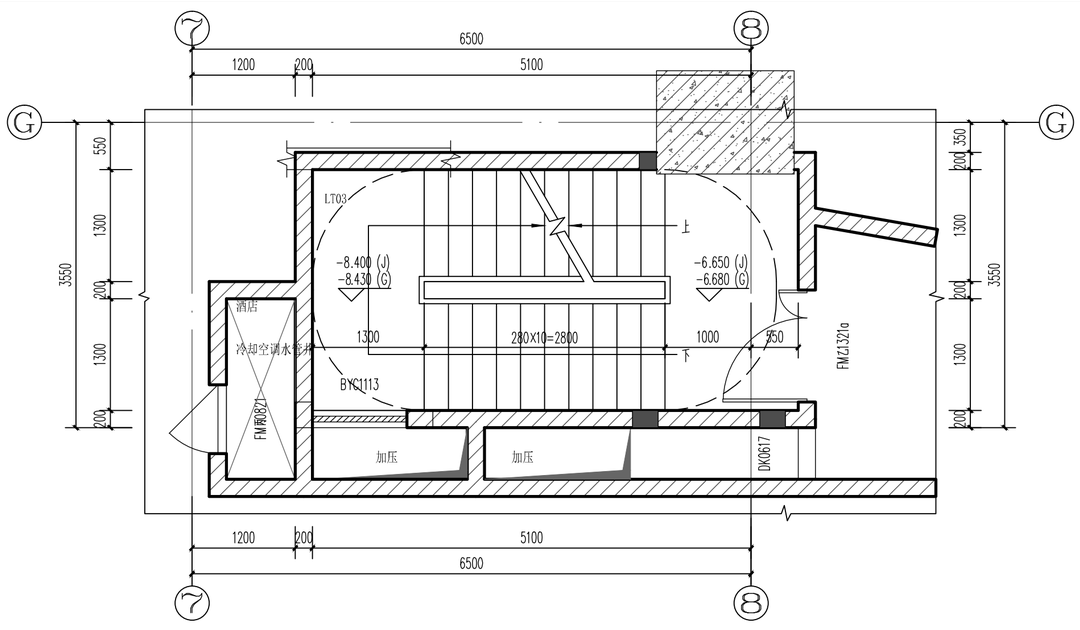


比例 1:50　LT03　地下一层平面

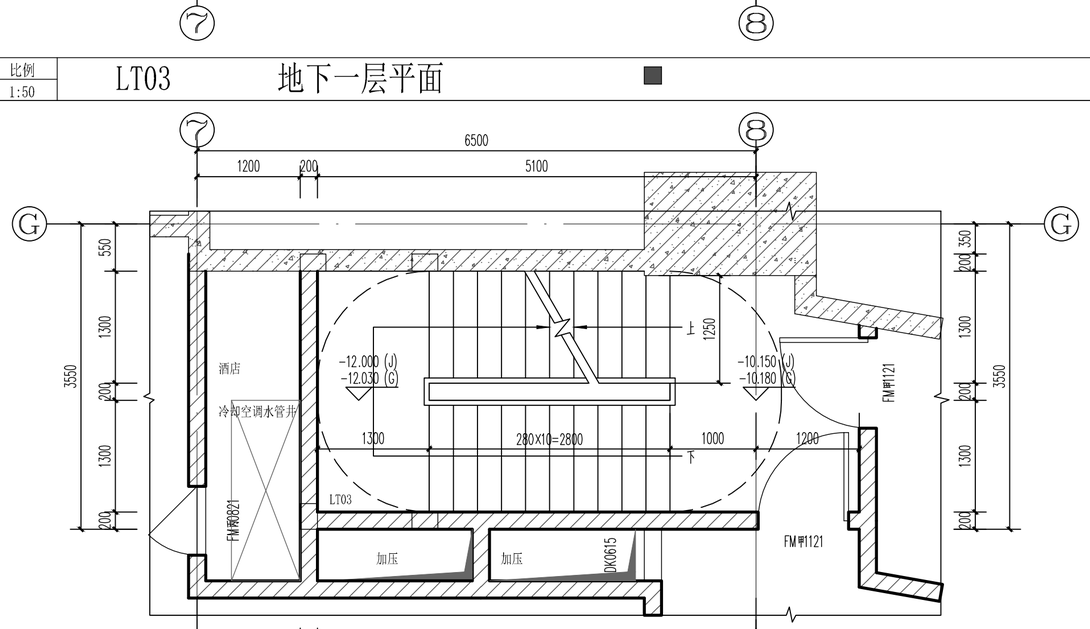

比例 1:50　LT03　地下二层平面

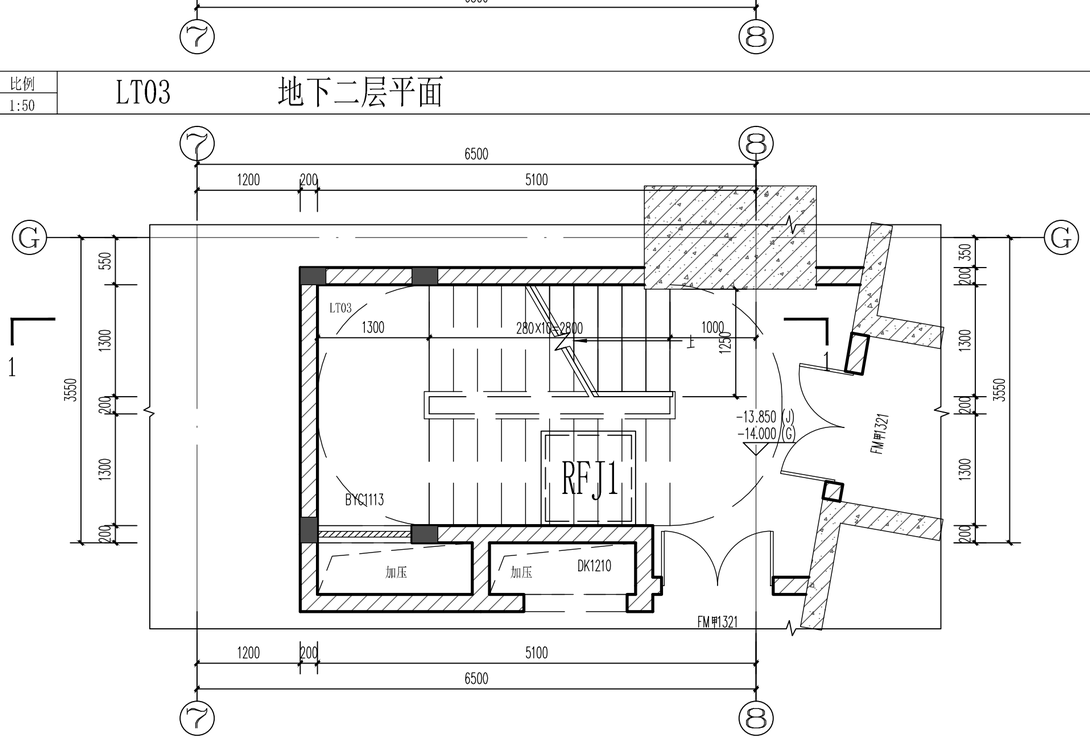

比例 1:50　LT03　地下三层平面

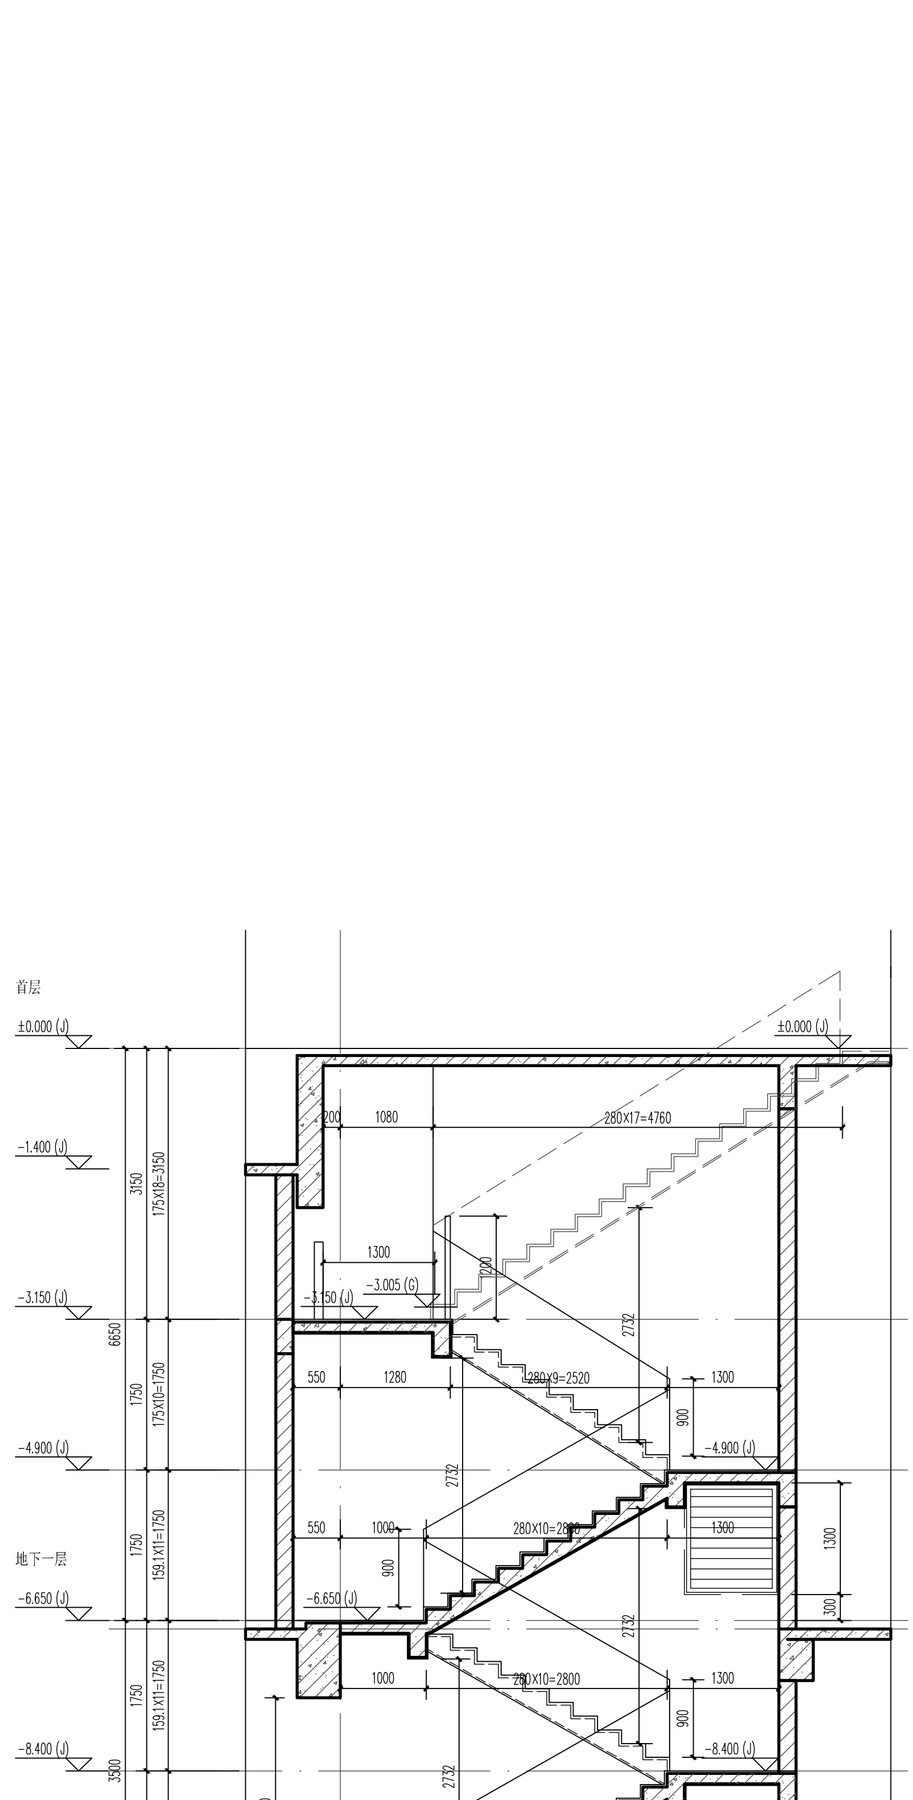

比例 1:50　LT03　1-1剖面

版本号	日期	修改内容	修订者

图纸条码

院总工程师	赵松林	
审定	黄孝颖	
审核	张林汉	
设总负责人	张林汉	
专业负责人	宋延勇	
校核	石昊洋	
设计	胡伟航	

建设单位：佛山市禅城区保宸置业有限公司

工程名称：保利天珺秀台7#

业务号：21-347　专业：建筑

设计阶段：施工图


图纸名称：LT03 楼梯大样图

图号：J-1-LT05　版号：

出图日期：2023.08.02　序号：

版权所有，不得复制、套用或公开。
ALL RIGHTS RESERVED.

平面位置示意 Key Plan

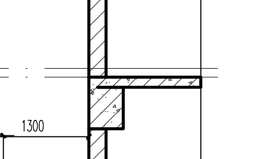

广州市设计院集团有限公司
GUANGZHOU DESIGN INSTITUTE GROUP CO.,LTD.
工程设计甲级资质证书编号：A244007378
工程勘察甲级资质证书编号：B244007378