




会 签 栏	建 筑	宋廷勇			暖 通	陈少玲		
	结 构	邓艳青						
	给 排 水	甘兆麟						
	电 气	蔡泽钢						

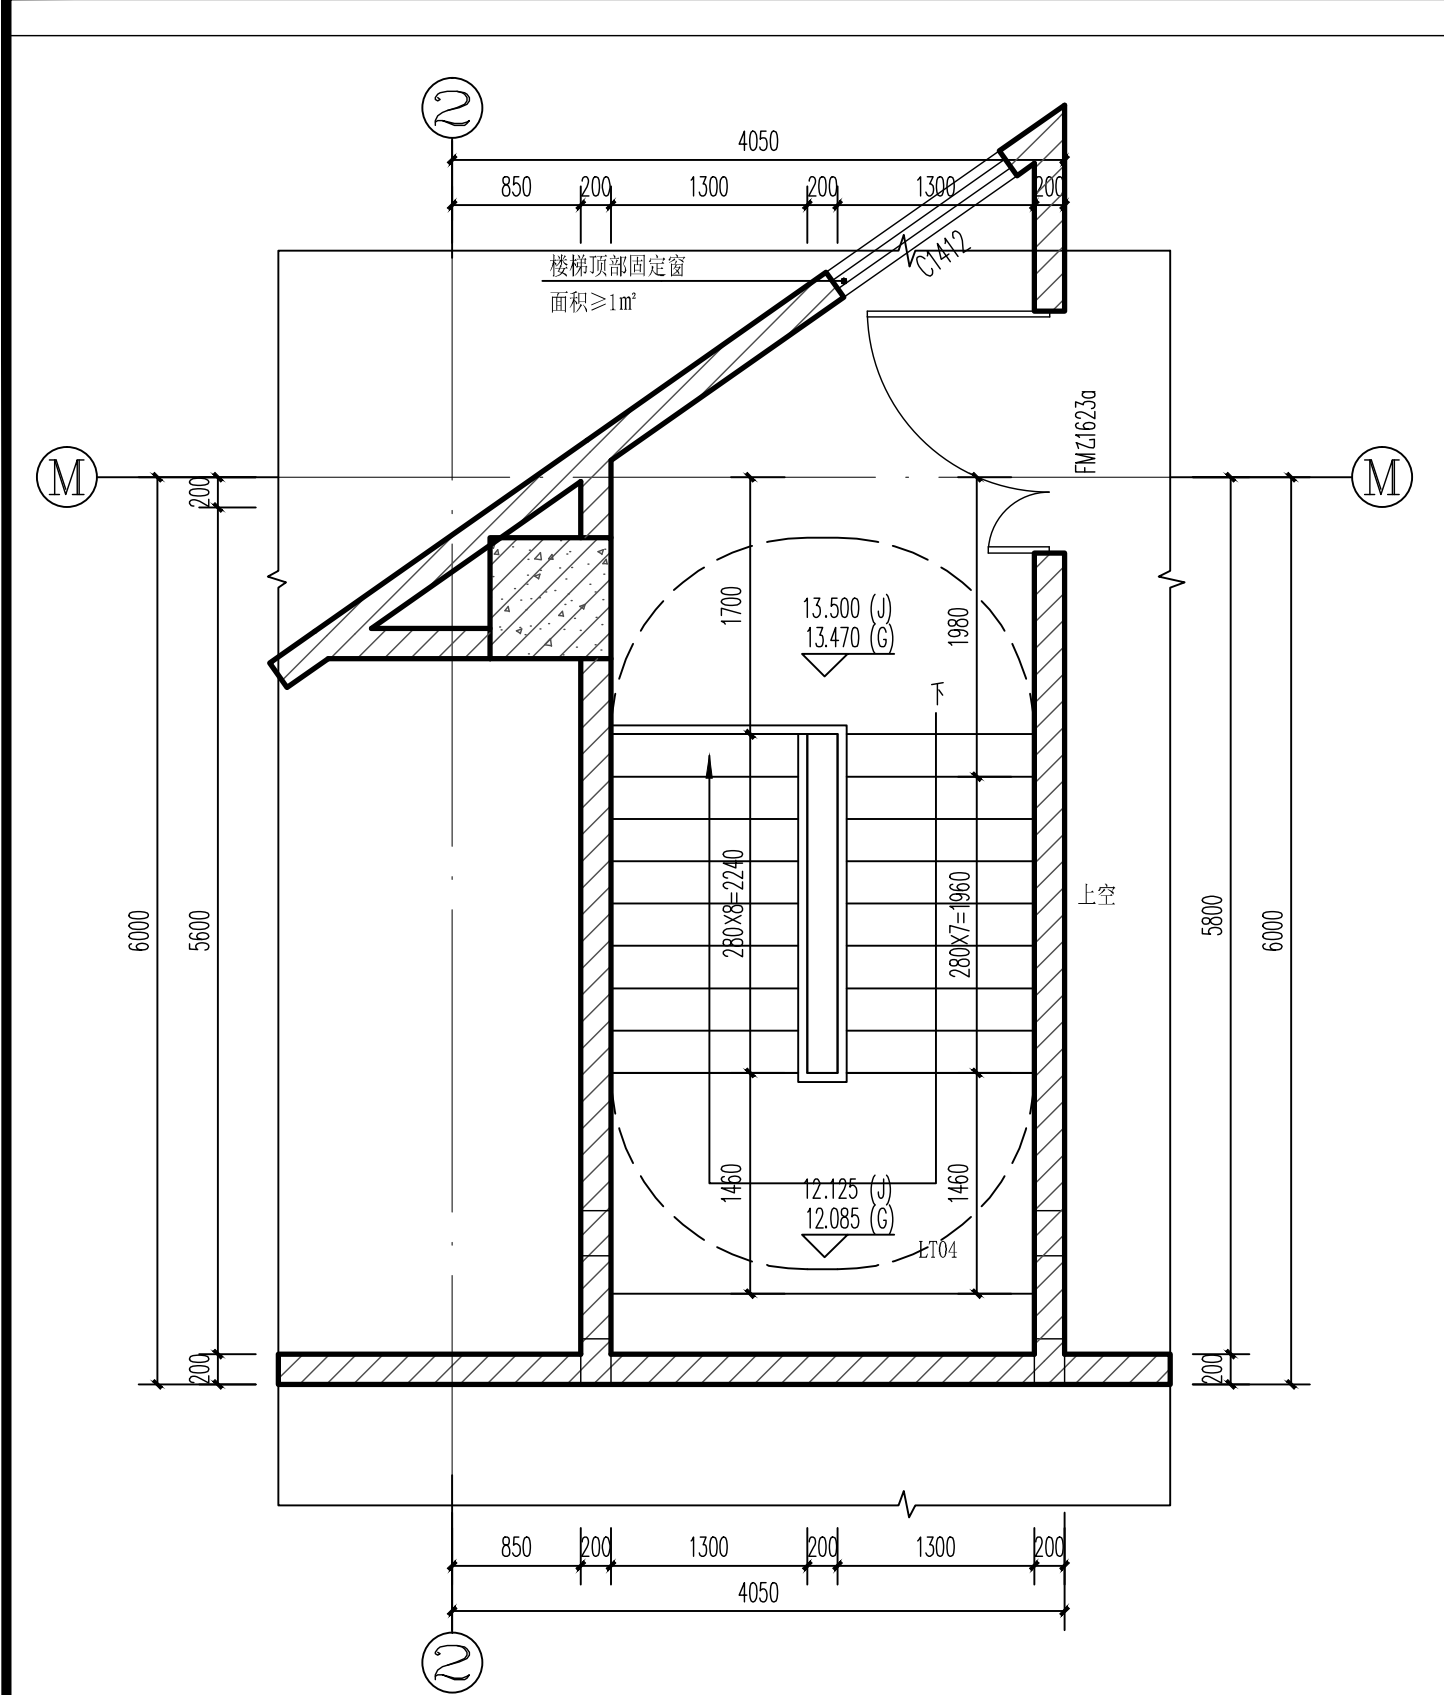


比例	LT04	三层平面
1:50		

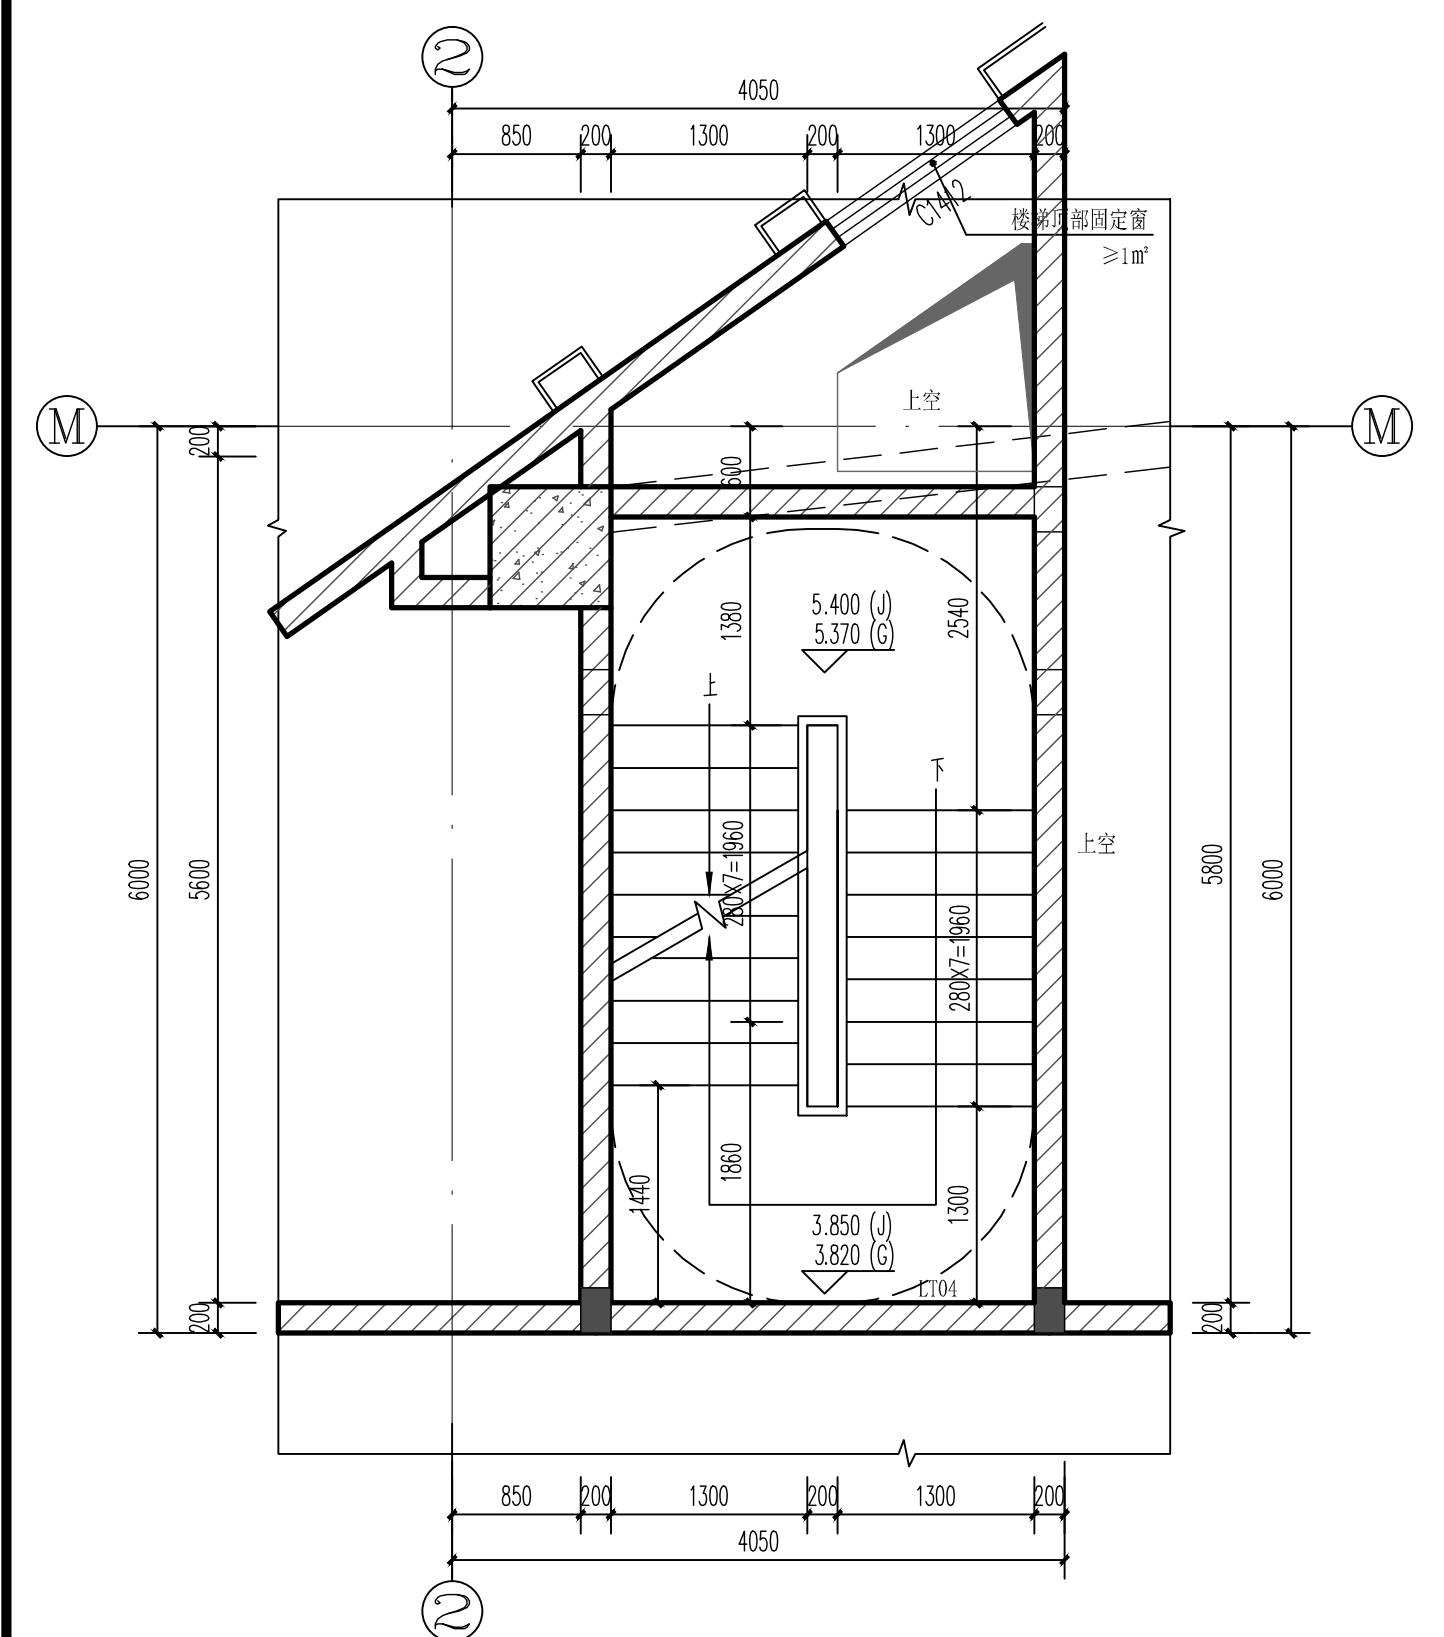


比例	LT04	5.400m标高平面
1:50		

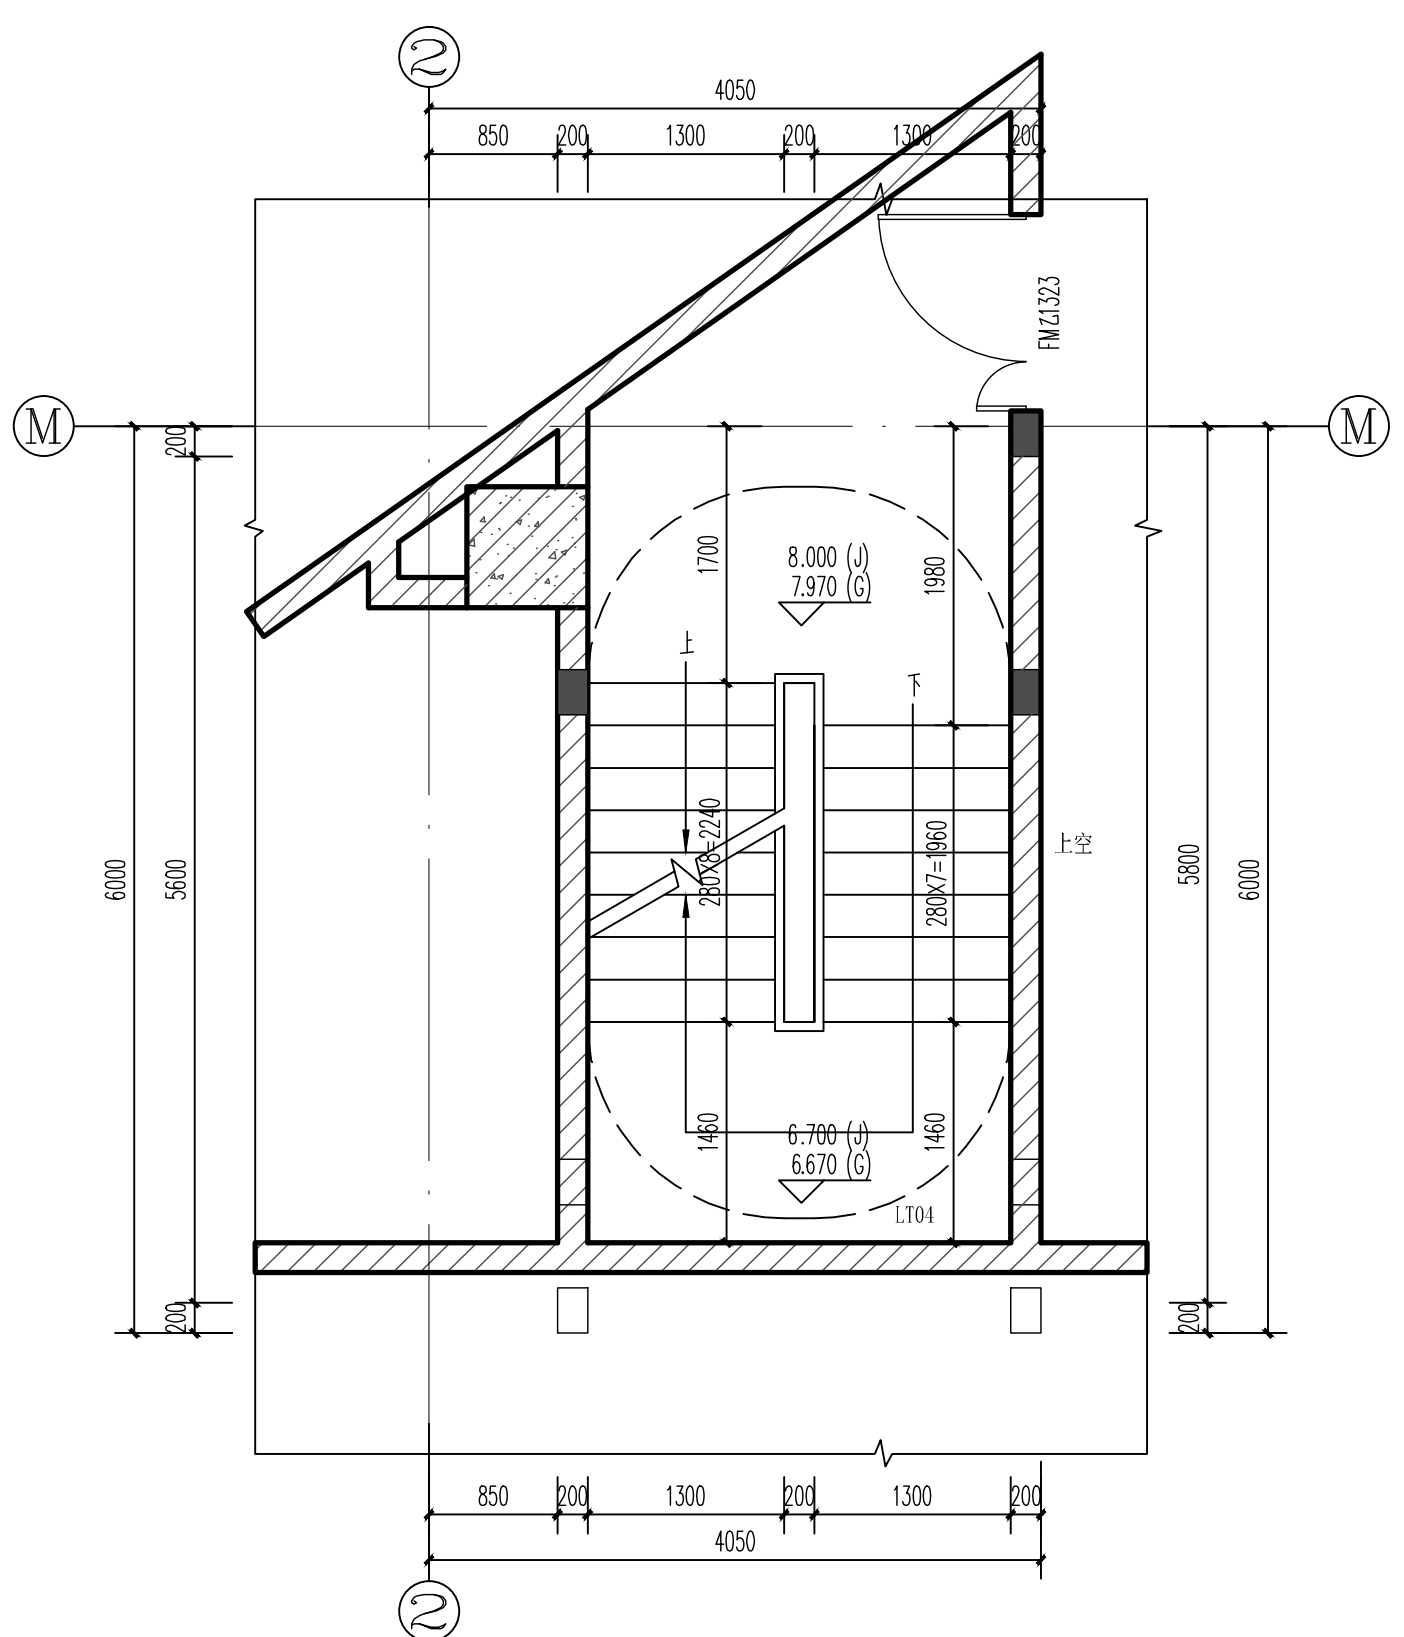


比例	LT04	5.400m标高平面	比例	LT04	二层平面
1:50			1:50		

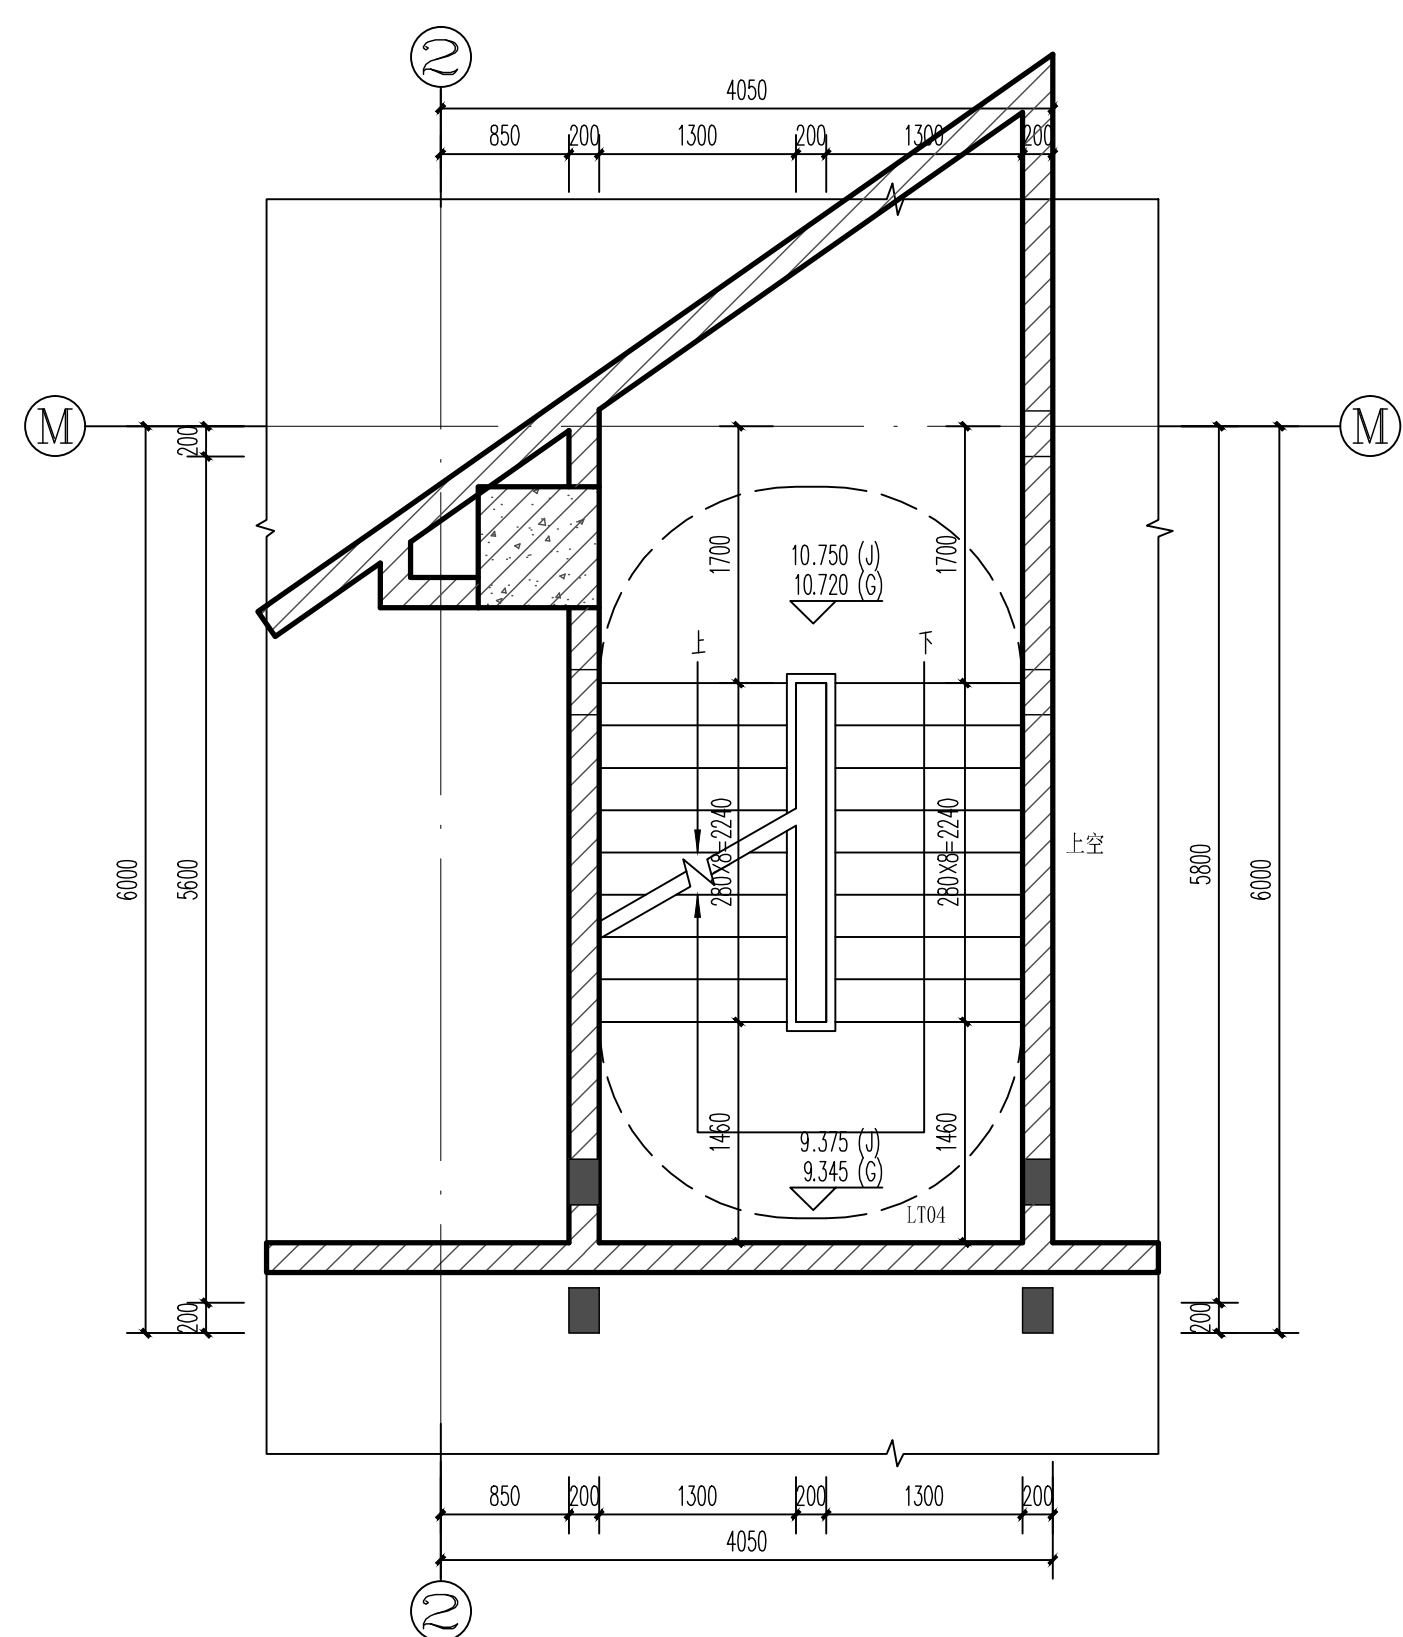


比例	LT04	10.750标高平面
1:50		

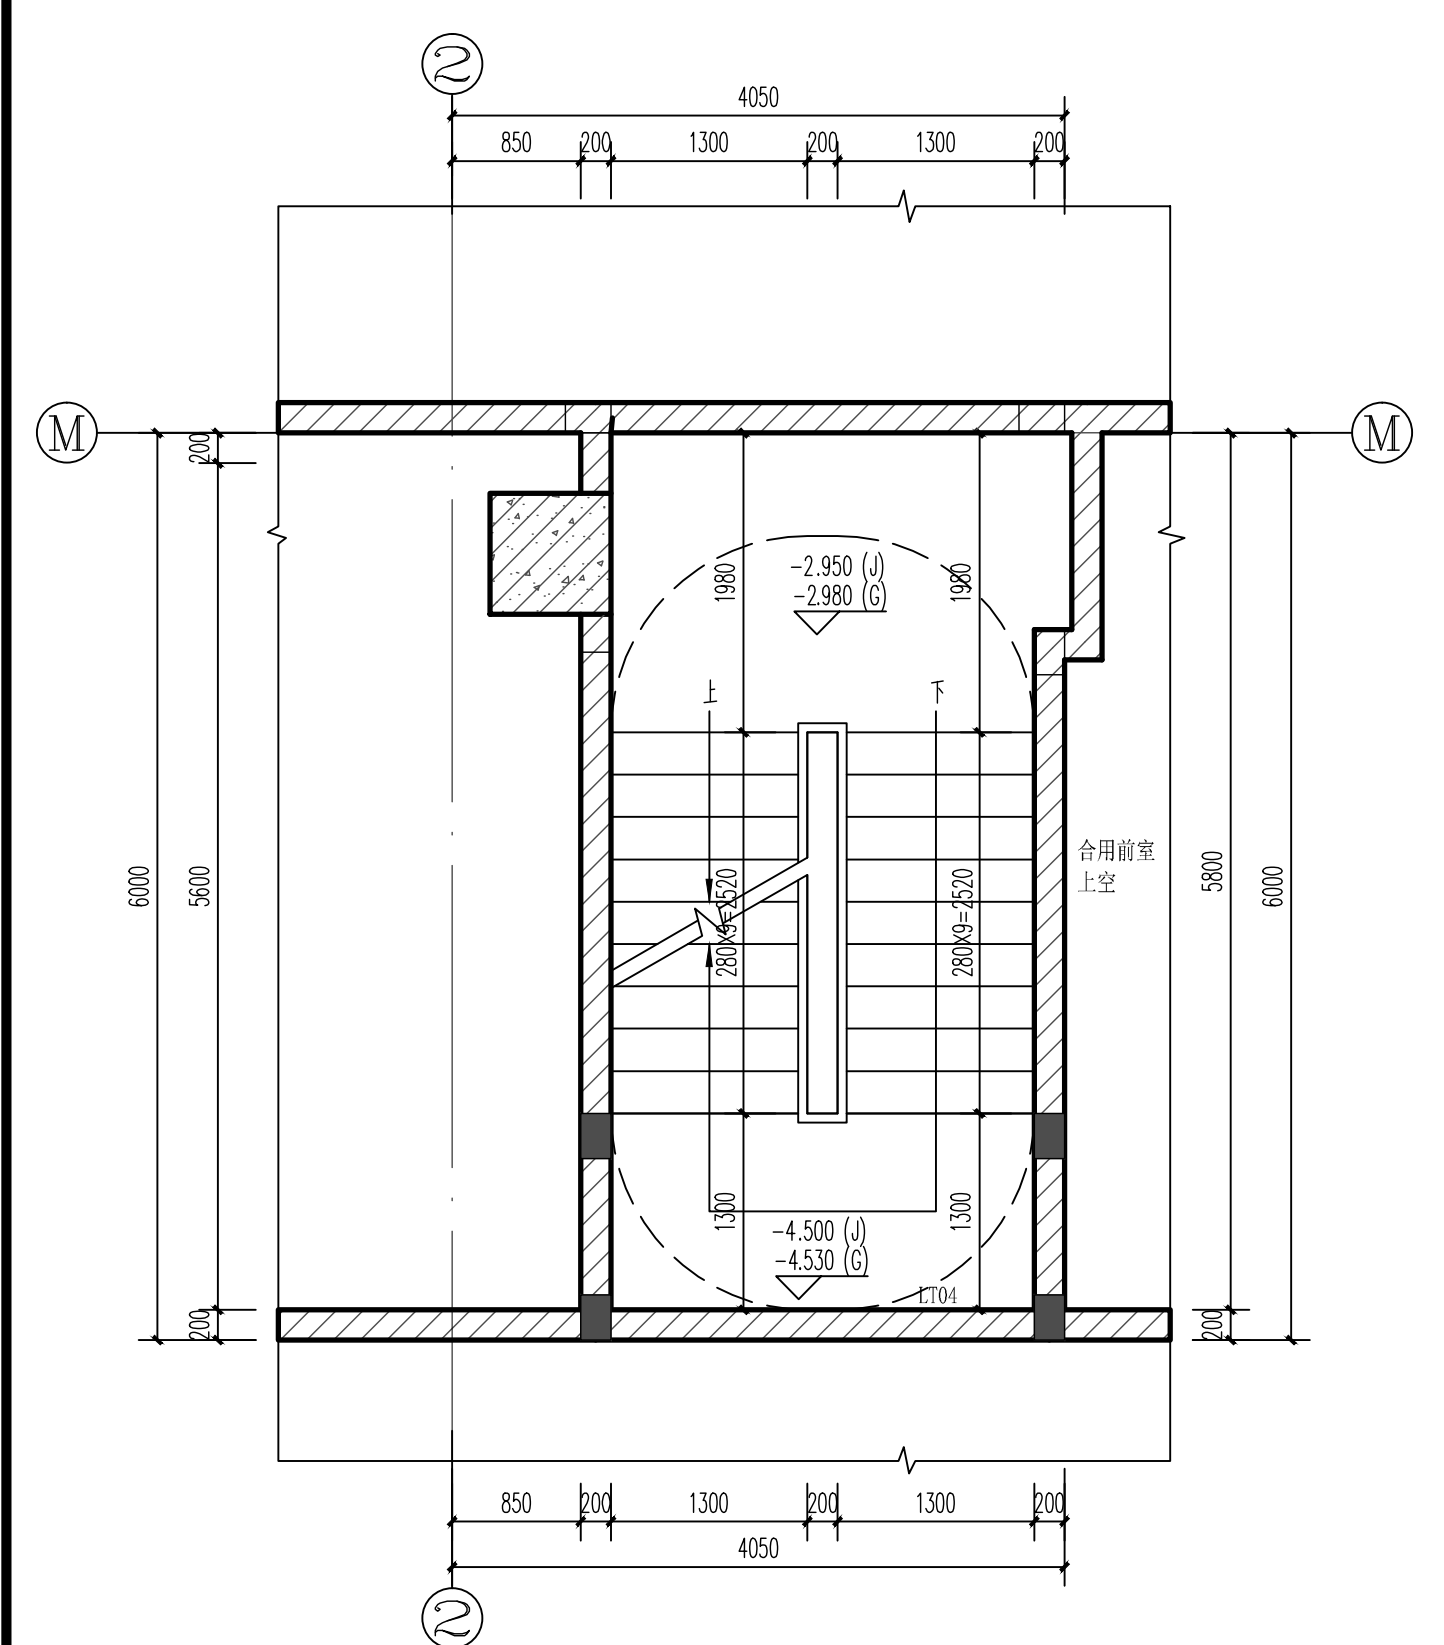


比例	LT04	-2.950m标高平面
1:50		

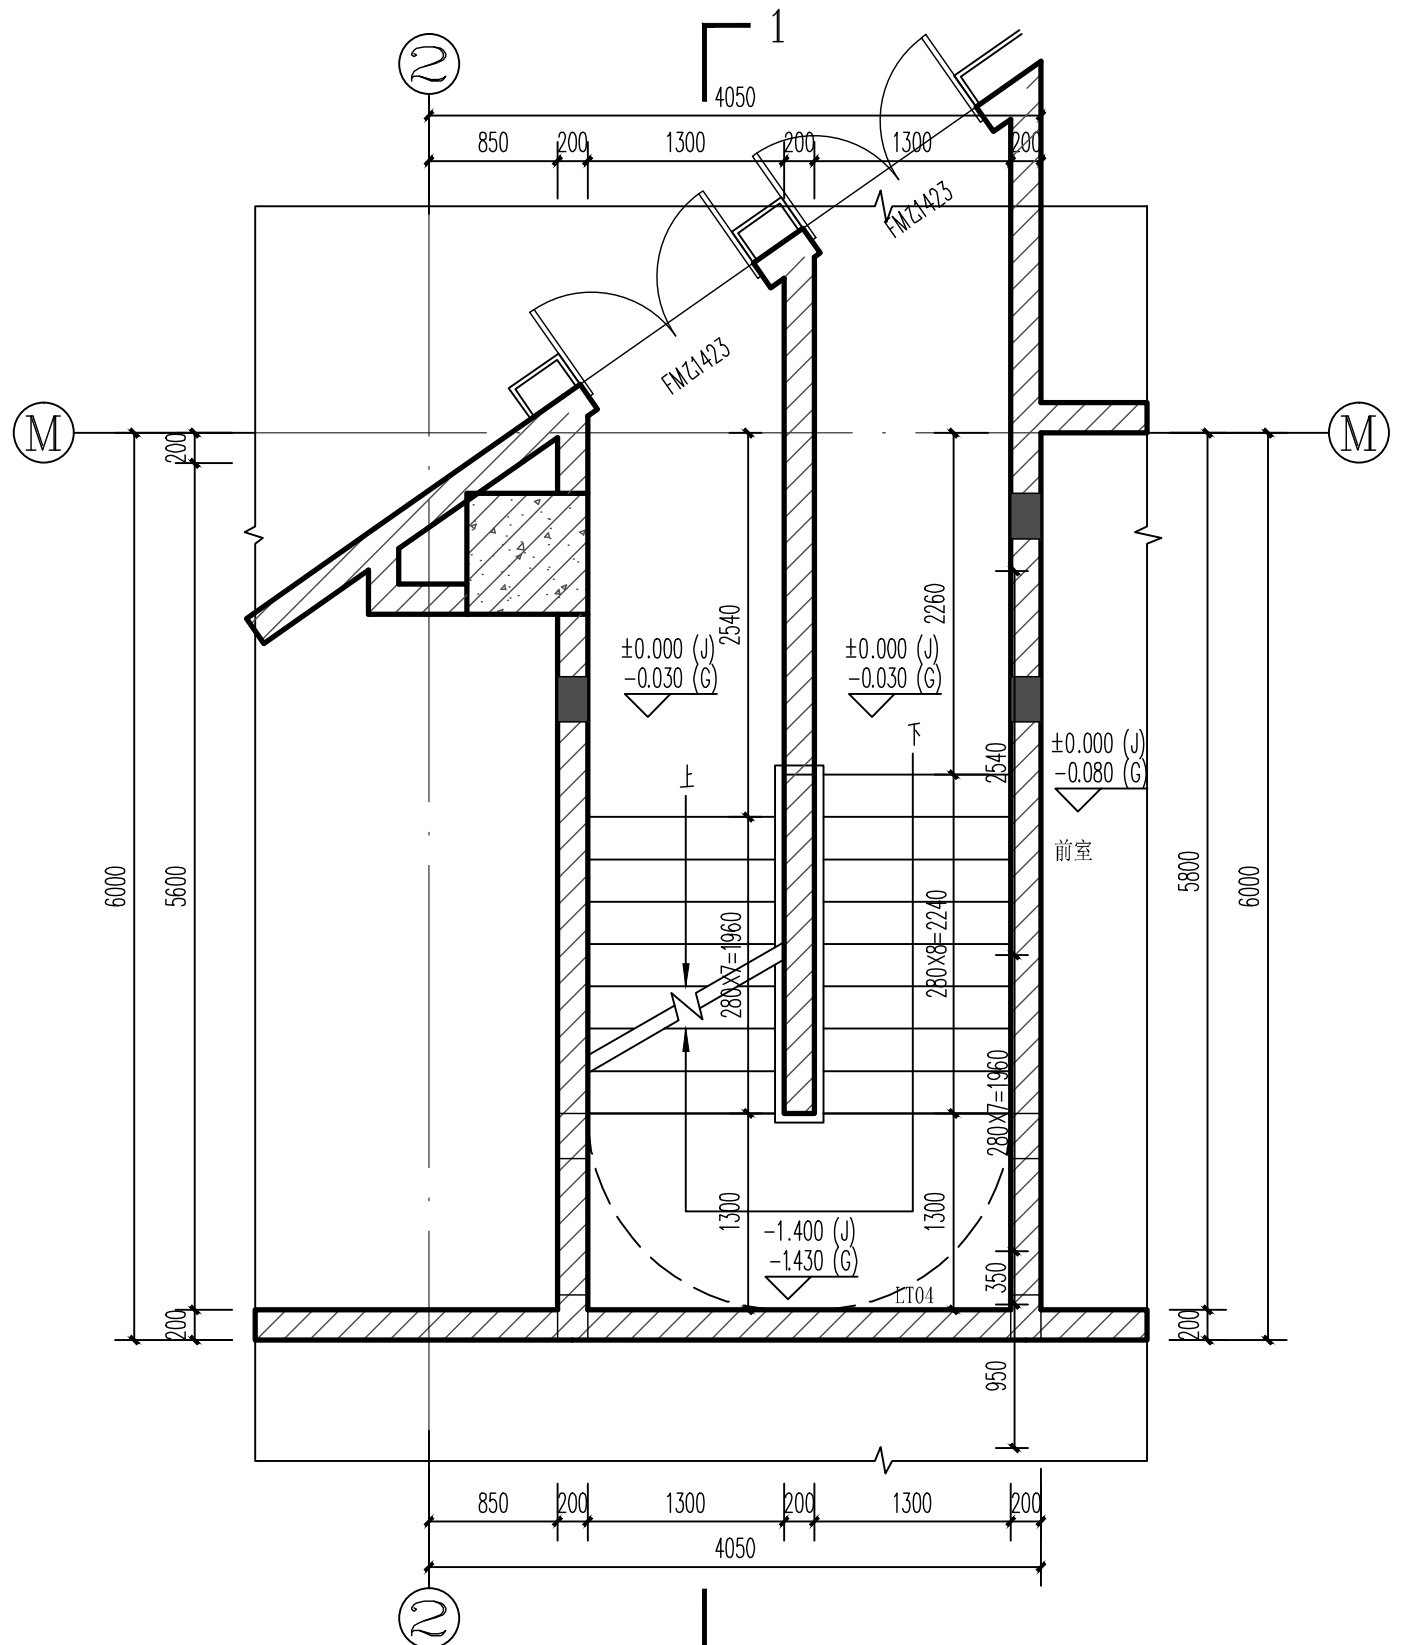


比例 1:50	LT04	-2.950m标高平面	比例 1:50	LT04	首层平面
------------	------	-------------	------------	------	------

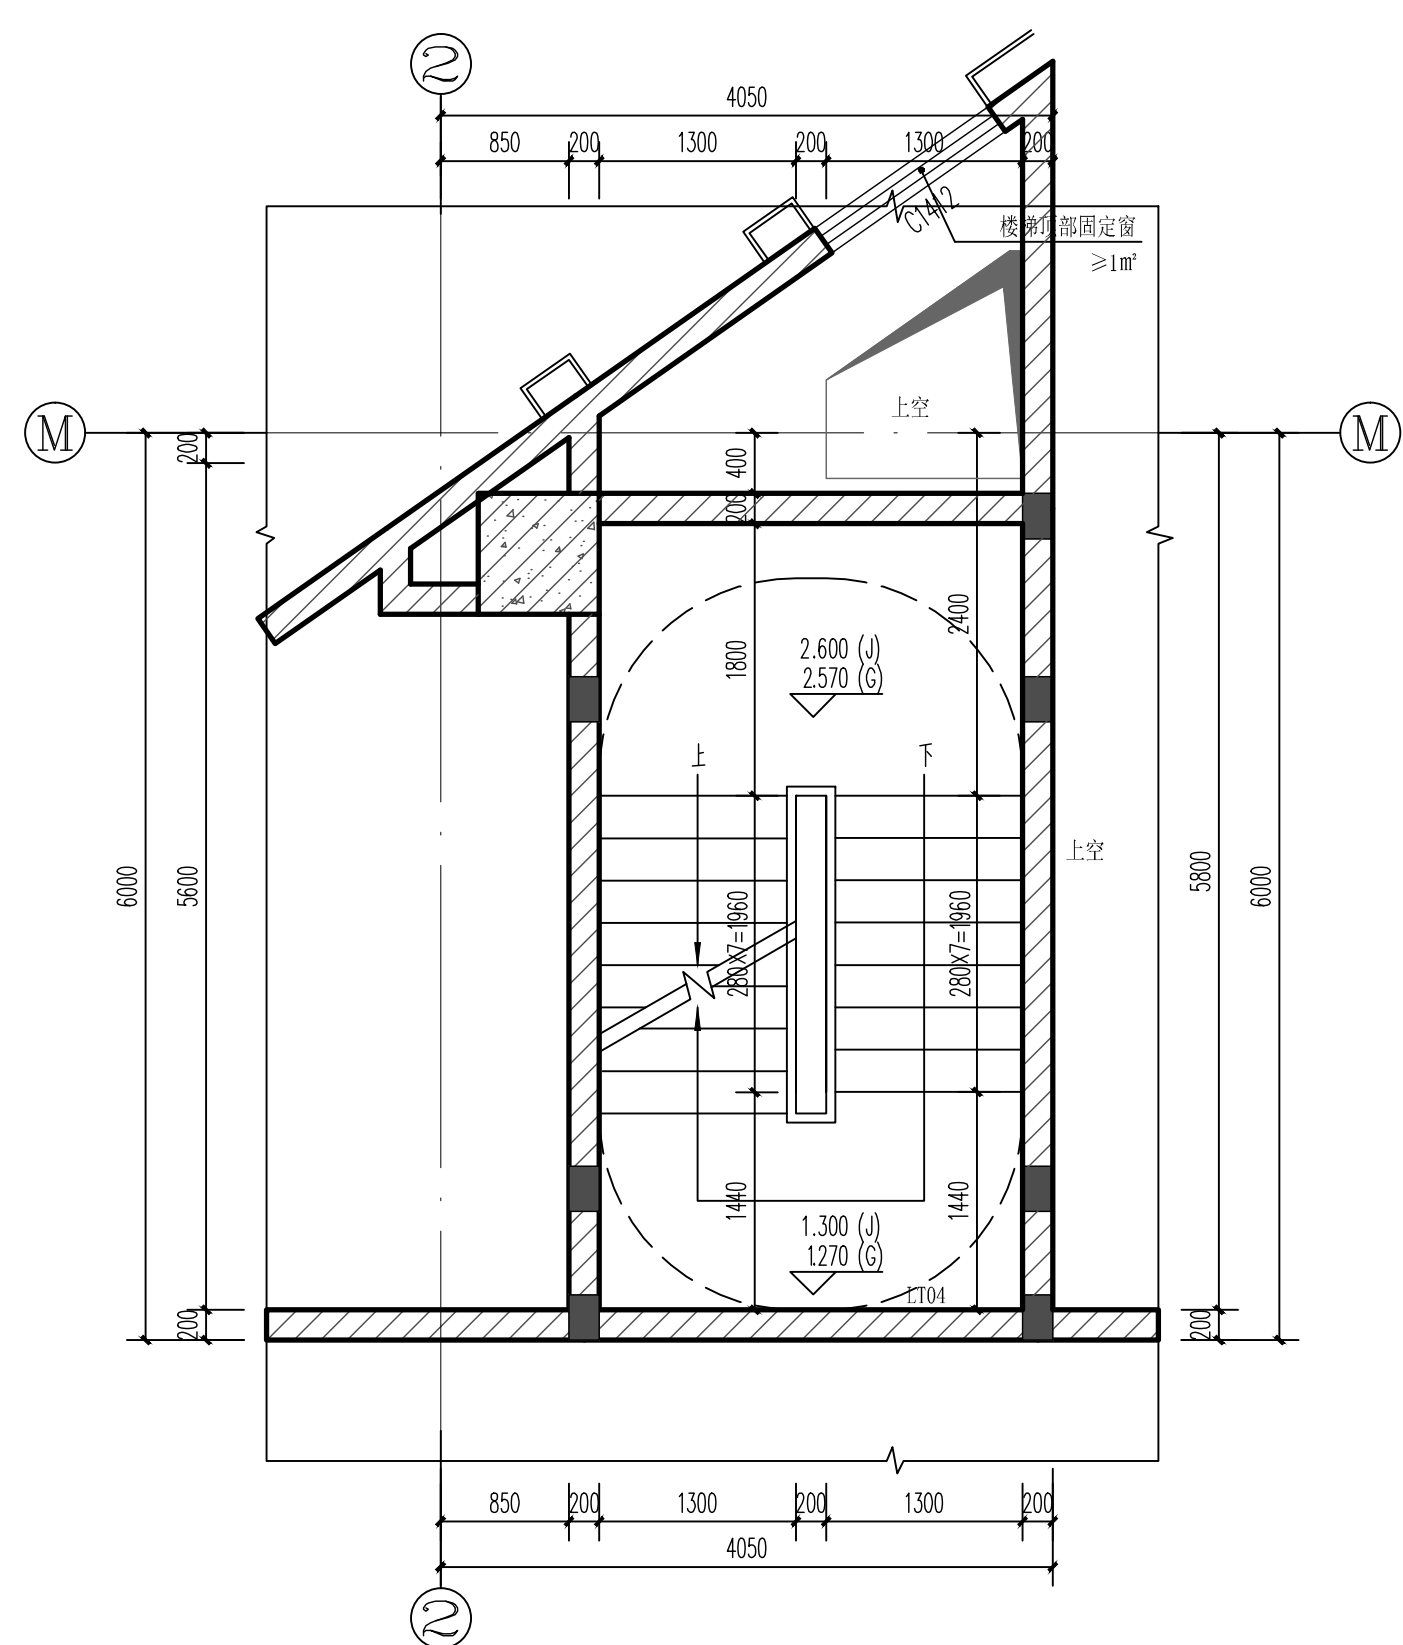


比例	LT04	2.600m标高平面
1:50		

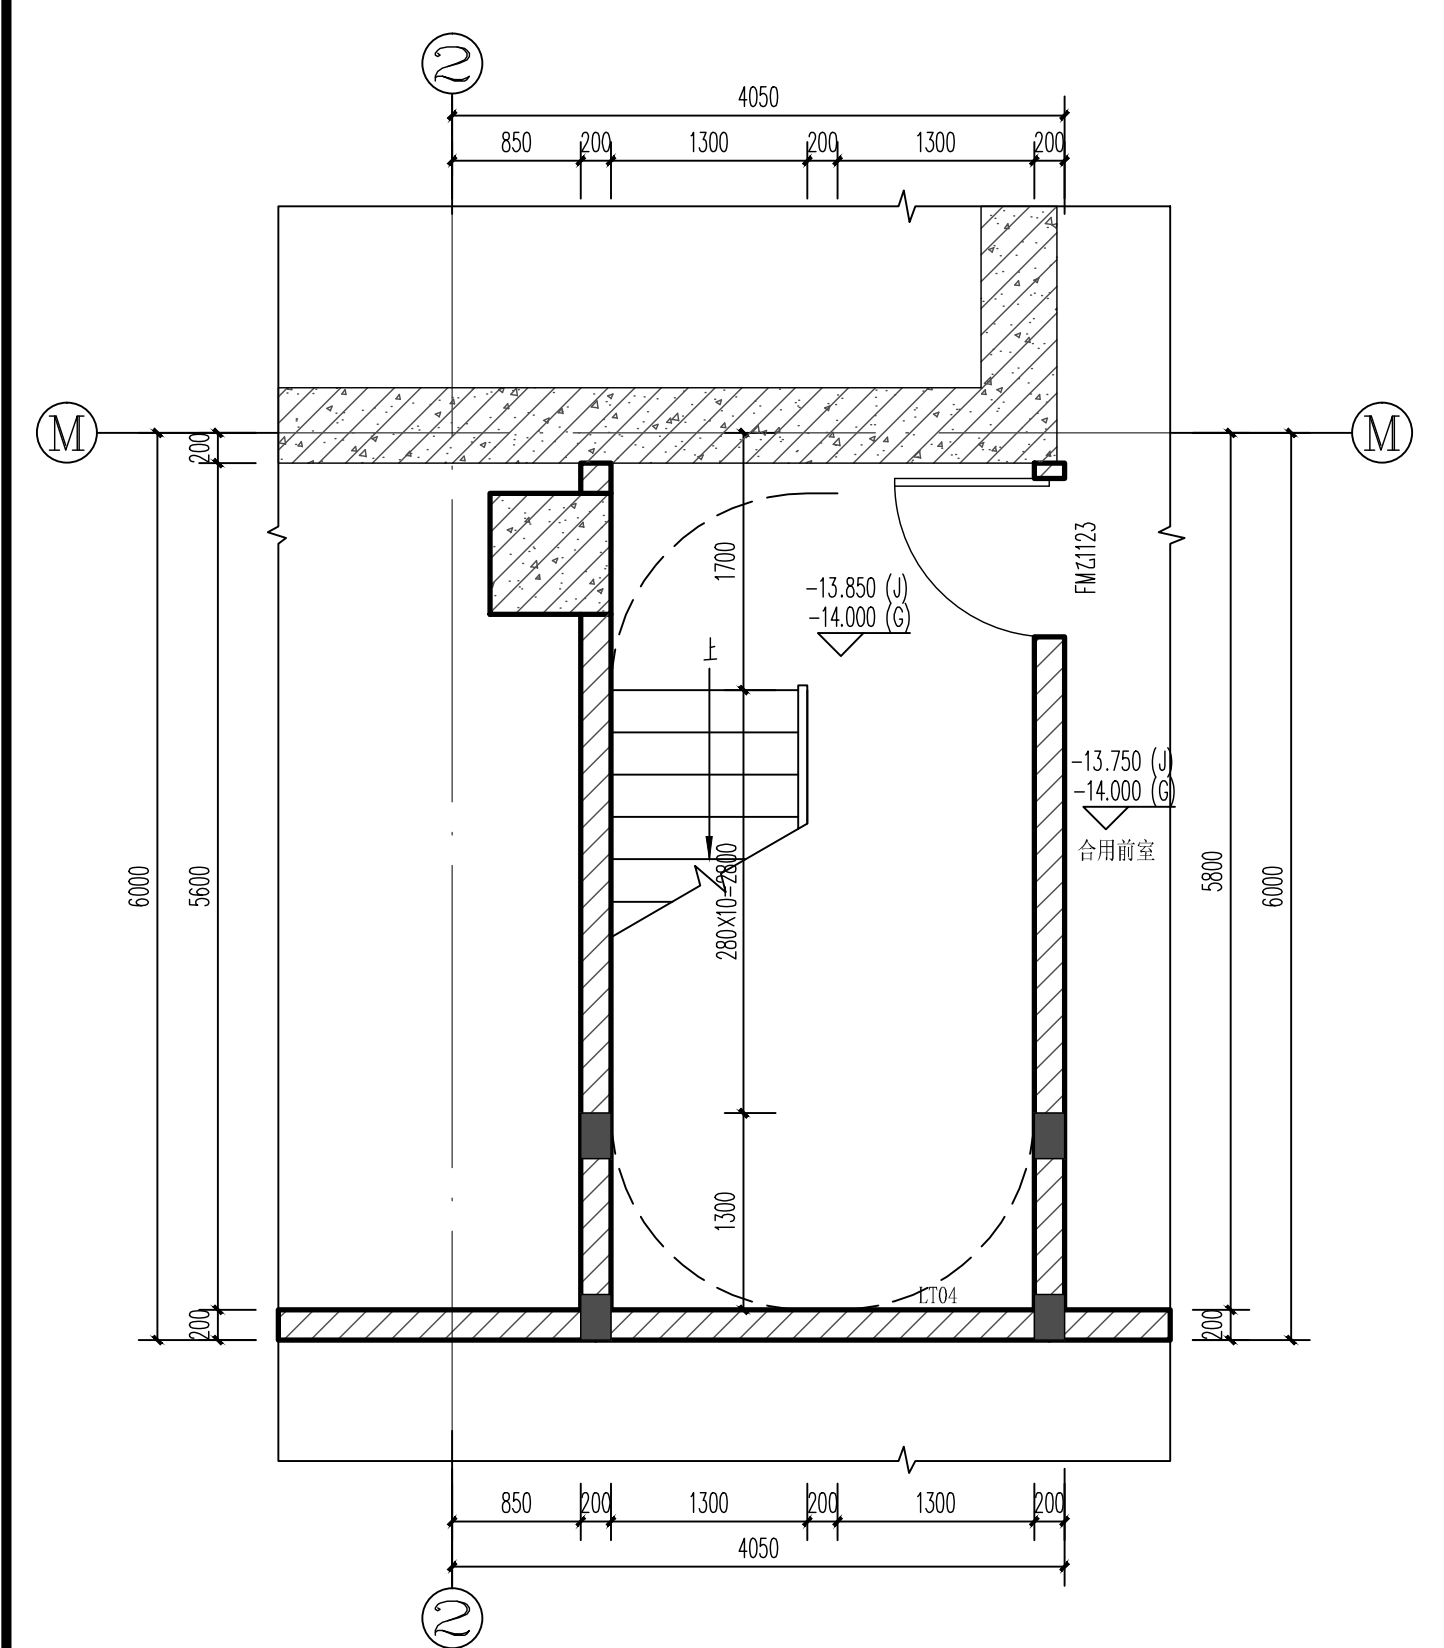

比例	LT04	地下三层平面
1:50		

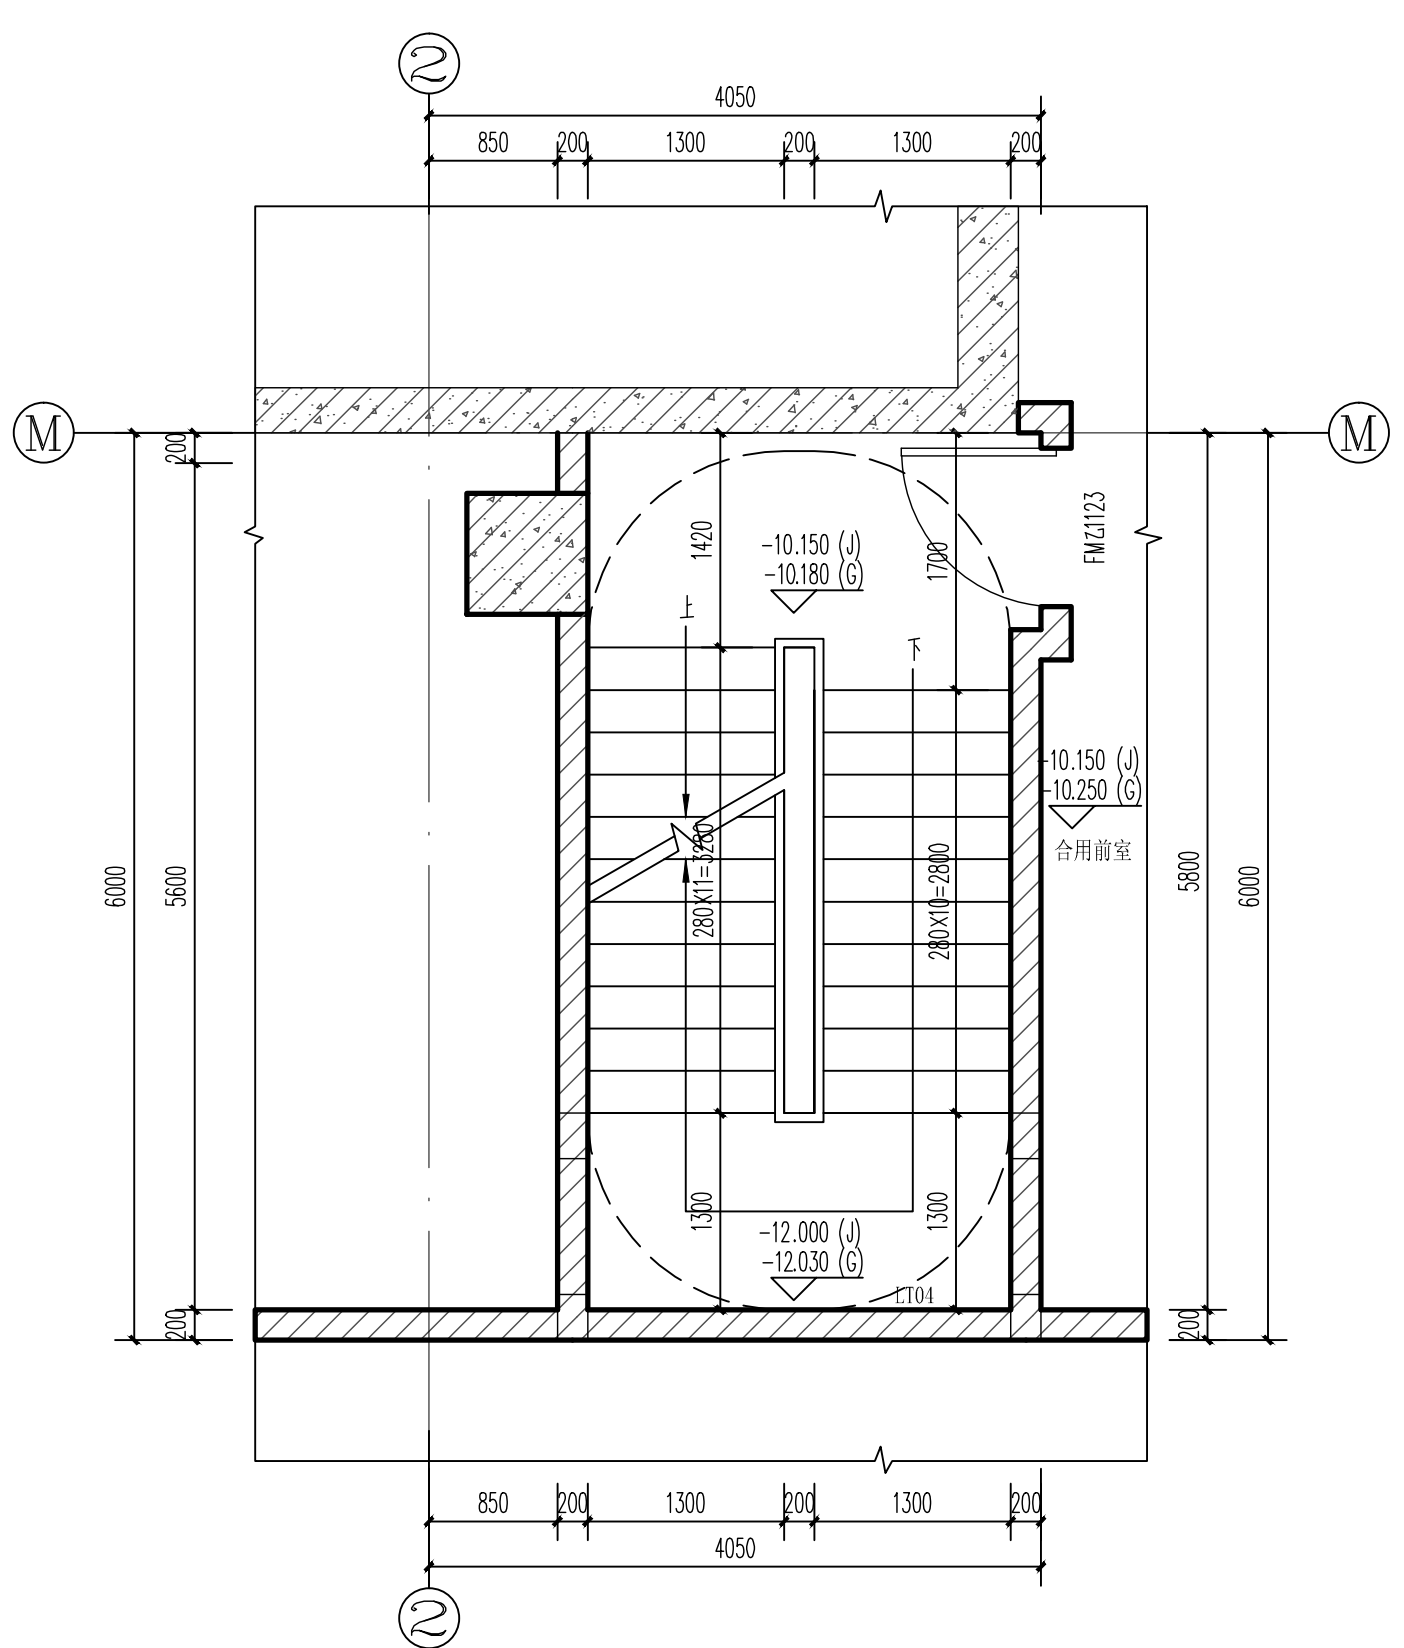

比例 1:50	LT04 地下三层平面	比例 1:50	LT04 地下二层平面
------------	-------------	------------	-------------

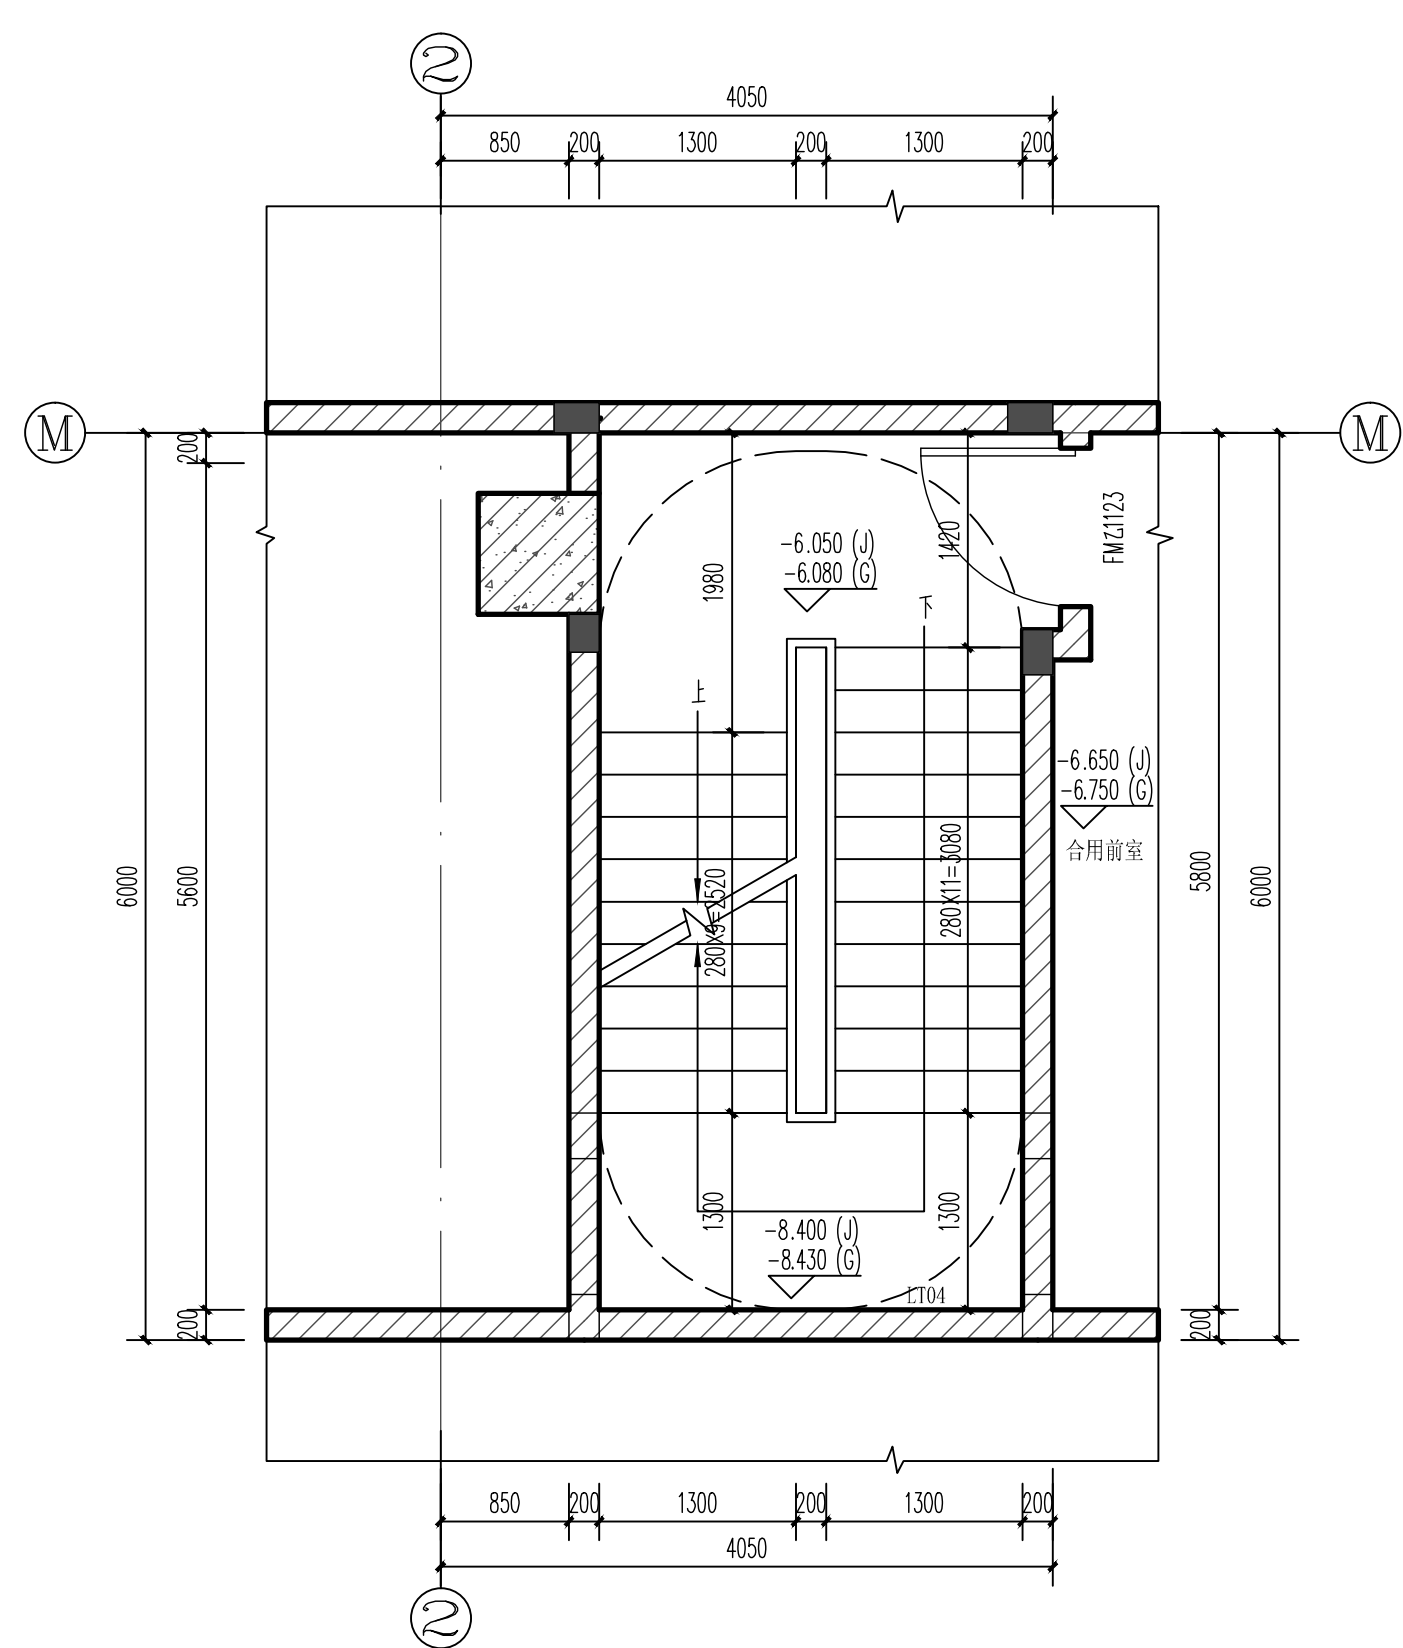

比例	LT04	地下一层平面
1:50		

[illegible]