会签栏								
建　筑	宋延勇			暖　通	陈少玲		
结　构	邓艳青						
给排水	甘兆麟						
电　气	蔡泽炯						

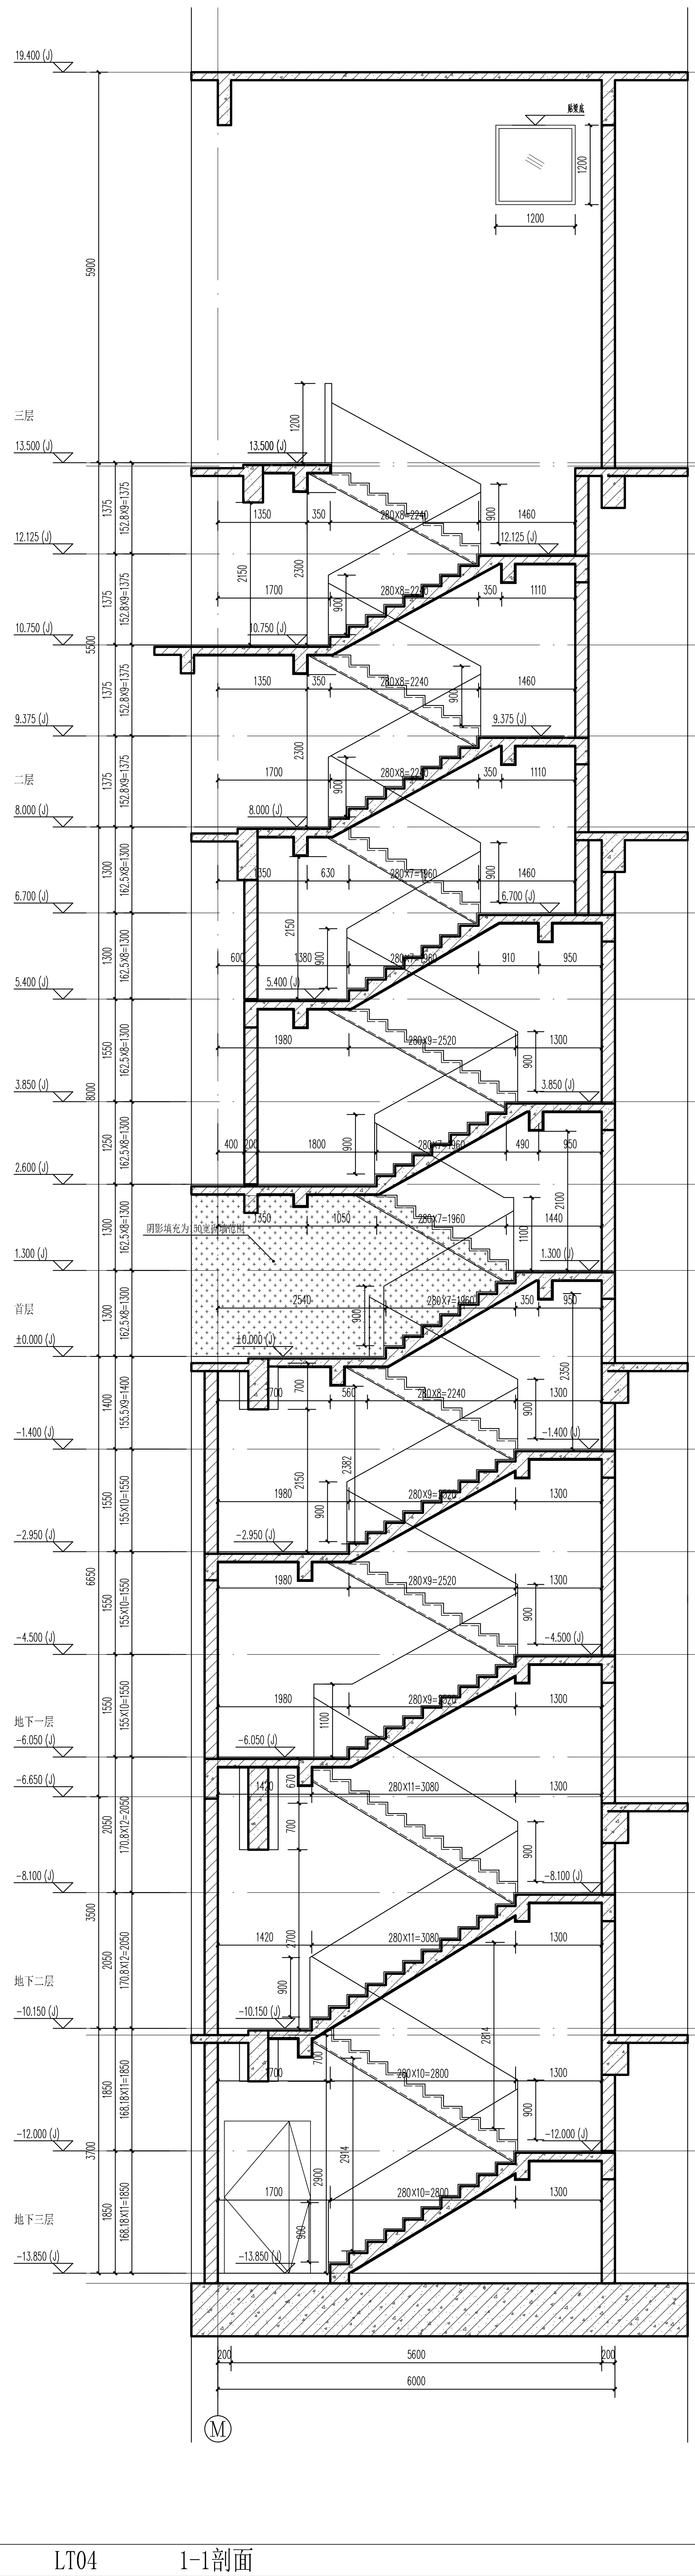

比例 1:50

LT04　　1-1剖面

院总工程师	赵松林
审　定	黄孝颖
审　核	张林汉
设　计 总负责人	黄孝颖 张林汉
专业负责人	宋延勇
校　核	石昊洋
设　计	胡伟航

图纸条码

版本号 | 日期 | 修改内容 | 修订者

修订栏

建设单位	佛山市禅城区保宸置业有限公司
工程名称	保利天珺秀台7#
业务号	21-347
专业	建筑
设计阶段	施工图
图纸名称	LT04 楼梯大样图（二）
图号	J-1-LT07
版本号	
出图日期	2023.08.02
序号	

版权所有，不得复制、套用或公开。
ALL RIGHTS RESERVED.

平面位置示意 Key Plan

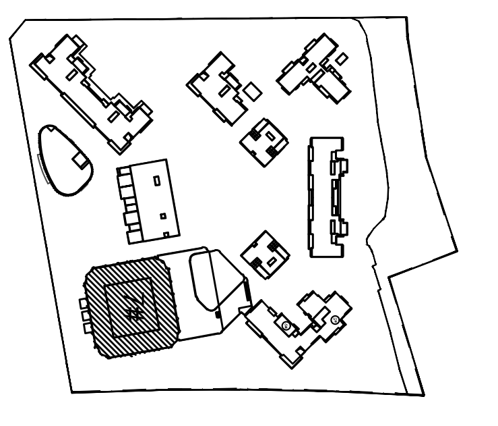

广州市设计院集团有限公司
GUANGZHOU DESIGN INSTITUTE GROUP CO.,LTD.
工程设计甲级资质证书编号：A244007378
工程勘察甲级资质证书编号：B244007378