




会	建	末延勇	暖	陈少玲			
签	筑	邓艳青	通				
栏	结	甘亮麟					
	给	蔡泽刚					
	排						
	水						
	电						
	气						

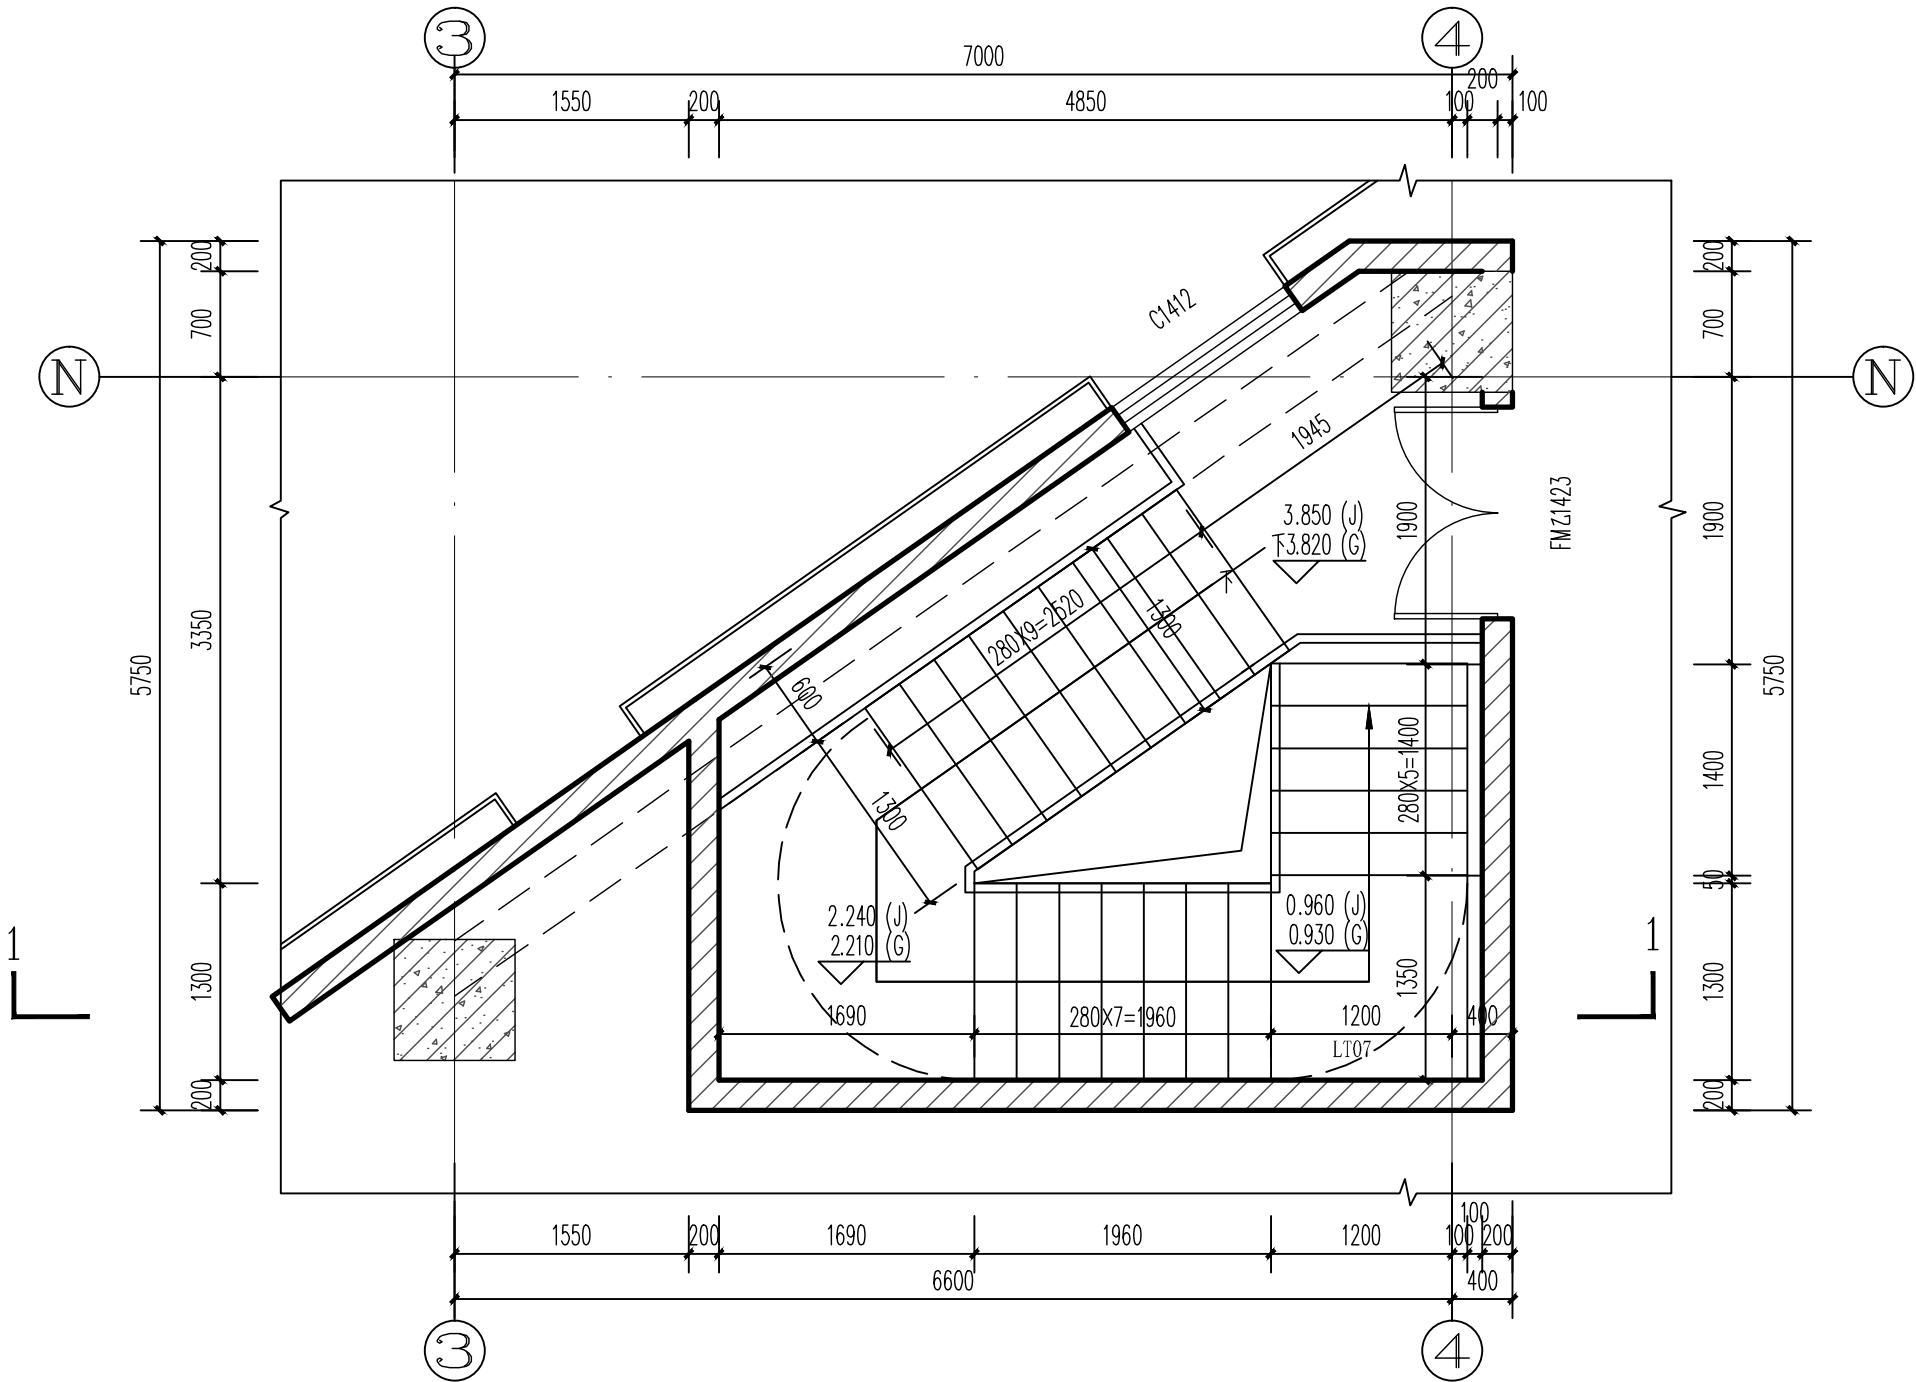


LT08 首层夹层平面

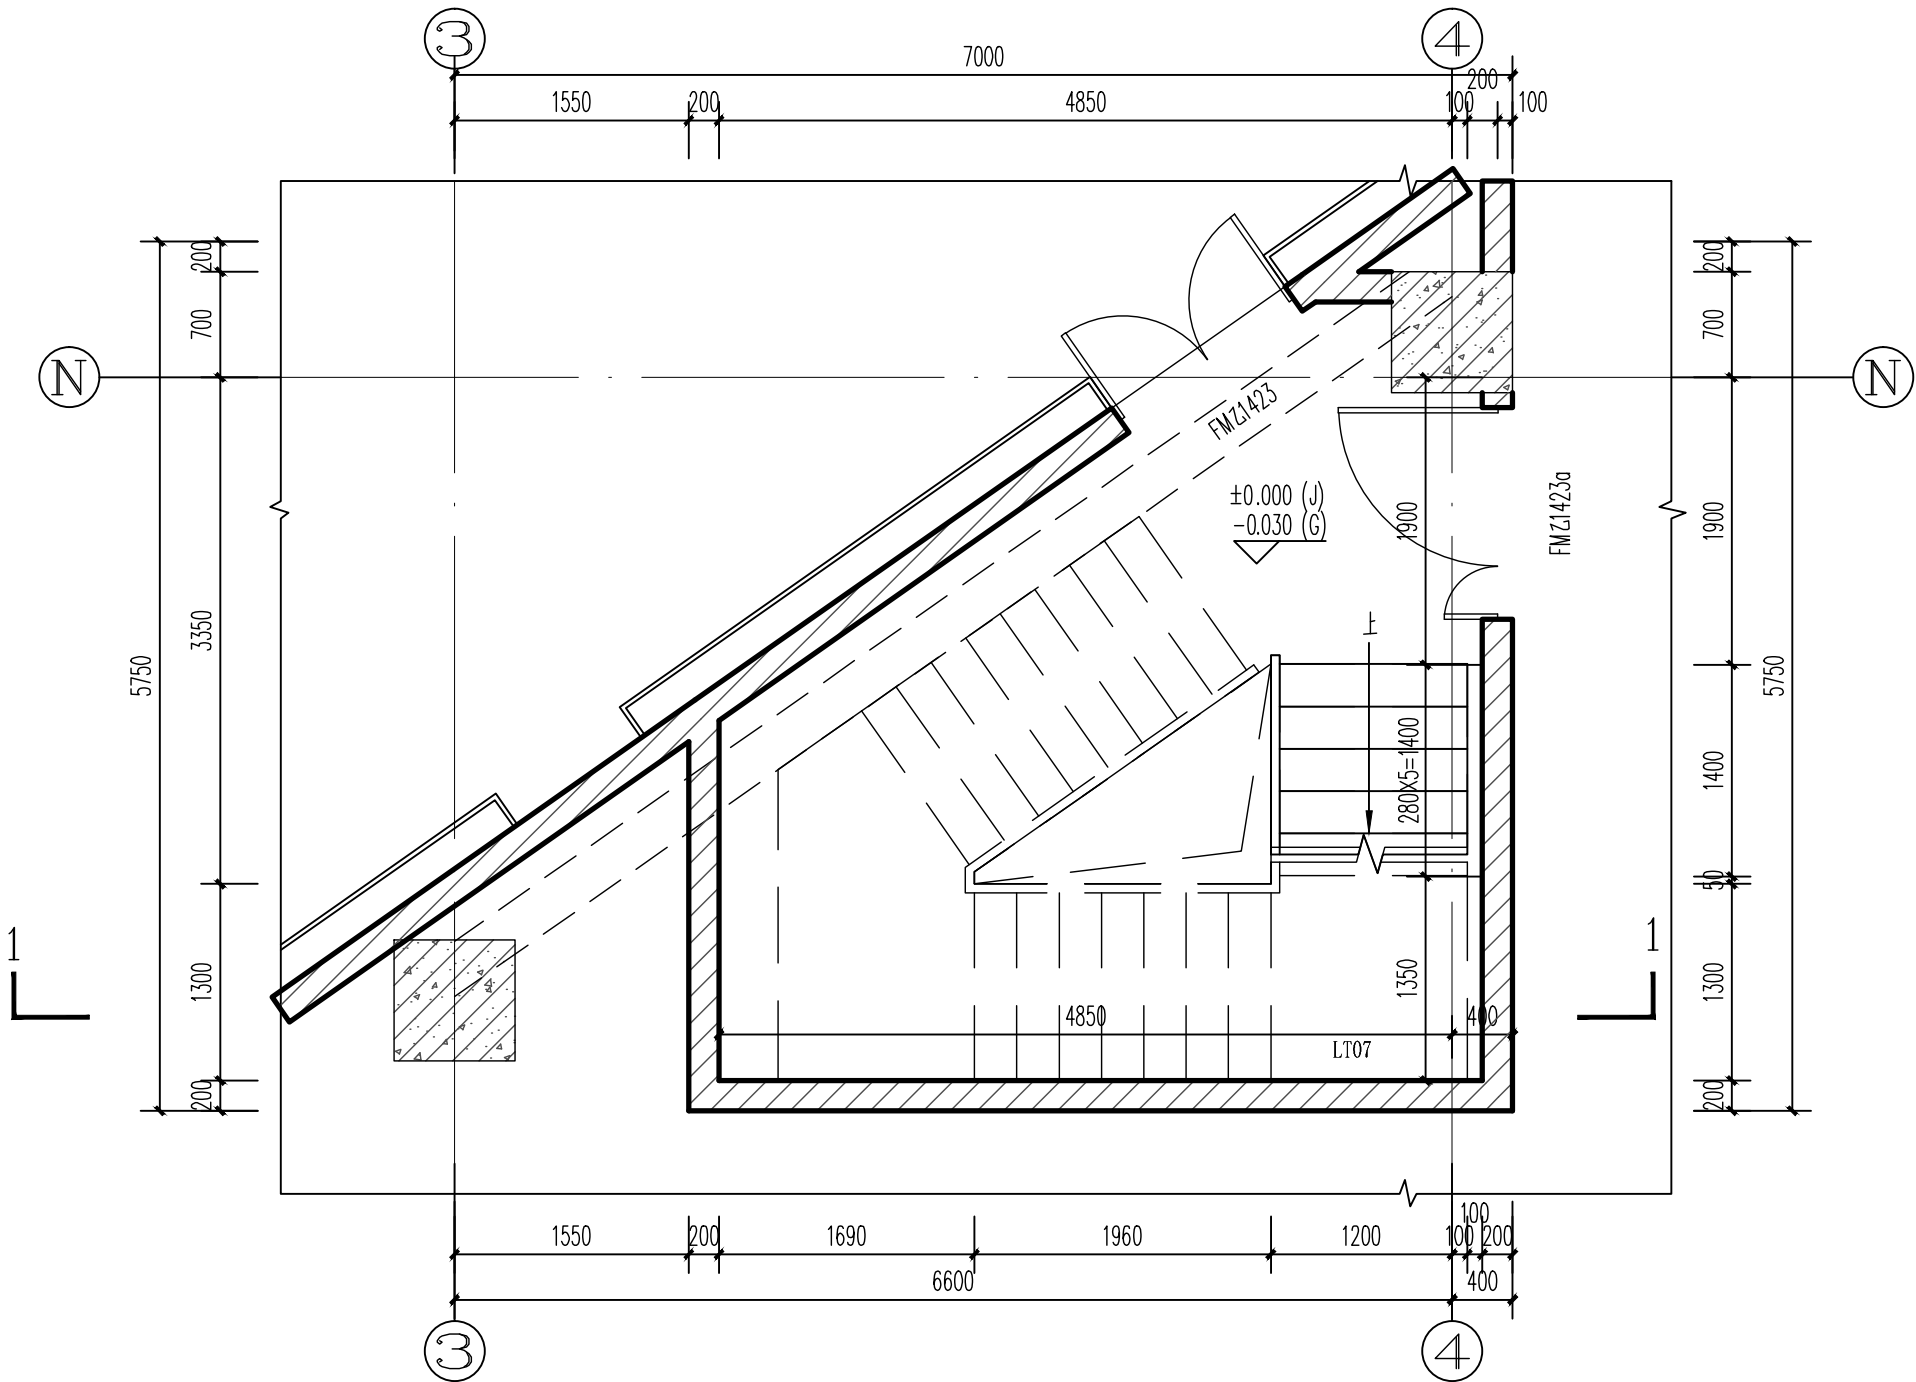

LT08 首层平面

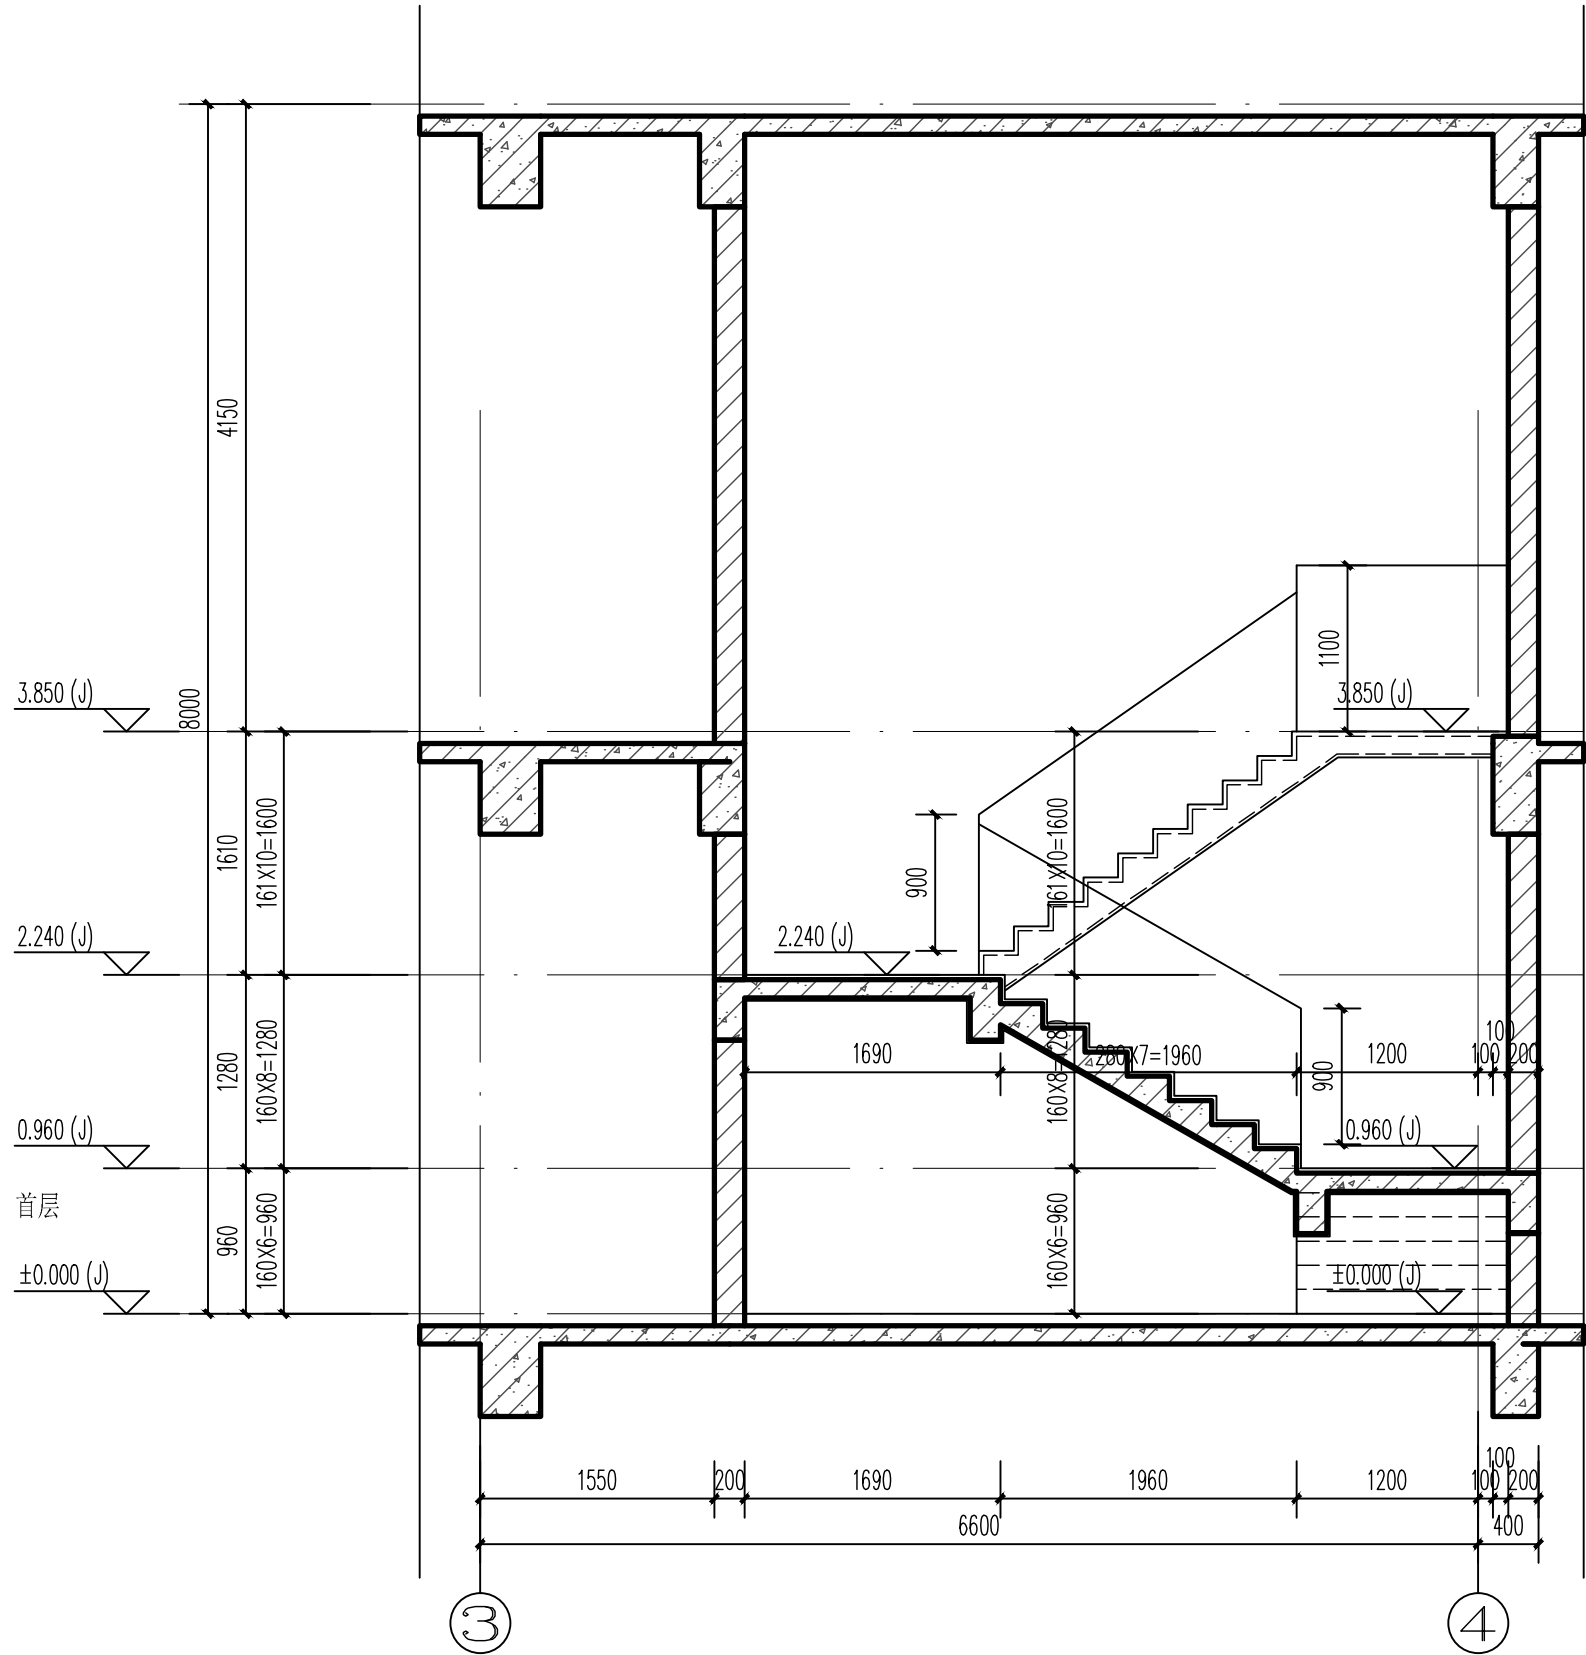

LT08 1-1剖面

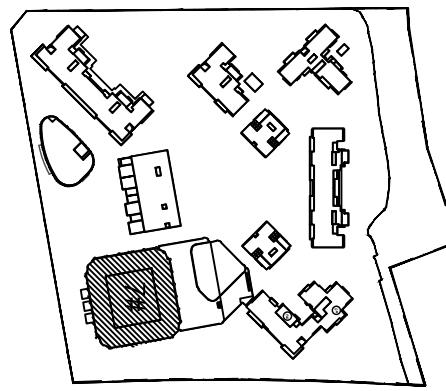

平面位置示意 Key Plan