会签栏							
建筑	宋延勇			暖通	陈少玲		
结构	邓艳青						
给排水	甘兆麟						
电气	蔡泽炯						

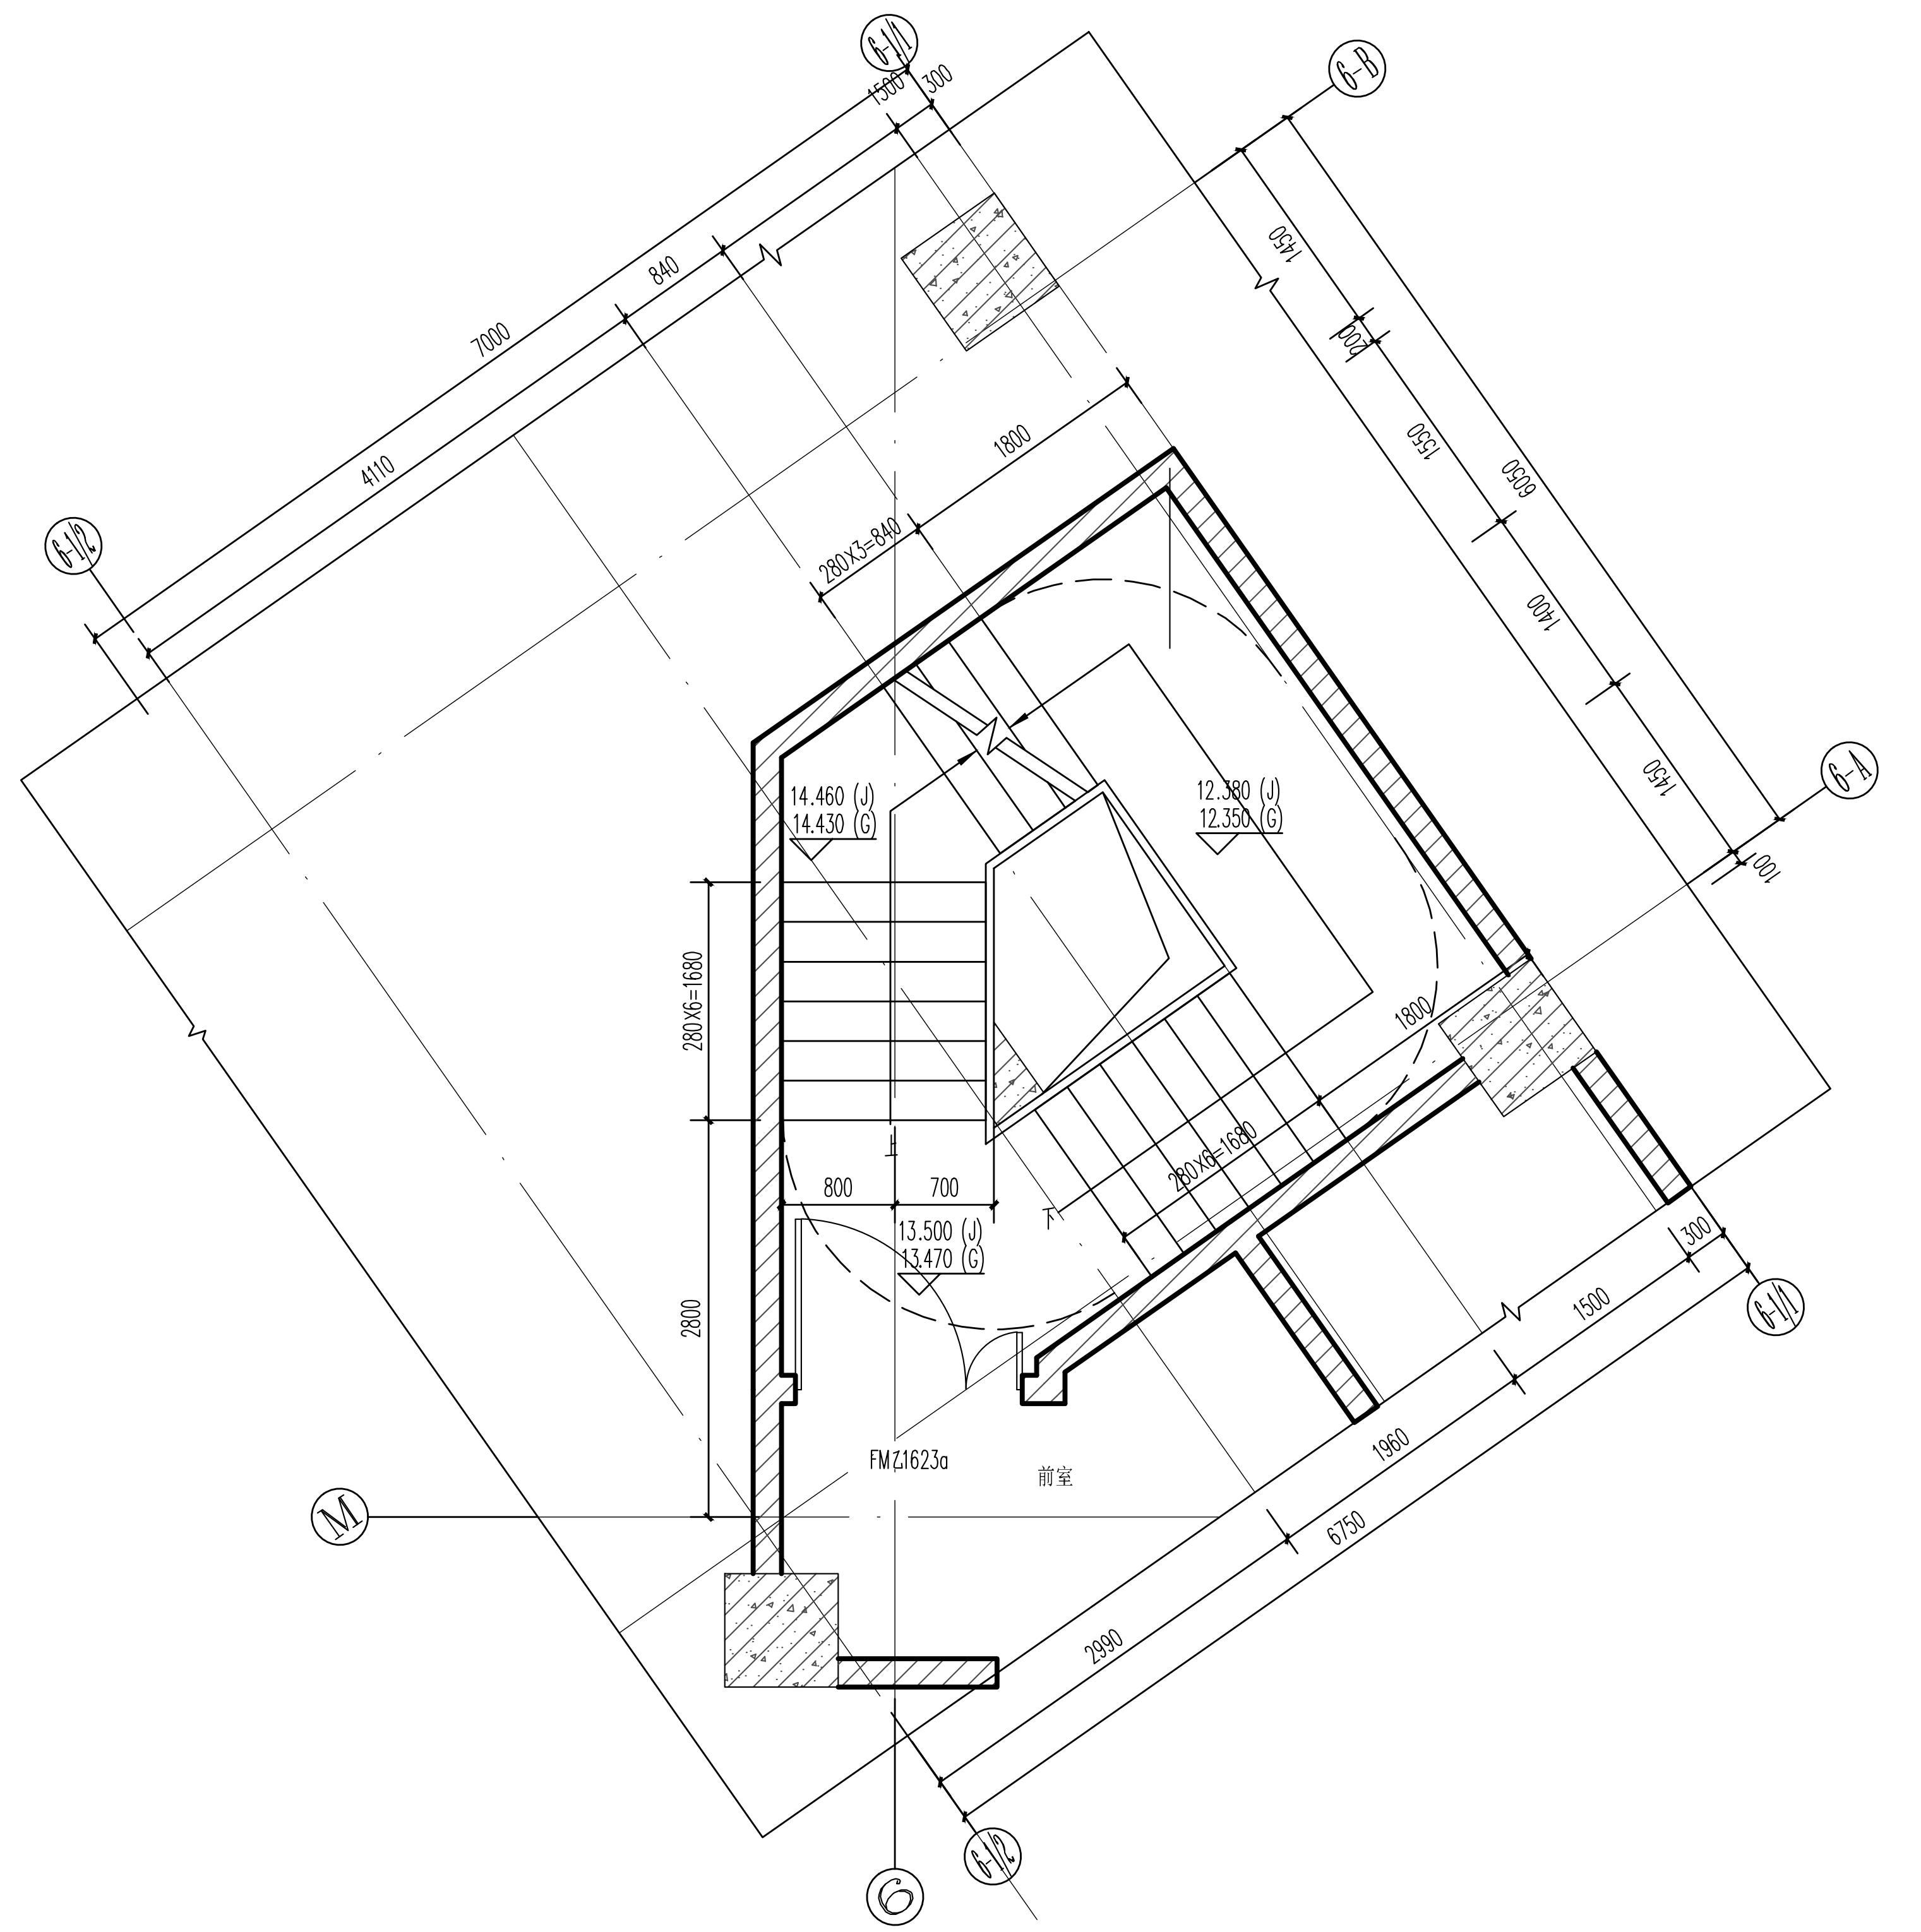

6-1/1
6-B
1500
300
840
7000
4110
6-1/2
1450
200
1550
6050
1400
1450
6-A
100
1800
280X3=840
14.460 (J)
14.430 (G)
12.380 (J)
12.350 (G)
280X6=1680
1800
280X6=1680
800
700
上
下
13.500 (J)
13.470 (G)
2800
300
1500
6-1/1
FMZ1623a
前室
1960
M
6750
2990
6-1/2
6

比例 1:50 LT09 三层平面

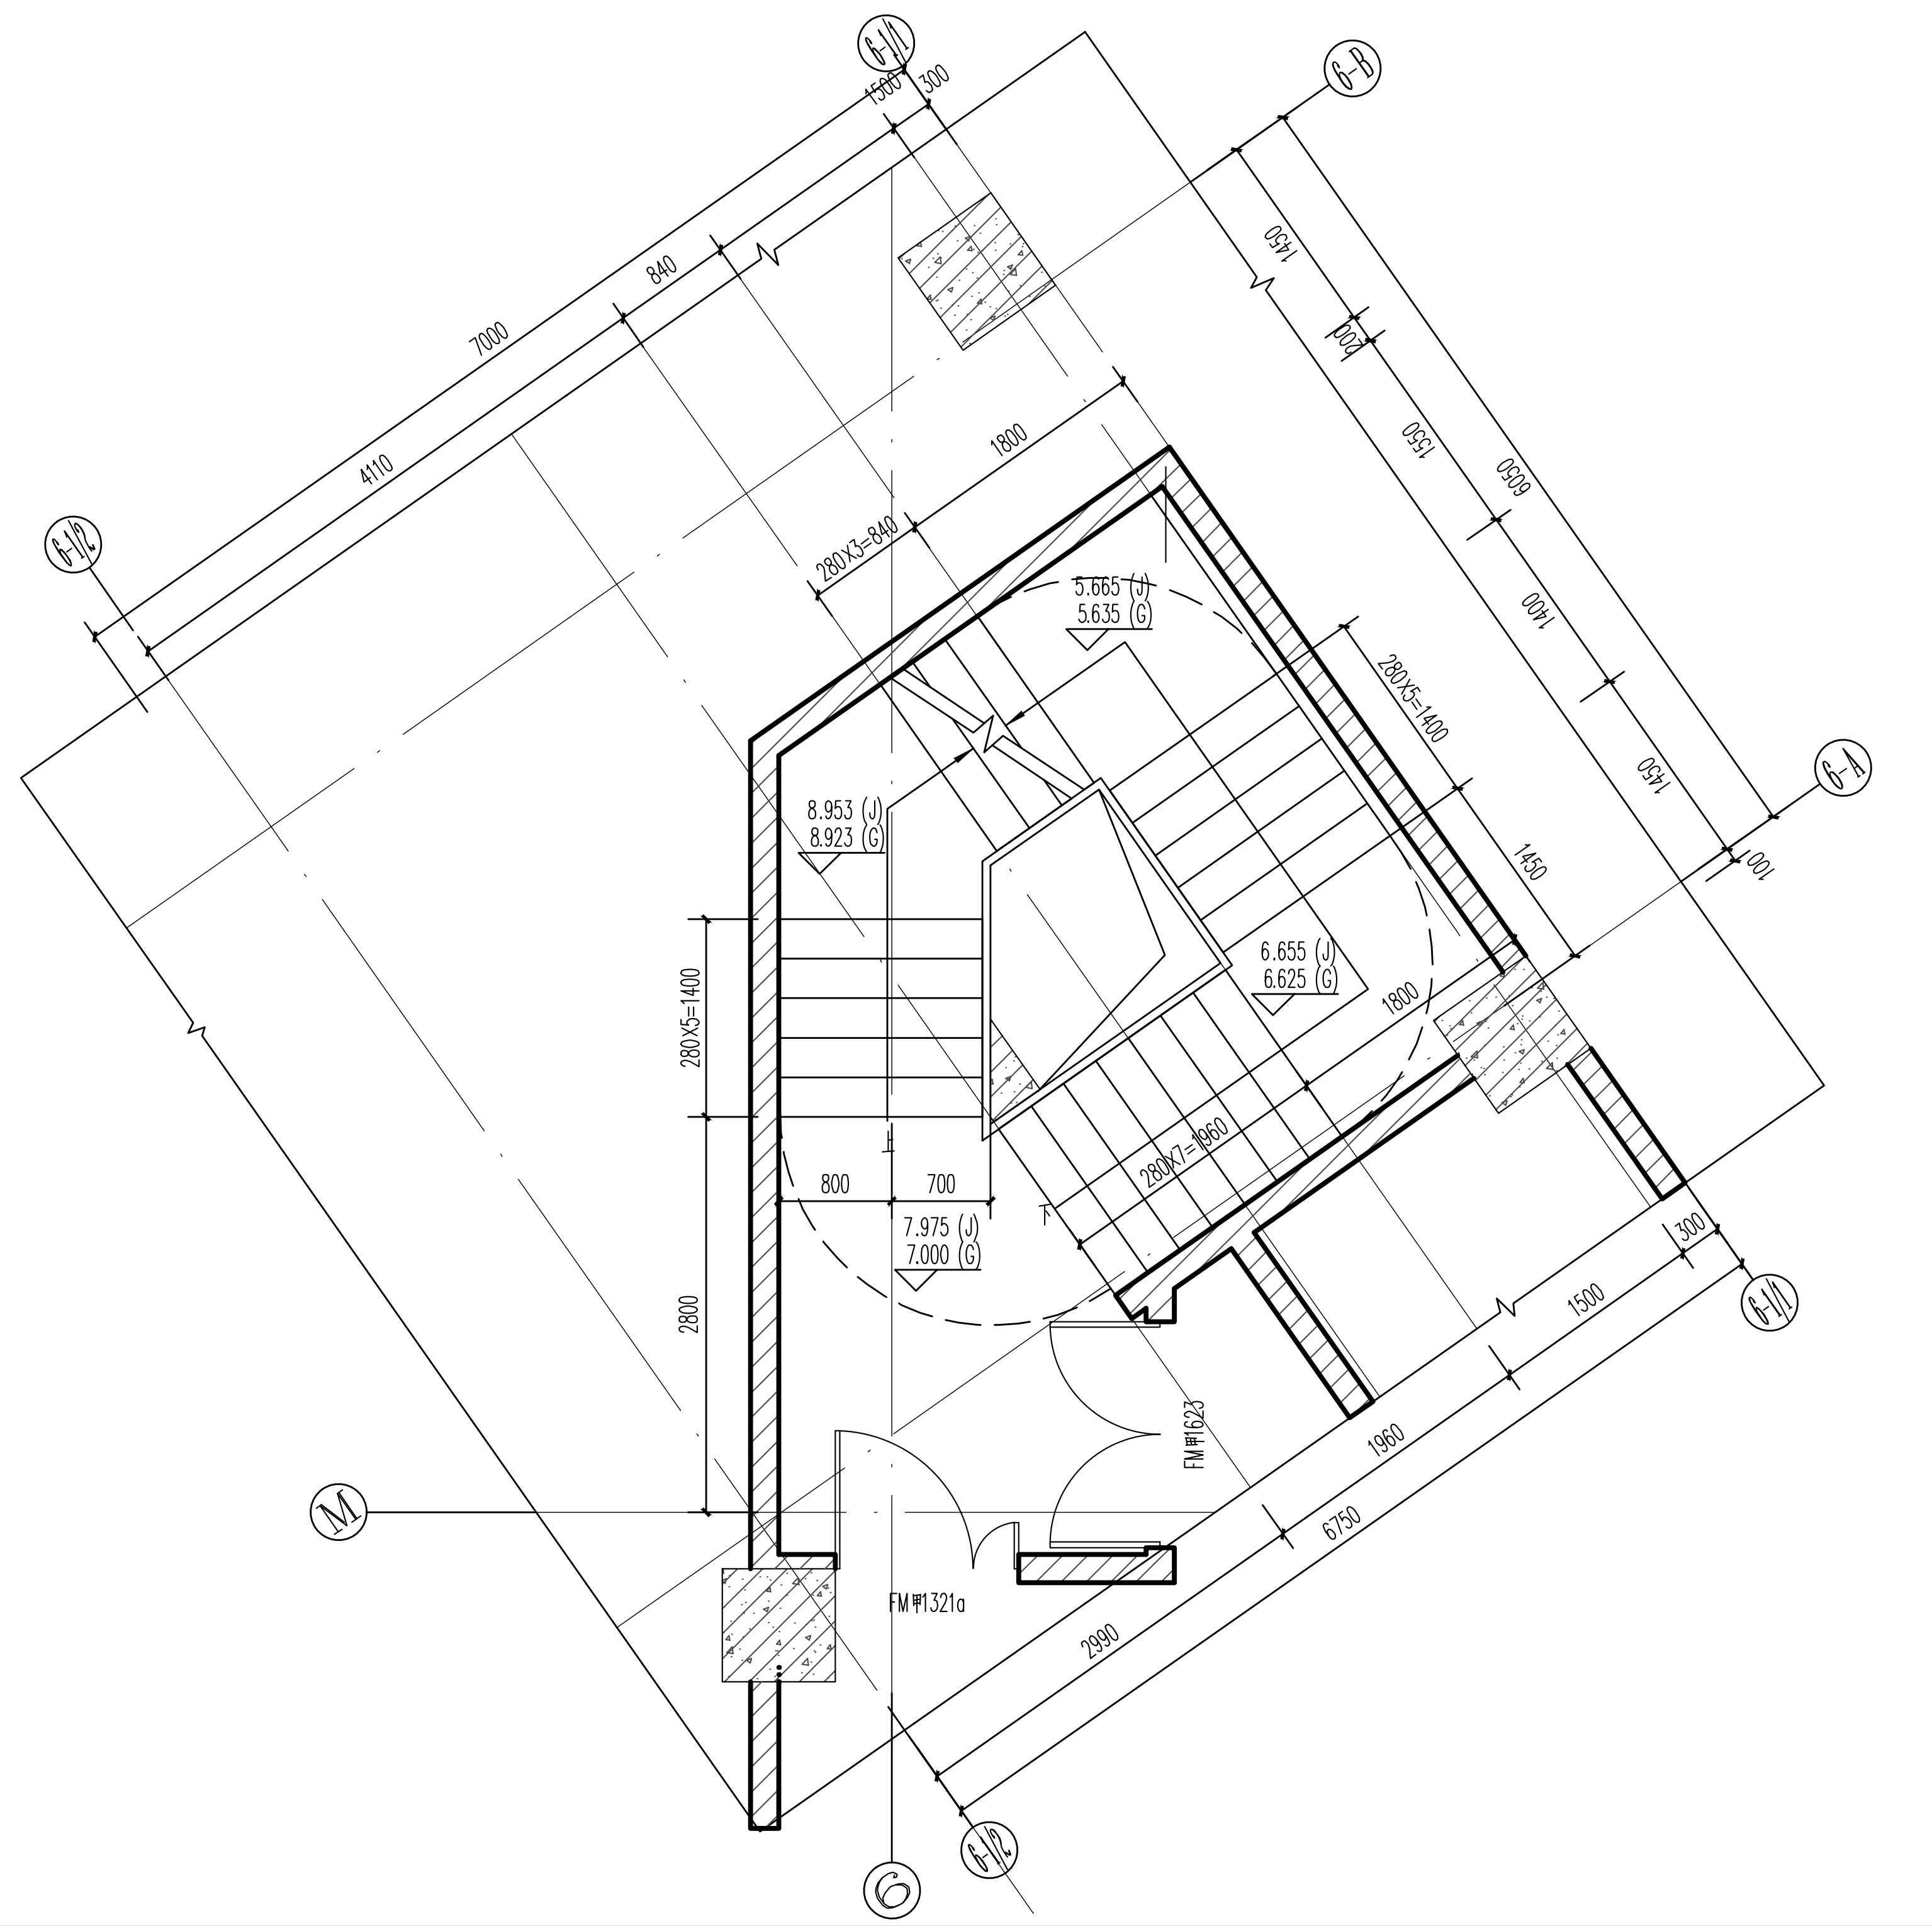

6-1/1
6-B
1500
300
840
7000
4110
6-1/2
1450
200
1550
6050
1400
1450
6-A
100
1800
280X3=840
5.665 (J)
5.635 (G)
280X5=1400
8.953 (J)
8.923 (G)
1450
280X5=1400
6.655 (J)
6.625 (G)
1800
280X7=1960
800
700
7.975 (J)
7.000 (G)
2800
300
1500
6-1/1
FM甲1623
1960
M
6750
FM甲1321a
2990
6-1/2
6

比例 1:50 LT09 二层平面

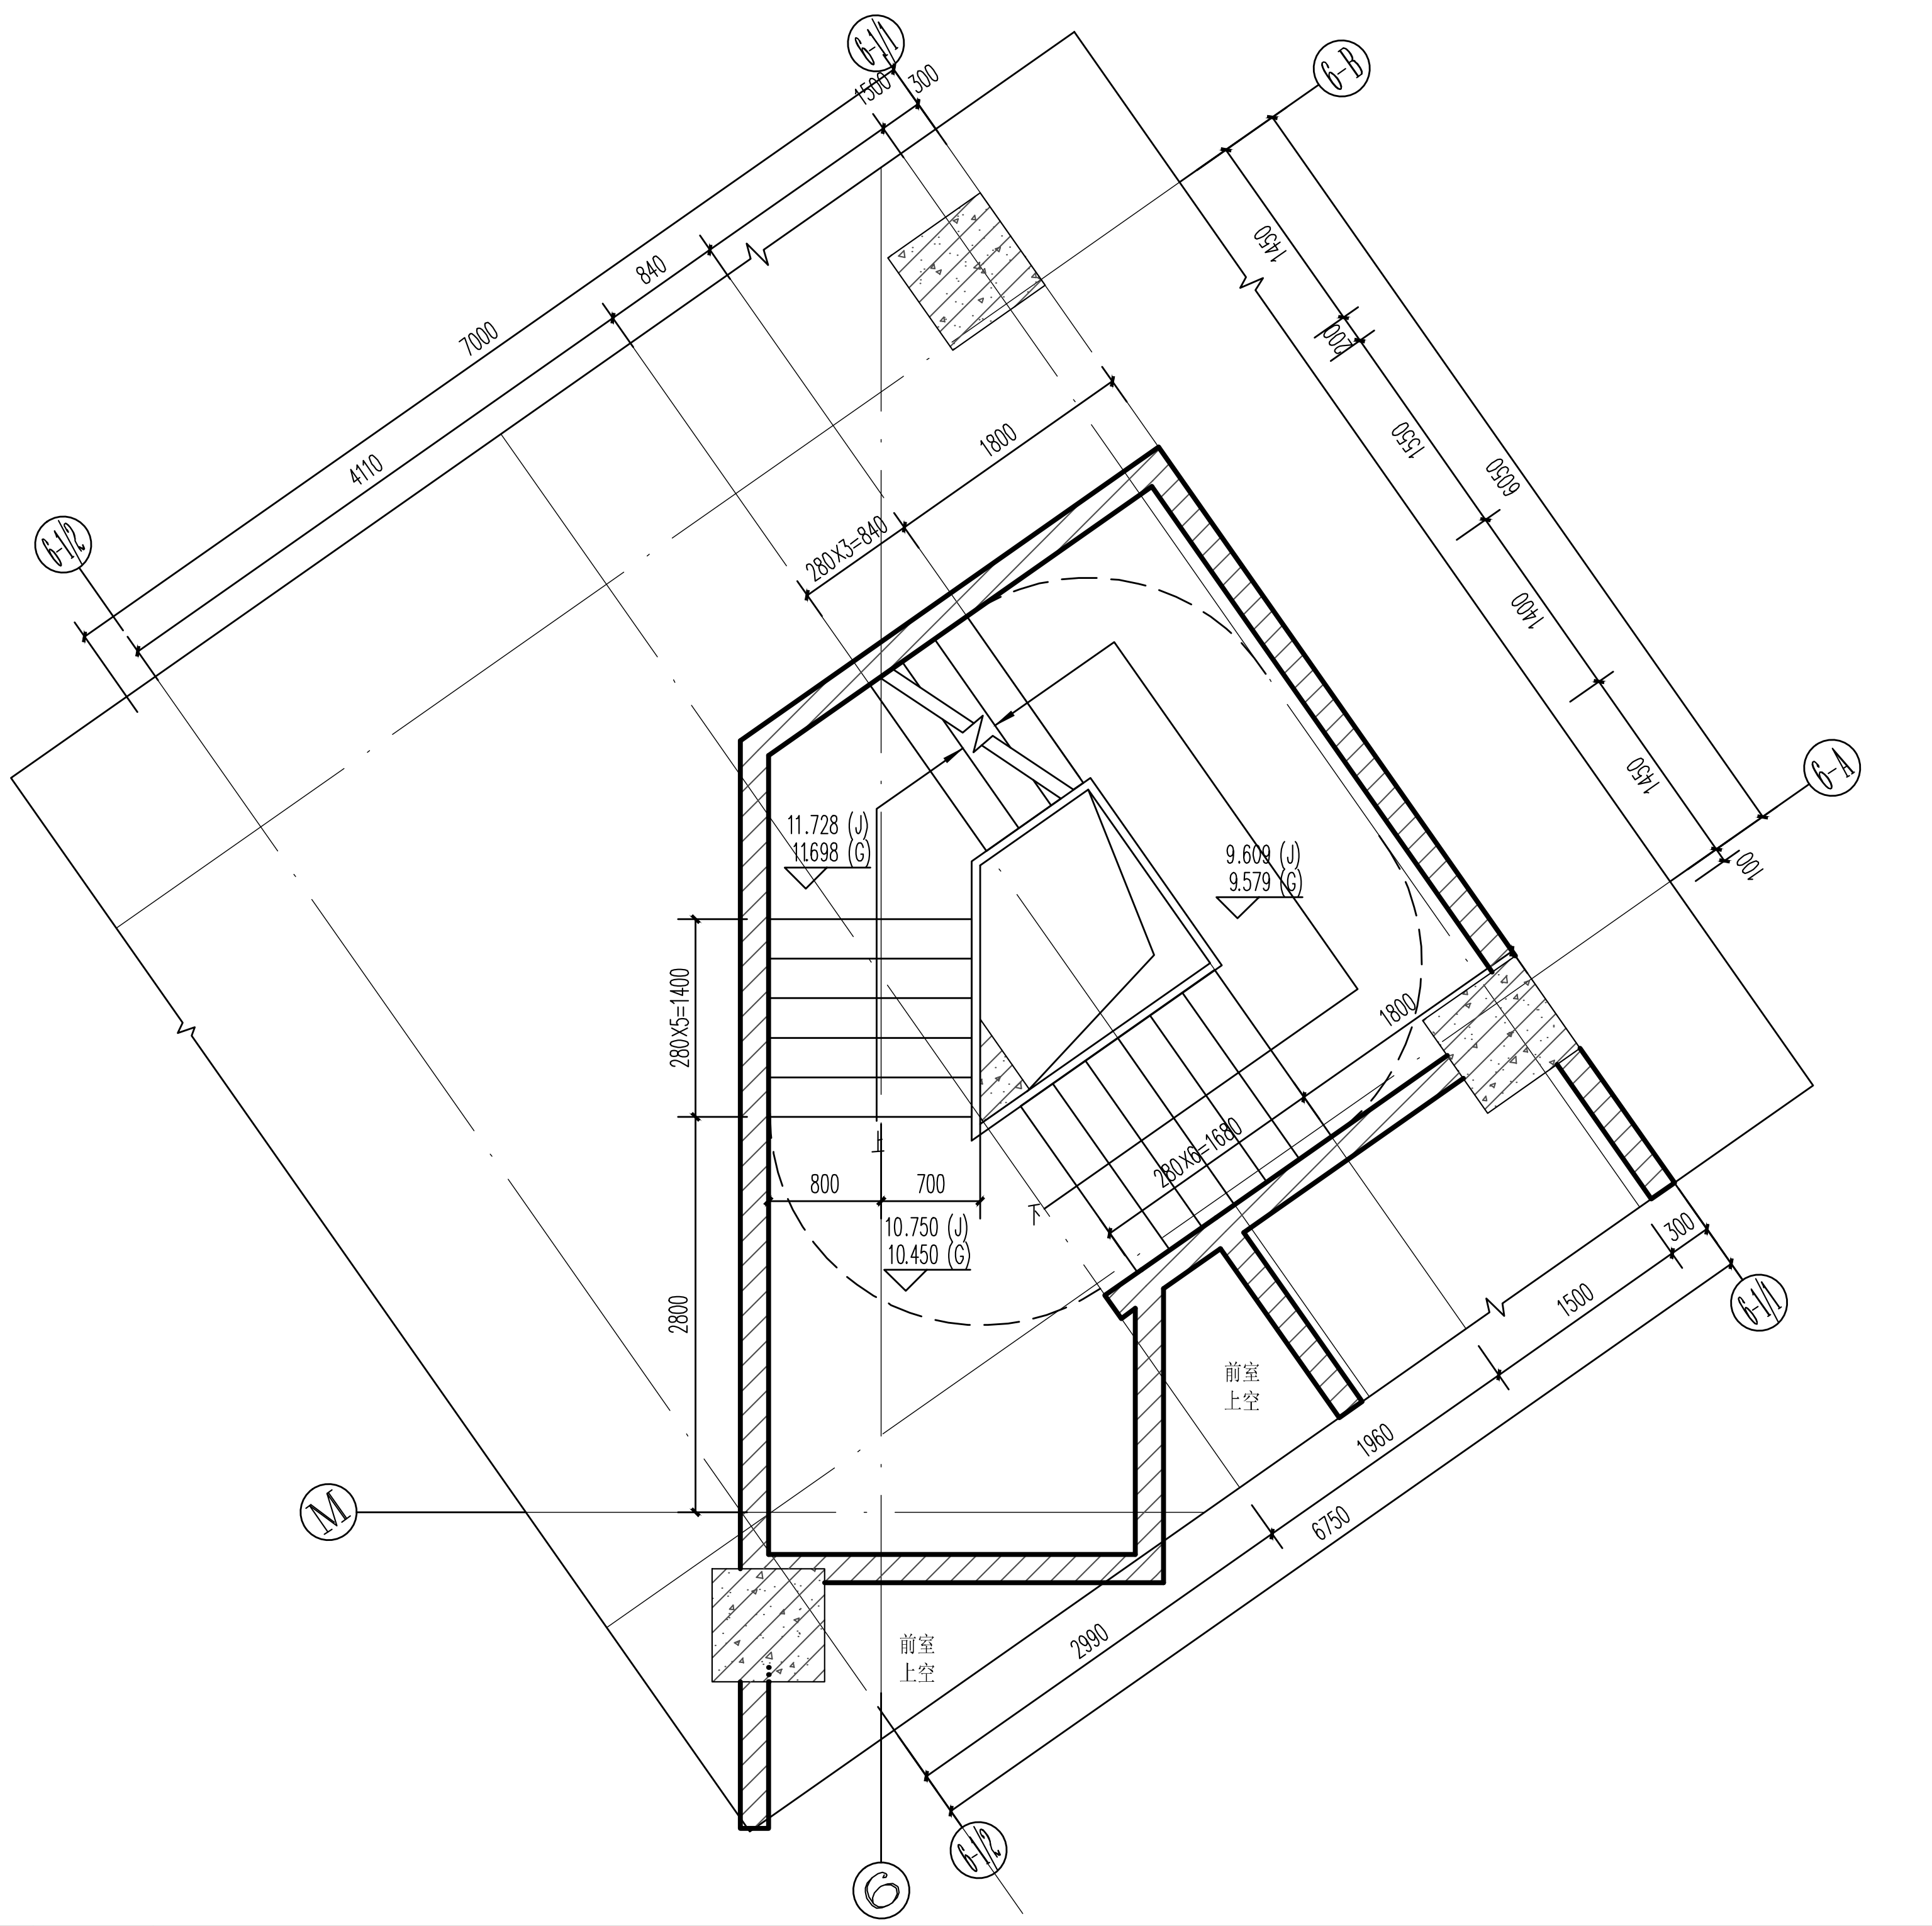

6-1/1
6-B
1500
300
840
7000
4110
6-1/2
1450
200
1550
6050
1400
1450
6-A
100
1800
280X3=840
11.728 (J)
11698 (G)
9.609 (J)
9.579 (G)
280X5=1400
1800
280X6=1680
800
700
10.750 (J)
10.450 (G)
2800
300
1500
6-1/1
前室
上空
1960
M
6750
前室
上空
2990
6-1/2
6

比例 1:50 LT09 10.750标高平面

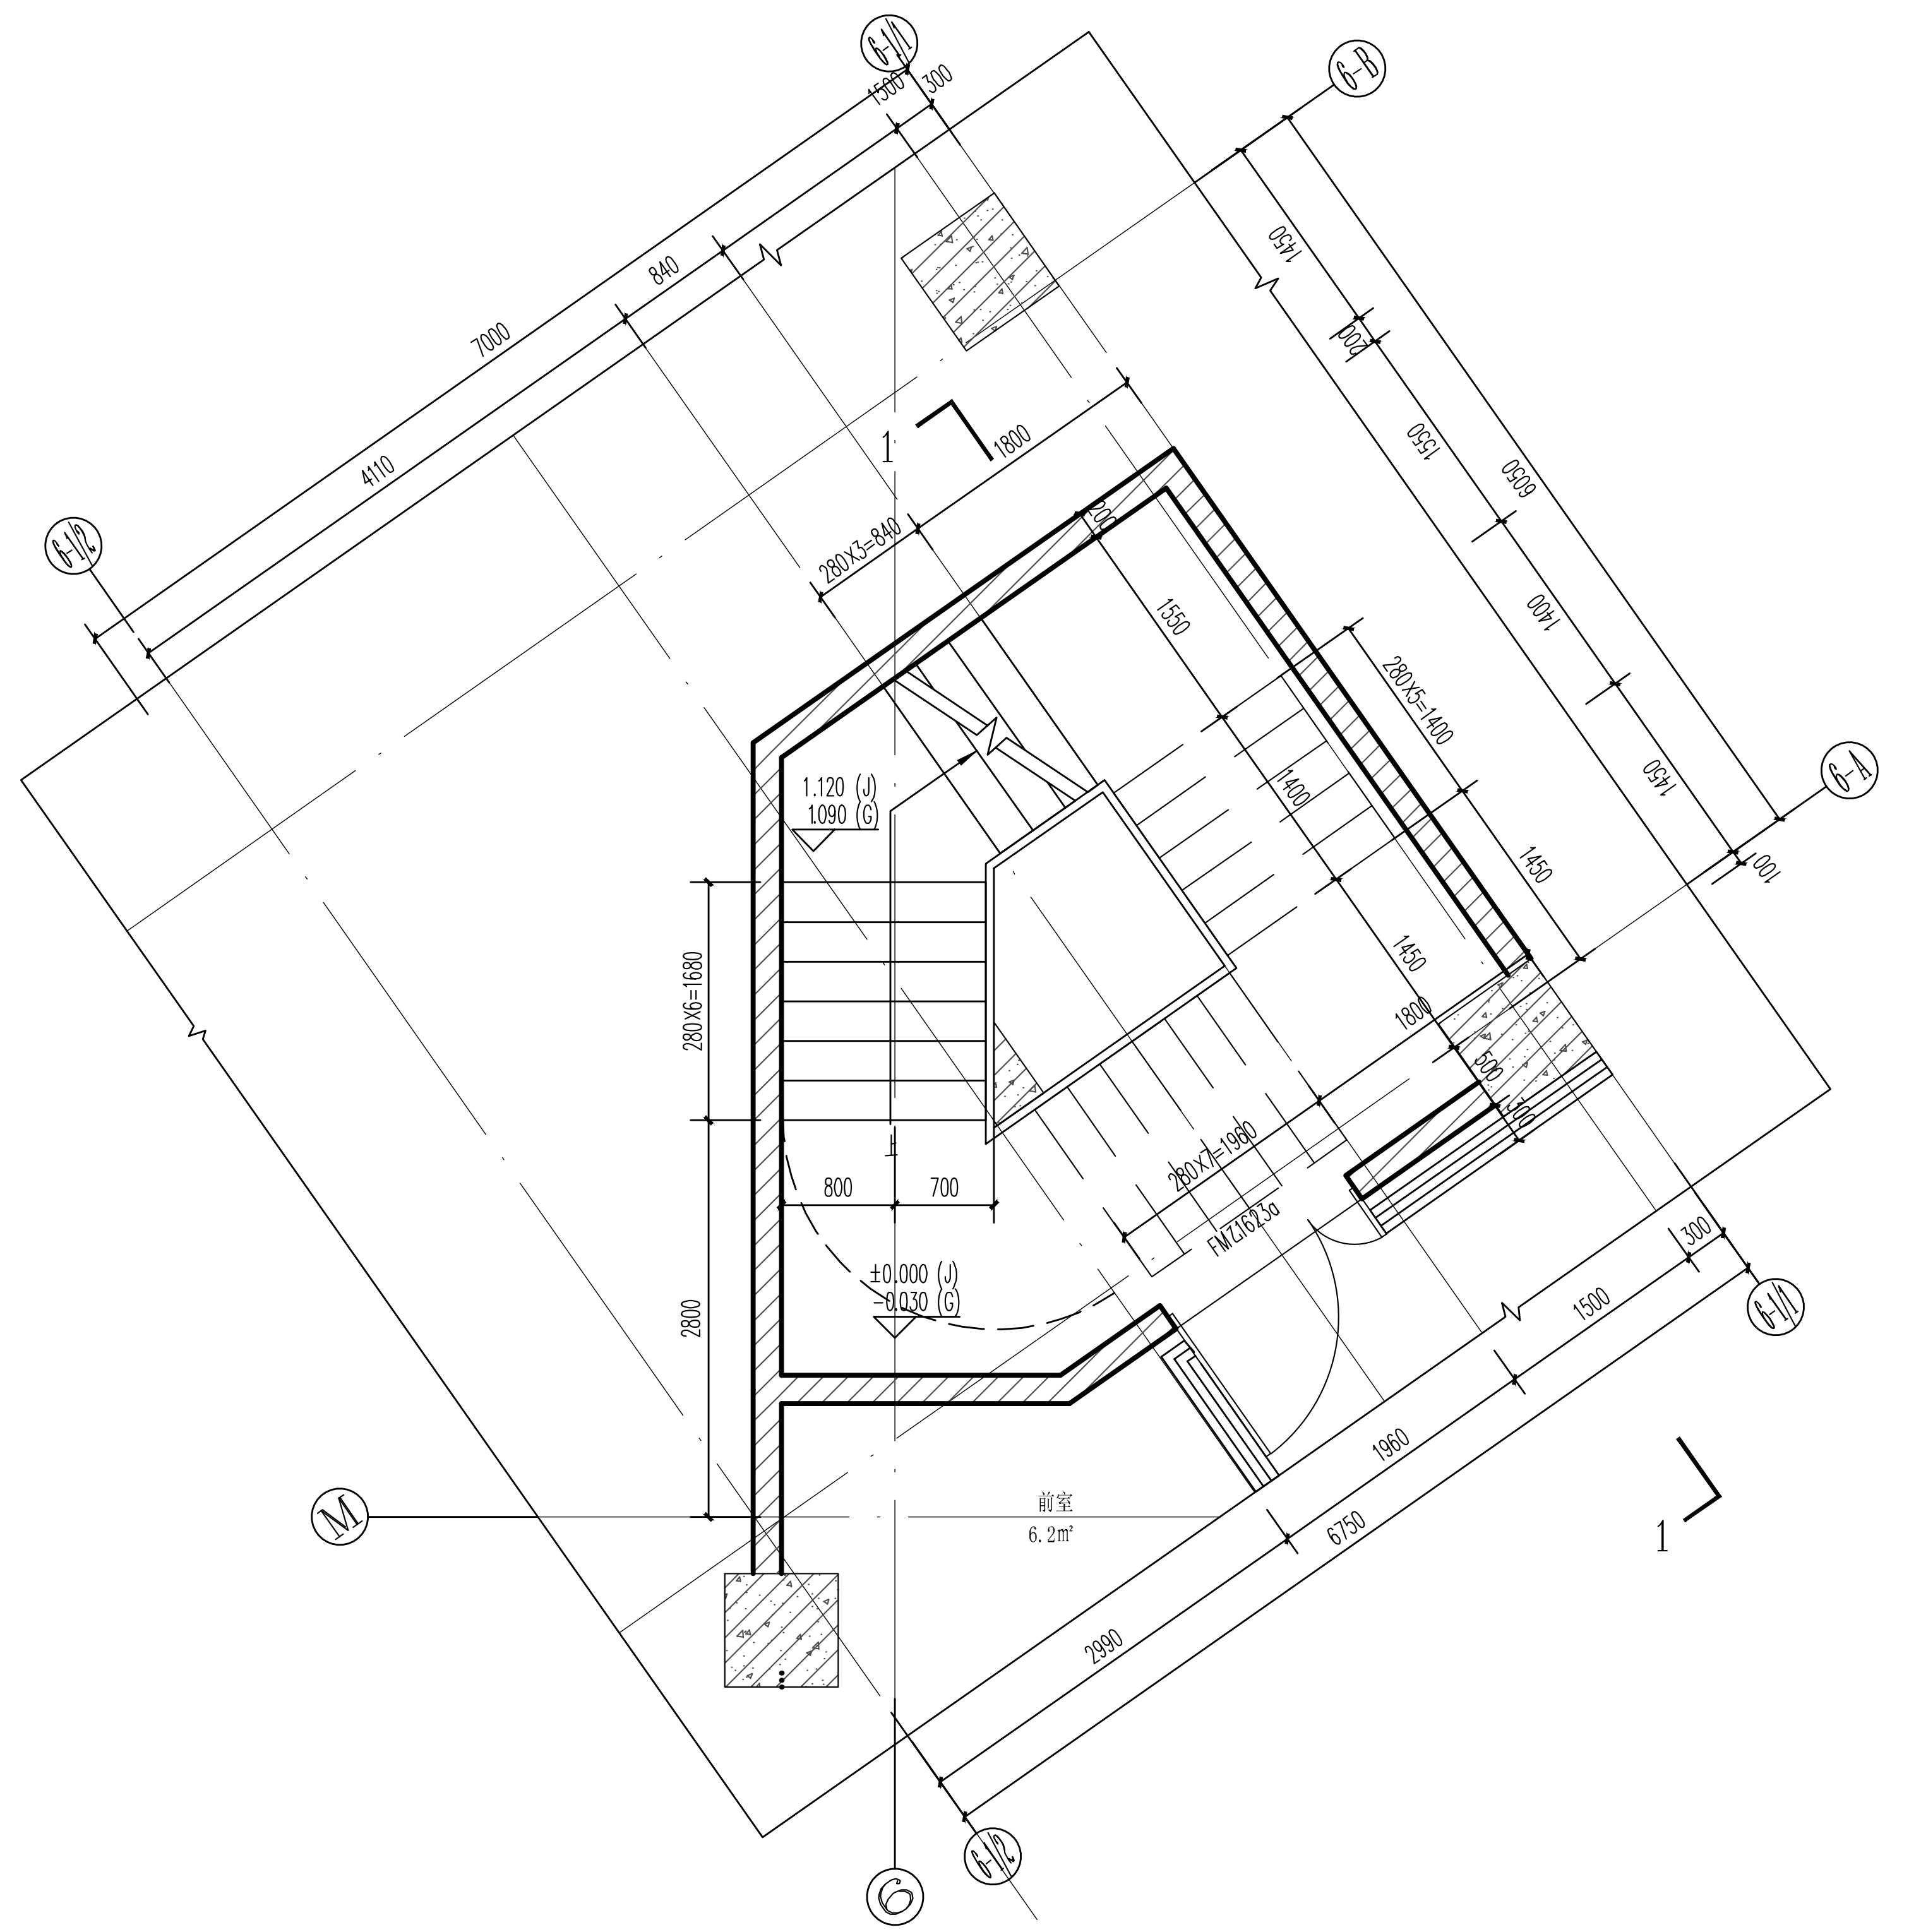

6-1/1
6-B
1500
300
840
7000
4110
6-1/2
1450
200
1
1800
280X3=840
200
1550
6050
280X5=1400
1400
1400
1450
6-A
100
1450
1.120 (J)
1.090 (G)
280X6=1680
1450
1800
500
300
280X7=1960
FMZ1623a
800
700
±0.000 (J)
-0.030 (G)
2800
300
1500
6-1/1
1960
1
前室
6.2m²
M
6750
2990
6-1/2
6

比例 1:50 LT09 首层平面

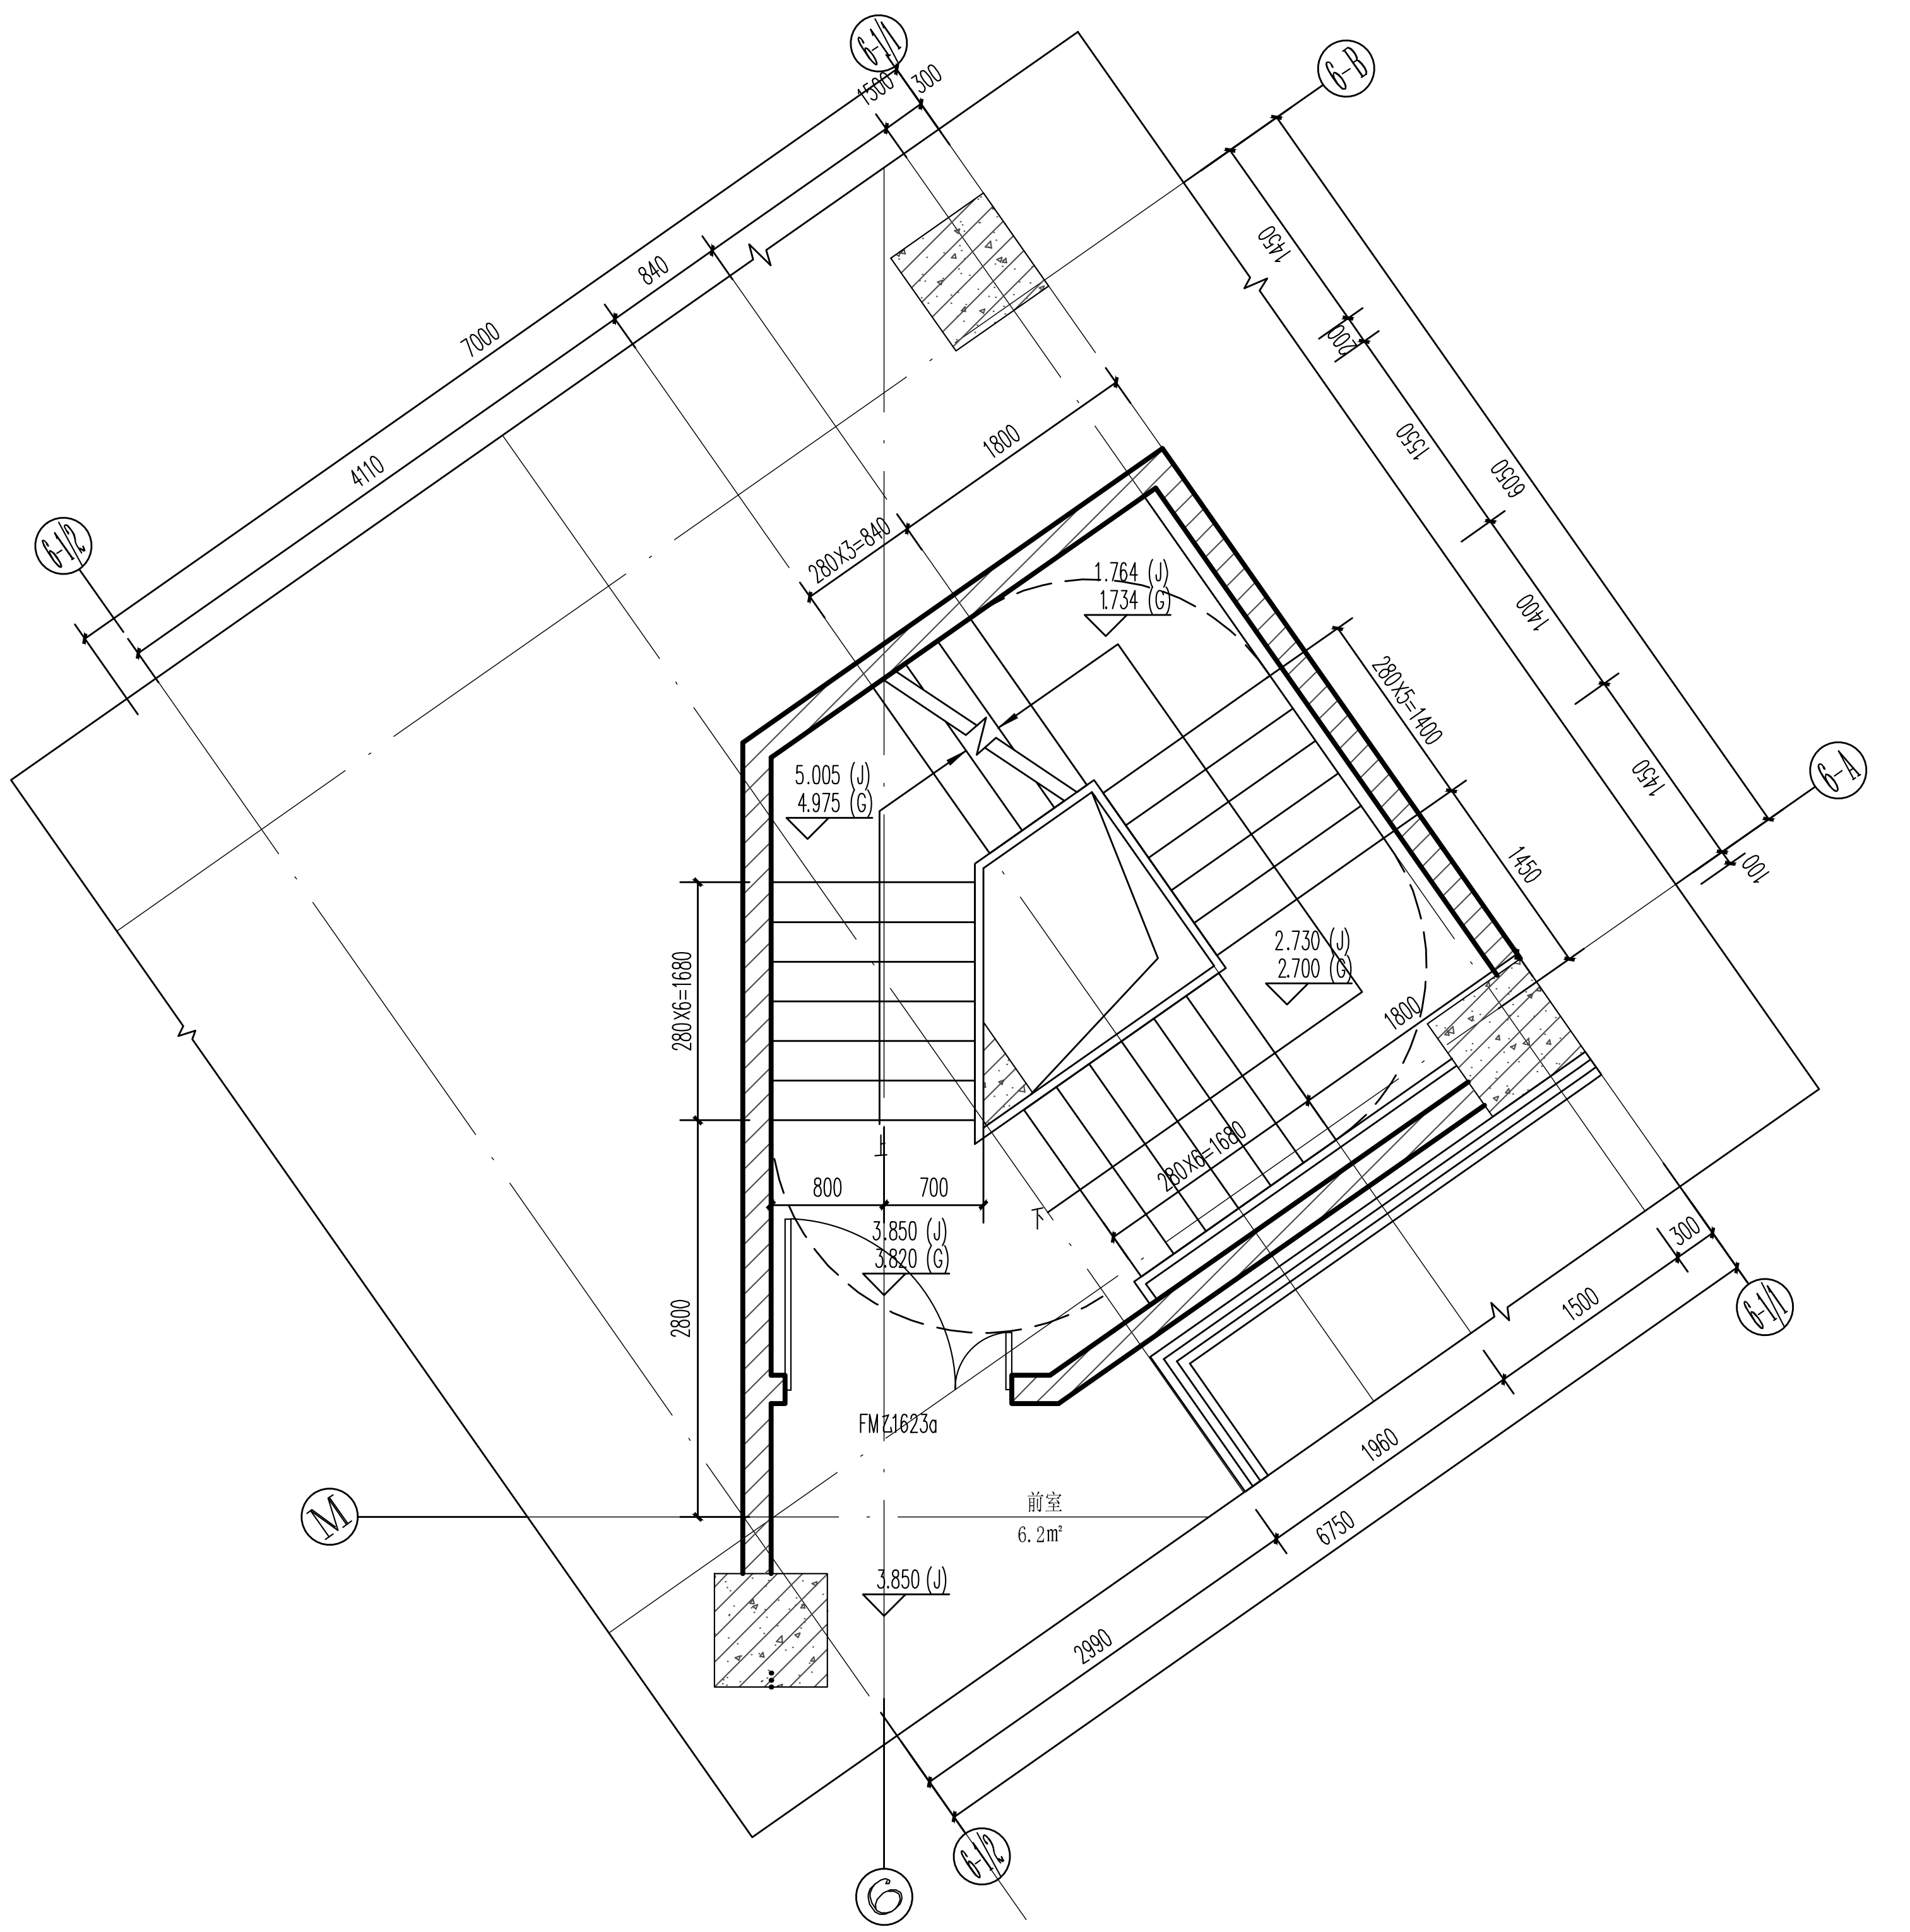

6-1/1
6-B
1500
300
840
7000
4110
6-1/2
1450
200
1550
6050
1400
1450
6-A
100
1800
280X3=840
1.764 (J)
1.734 (G)
280X5=1400
5.005 (J)
4.975 (G)
1450
2.730 (J)
2.700 (G)
280X6=1680
1800
280X6=1680
800
700
3.850 (J)
3.820 (G)
2800
300
1500
6-1/1
FMZ1623a
1960
前室
6.2m²
M
6750
3.850 (J)
2990
6-1/2
6

比例 1:50 LT09 首层夹层平面

图纸名称	LT09 楼梯大样图（一）
图号	J-1-LT12
版本号	
出图日期	2023.08.02
序号	
设计阶段	施工图
业务号	21-347
专业	建筑
工程名称	保利天珺秀台7#
建设单位	佛山市禅城区保宸置业有限公司
设计	胡伟航
校核	石昊洋
专业负责人	宋延勇
设计总负责人	张林汉 黄孝颖
审核	张林汉
审定	黄孝颖
院总工程师	赵松林

版权所有，不得复制、套用或公开。
ALL RIGHTS RESERVED.

图纸条码

版本号	日期	修改内容	修订者

修订栏

平面位置示意 Key Plan

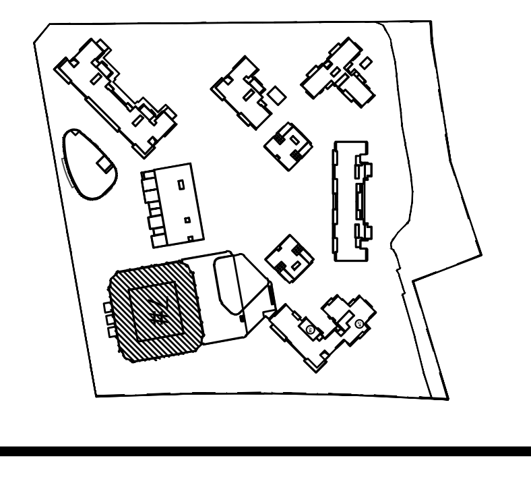

广州市设计院集团有限公司
GUANGZHOU DESIGN INSTITUTE GROUP CO.,LTD.
工程设计甲级资质证书编号：A244007378
工程勘察甲级资质证书编号：B244007378