

会签栏								
	建　筑	宋延勇			暖　通	陈少玲		
	结　构	邓艳青						
	给排水	甘兆麟						
	电　气	蔡泽炯						

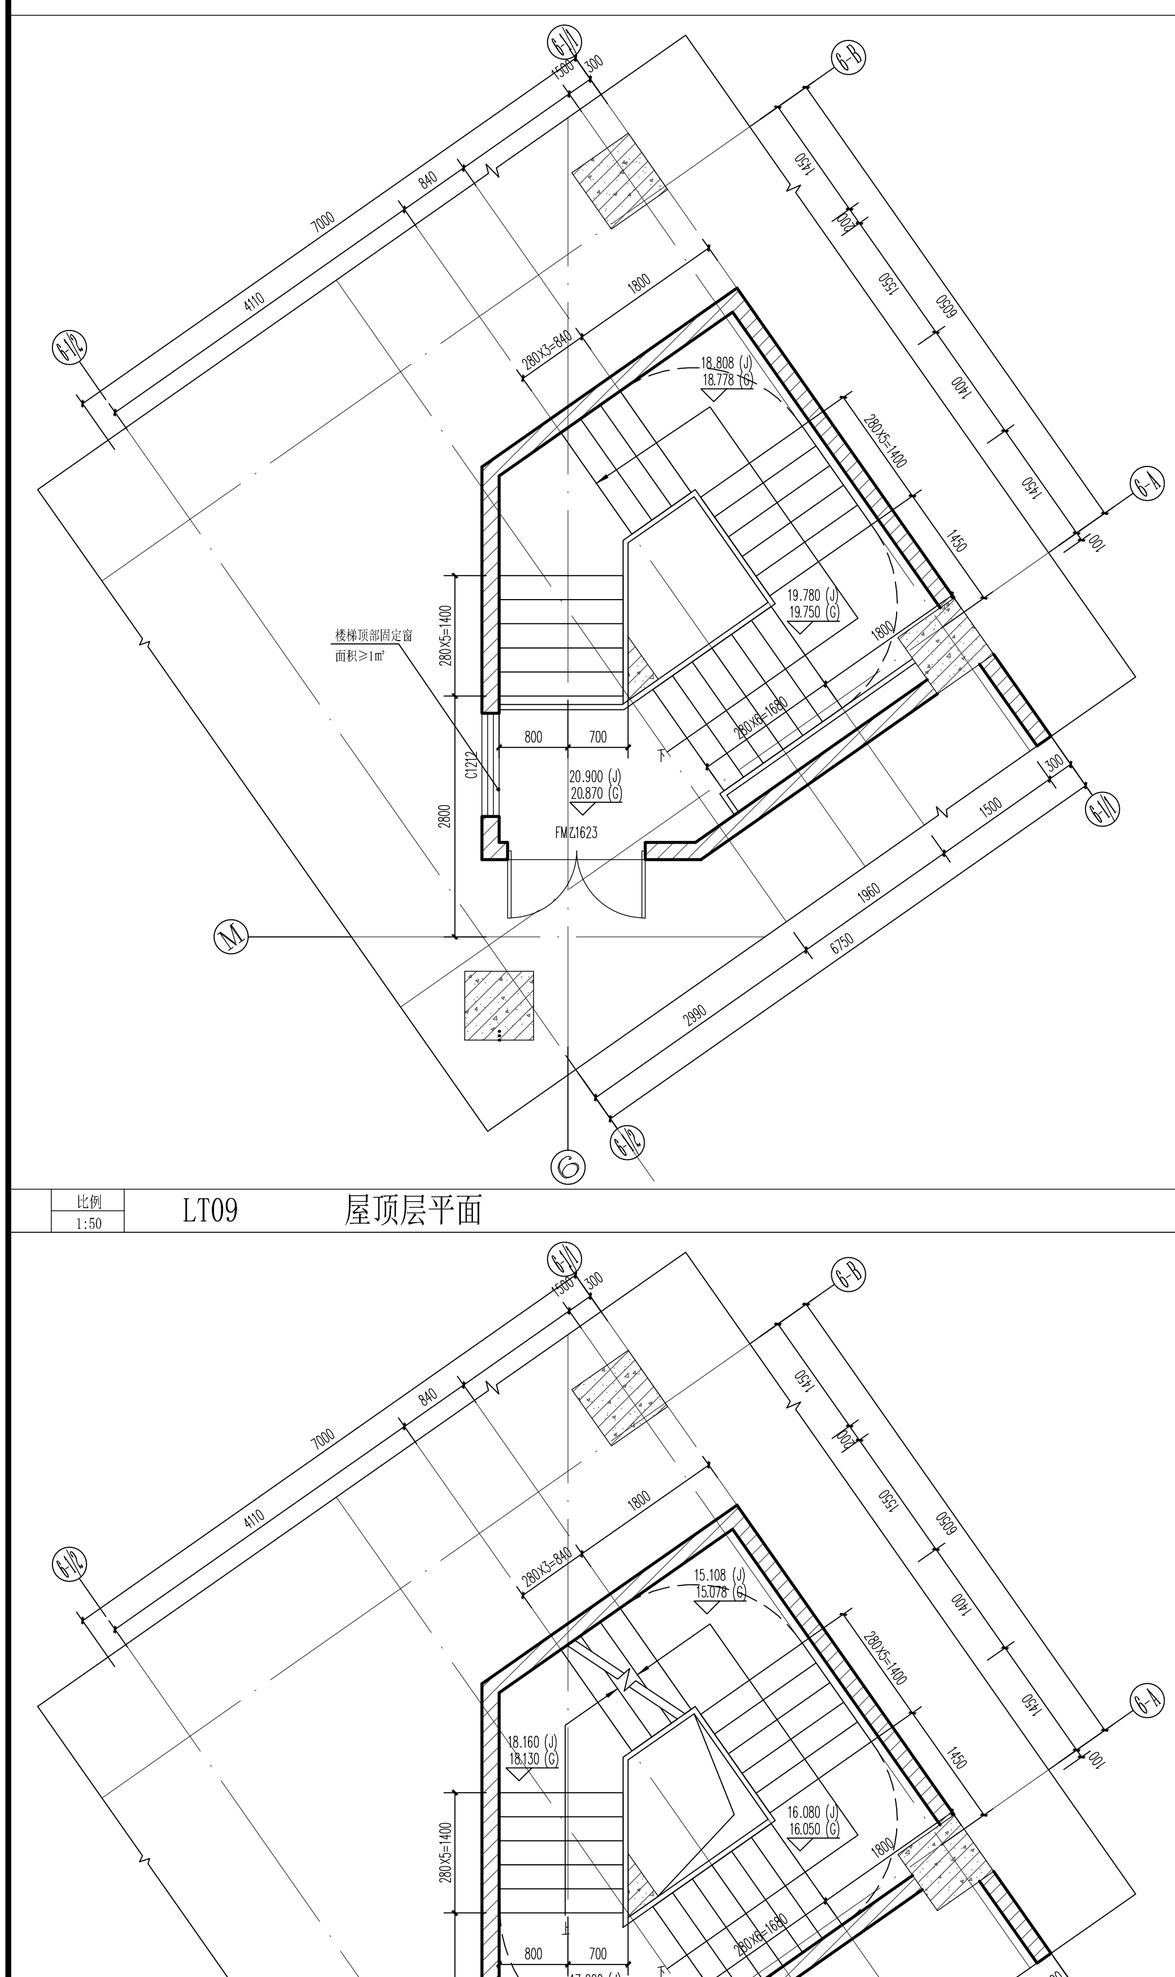

比例 1:50　LT09　屋顶层平面

比例 1:50　LT09　17.050标高平面

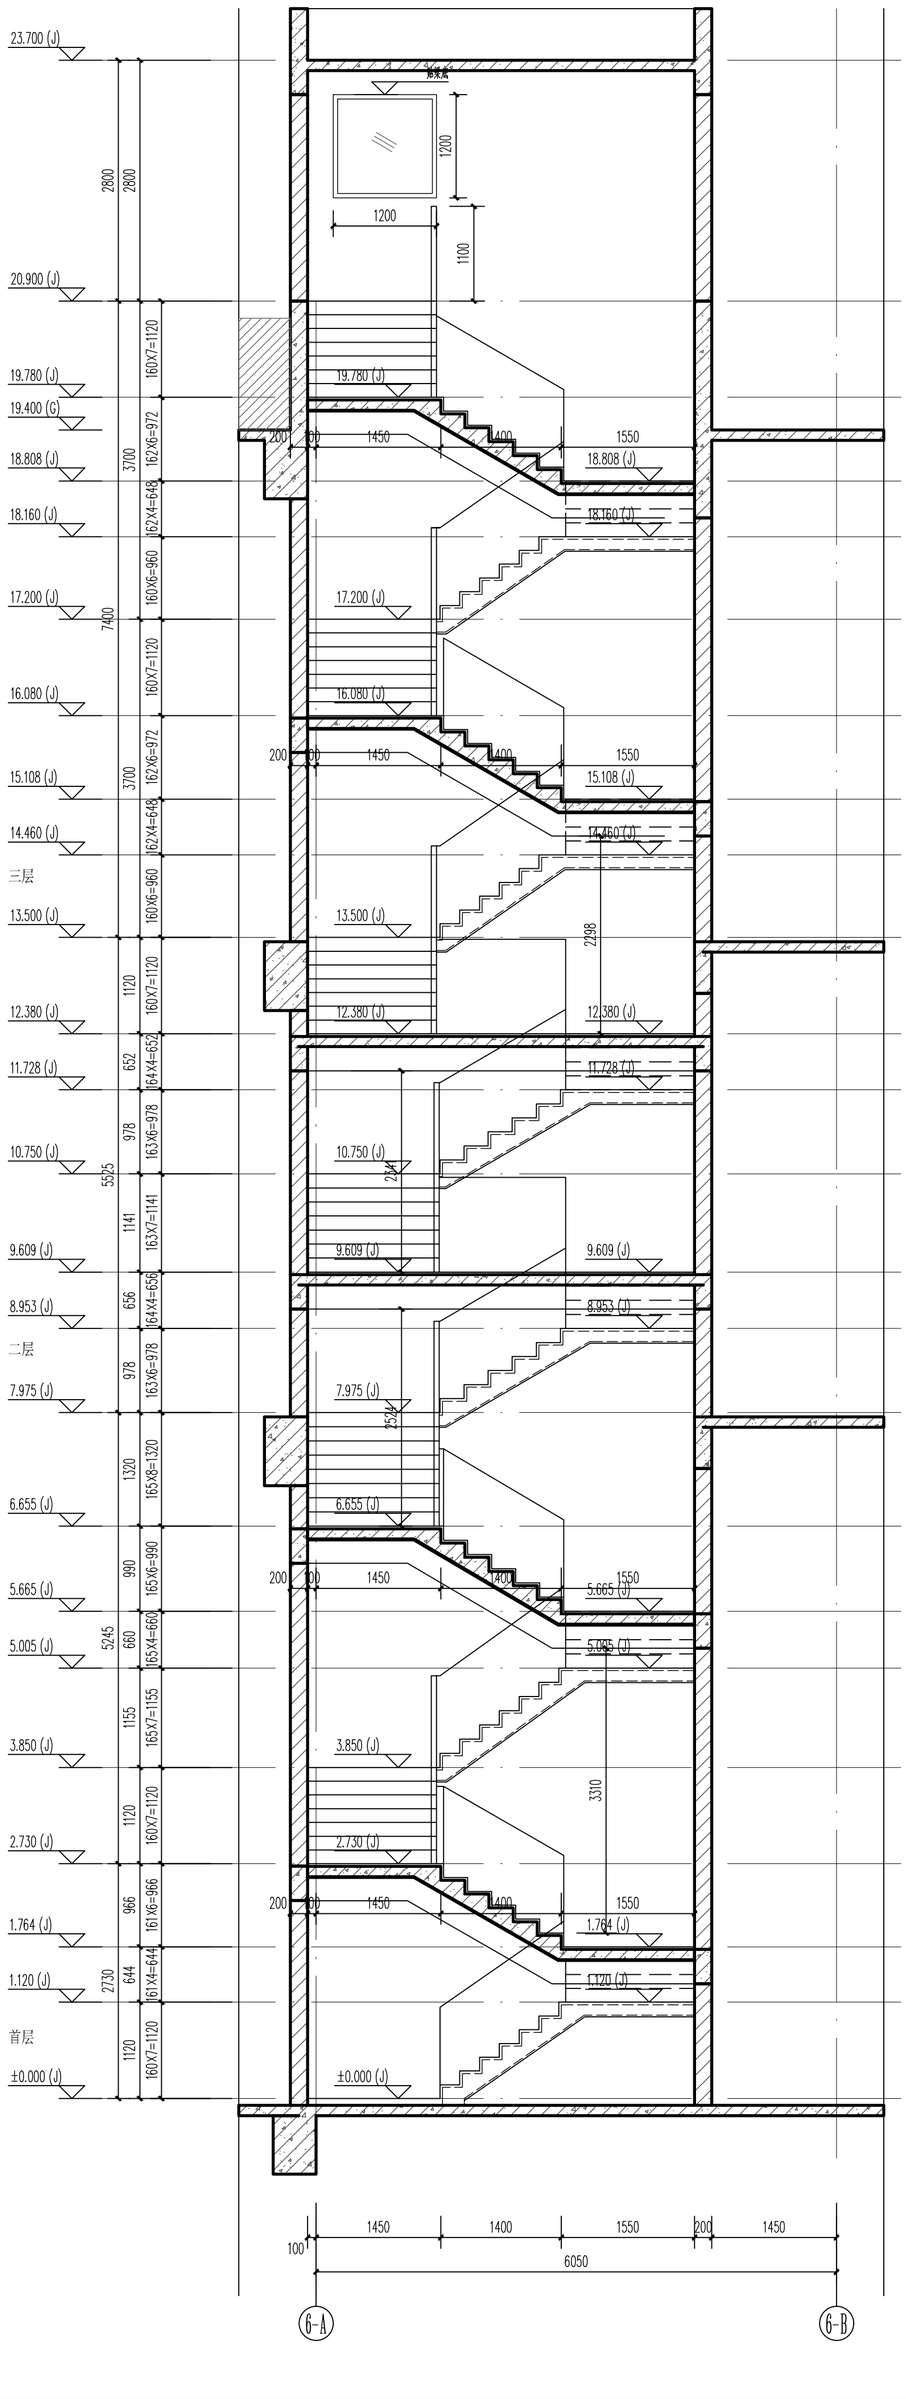

比例 1:50　LT09　1-1剖面

版本号	日期	修改内容栏	修订者

图纸条码

院总工程师	赵松林	
审　定	黄孝颖	
审　核	张林汉	
设　计 总负责人	黄孝颖 张林汉	
专业负责人	宋延勇	
校　核	石昊洋	
设　计	胡伟航	

建设单位：佛山市禅城区保宸置业有限公司

工程名称：保利天珺秀台7#

业务号：21-347　专业：建筑

设计阶段：施工图


图纸名称：LT09 楼梯大样图（二）

图号：J-1-LT13　版本号：

出图日期：2023.08.02　序号：

版权所有，不得复制、套用或公开。
ALL RIGHTS RESERVED.

平面位置示意 Key Plan

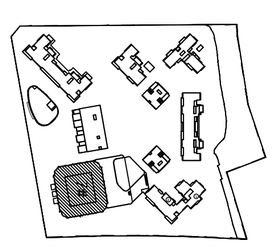

广州市设计院集团有限公司
GUANGZHOU DESIGN INSTITUTE GROUP CO.,LTD.
工程设计甲级资质证书编号：A244007378
工程勘察甲级资质证书编号：B244007378