	陈少玲
暖通	
智能化	
建筑	宋延勇
结构	邓艳青
给排水	甘兆麟
电气	蔡泽炯

会签栏

说明：

1、除特别注明外，图中所示标高为建筑面标高。结构标高和建筑面标高同时标注时，标高后加（J）表示为建筑完成面标高，标高后加（G）表示为结构面标高。

2、除特别注明外，墙厚为200mm。

3、除特别注明外，门垛均为100mm，或门位于所在房间(或走廊)的正中。

4、除特别注明外，以下的功能区域的标高对应相应的停车库楼面建筑标高“H”。

5、水管、地漏、雨水口、排水留孔的大小及具体位置以给排水专业图纸位置，本图仅为示意。

6、建筑内的电缆井、管道井应在每层楼板处采用不低于楼板耐火极限的不燃材料或防火封堵材料封堵；

7、本图中所有墙体预留孔洞均需在管道安装完后以膨胀性防火填料封堵。

8、消防救援窗采用易敲碎玻璃；幕墙与楼板之间的间缝，需用相当于楼板耐火极限的不燃烧材料严密填实，具体详幕墙图纸。

9、图示 ⛰ 为消火栓，其尺寸为700×1800×240（宽×高×深），离地100安装。

10、地下层所有集水井上面盖铁格栅，上行车道深沟处为承压铁格栅。地下车库内除注明外，浅沟均不设格栅。室外所有集水井和水沟上面盖不锈钢格栅或穿孔石板。

11、地下层高低压配电房的地面在完成电缆沟施工后，在结构面上二次浇C15混凝土，具体构造另详专业图。

12、水泵房地面在结构面上二次浇C15混凝土并找坡，排水另详水专业图，设备基础部分 构造另详专业图。

13、地下层各设备房内的通风百页，另详暖通专业图。楼梯和前室的加压洞口与百叶除特别注明外，均距地300高安装。

14、所有汽车坡道两侧非混凝土结构的墙体需在坡道面上1000以下的高度浇注C20混 凝土同墙厚，内配Φ12@200双面。

15、强、弱电间在门内侧设C15混凝土门槛100mm宽X200mm高。电井、水井的预留管井 应在每层楼板处用相当于楼板耐火极限的不燃材料封堵。消防水泵房应采取防水淹的技术措施，设置100mm宽X200mm高混凝土门槛以防水淹。

16、消防电梯设置符合《消防电梯制造和安装安全规范》GB26465-2011相关规定。

17、设备房砌体在设备安装后再砌筑；外墙饰面砖铺贴采用专用粘结剂和柔性勾缝剂，禁止使用水泥砂浆铺贴。

18、人防墙体、人防门洞、人防口部、人防套管、人防集水井等具体设计应另详人防专业图纸。

19、防火墙耐火极限为3.00h，特级防火卷帘耐火时间为3.00h。

20、300mm宽排水浅沟，排水浅沟起点处深20mm，终点处深50mm。

21、发电机房内的储油间其总储存量不应大于1m3，储油间门内侧设C15混凝土门槛100mm宽X200mm高混凝土门槛以防油品流散。工具间不得储藏气、液体燃料。不应设置修理车位，喷漆间、充电间、乙炔间和甲乙类物品库房。

22、厨房一般区域预留荷载450kg/㎡，冷库及仓库区域是750kg/㎡。

23、变压器采用干式变压器，详见D0-1-01电气设计施工图总说明（上）。

24、本项目设置自动喷水灭火系统和自动报警系统。

25、电梯层门的耐火极限不应低于1.00h。

消防分区示意图

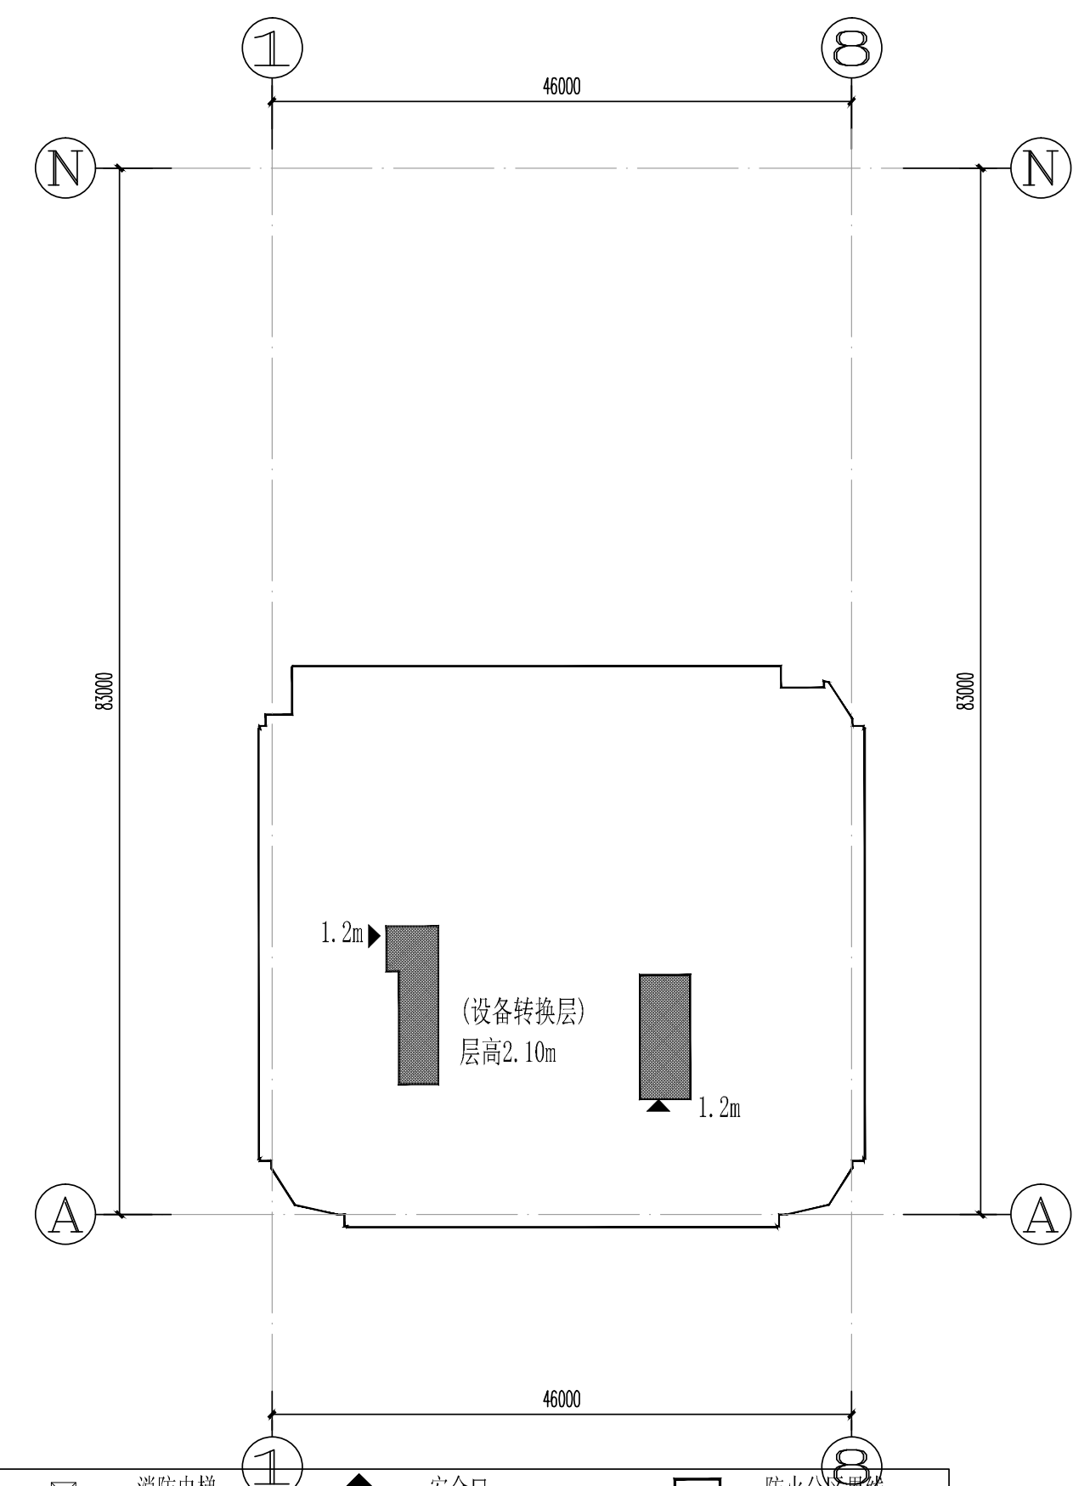

①
⑧
46000
N
A
83000
1.2m
(设备转换层)
层高2.10m
1.2m

图例：	☒ 消防电梯	▲ 安全口	☐ 防火分区界线
	▨ 楼梯间	△ 安全口(借口)	----- 疏散距离

消防宽度计算

佛山保利天珺7#楼层高表(B3F~4F)

	楼层	层高(mm)	建筑标高（J）H	结构标高(G)		楼层	层高(mm)	建筑标高（J）H	结构标高(G)
塔楼	4F（公寓大堂）	3600	21.150	21.100	裙房	1F（公寓、宴会大堂）	8000	0.000	-0.080
裙房	3F设备转换层	2150	19.000	18.950	地下室	B1F（酒店后勤）	6650	-6.650	-6.750
	3F	5500	13.500	13.450		B2F（局部人防区）	3500	-10.150	-10.250
	2F（酒店大堂）	5500	8.000	7.920		B3F(整体人防区)	3700	-13.850	-14.000

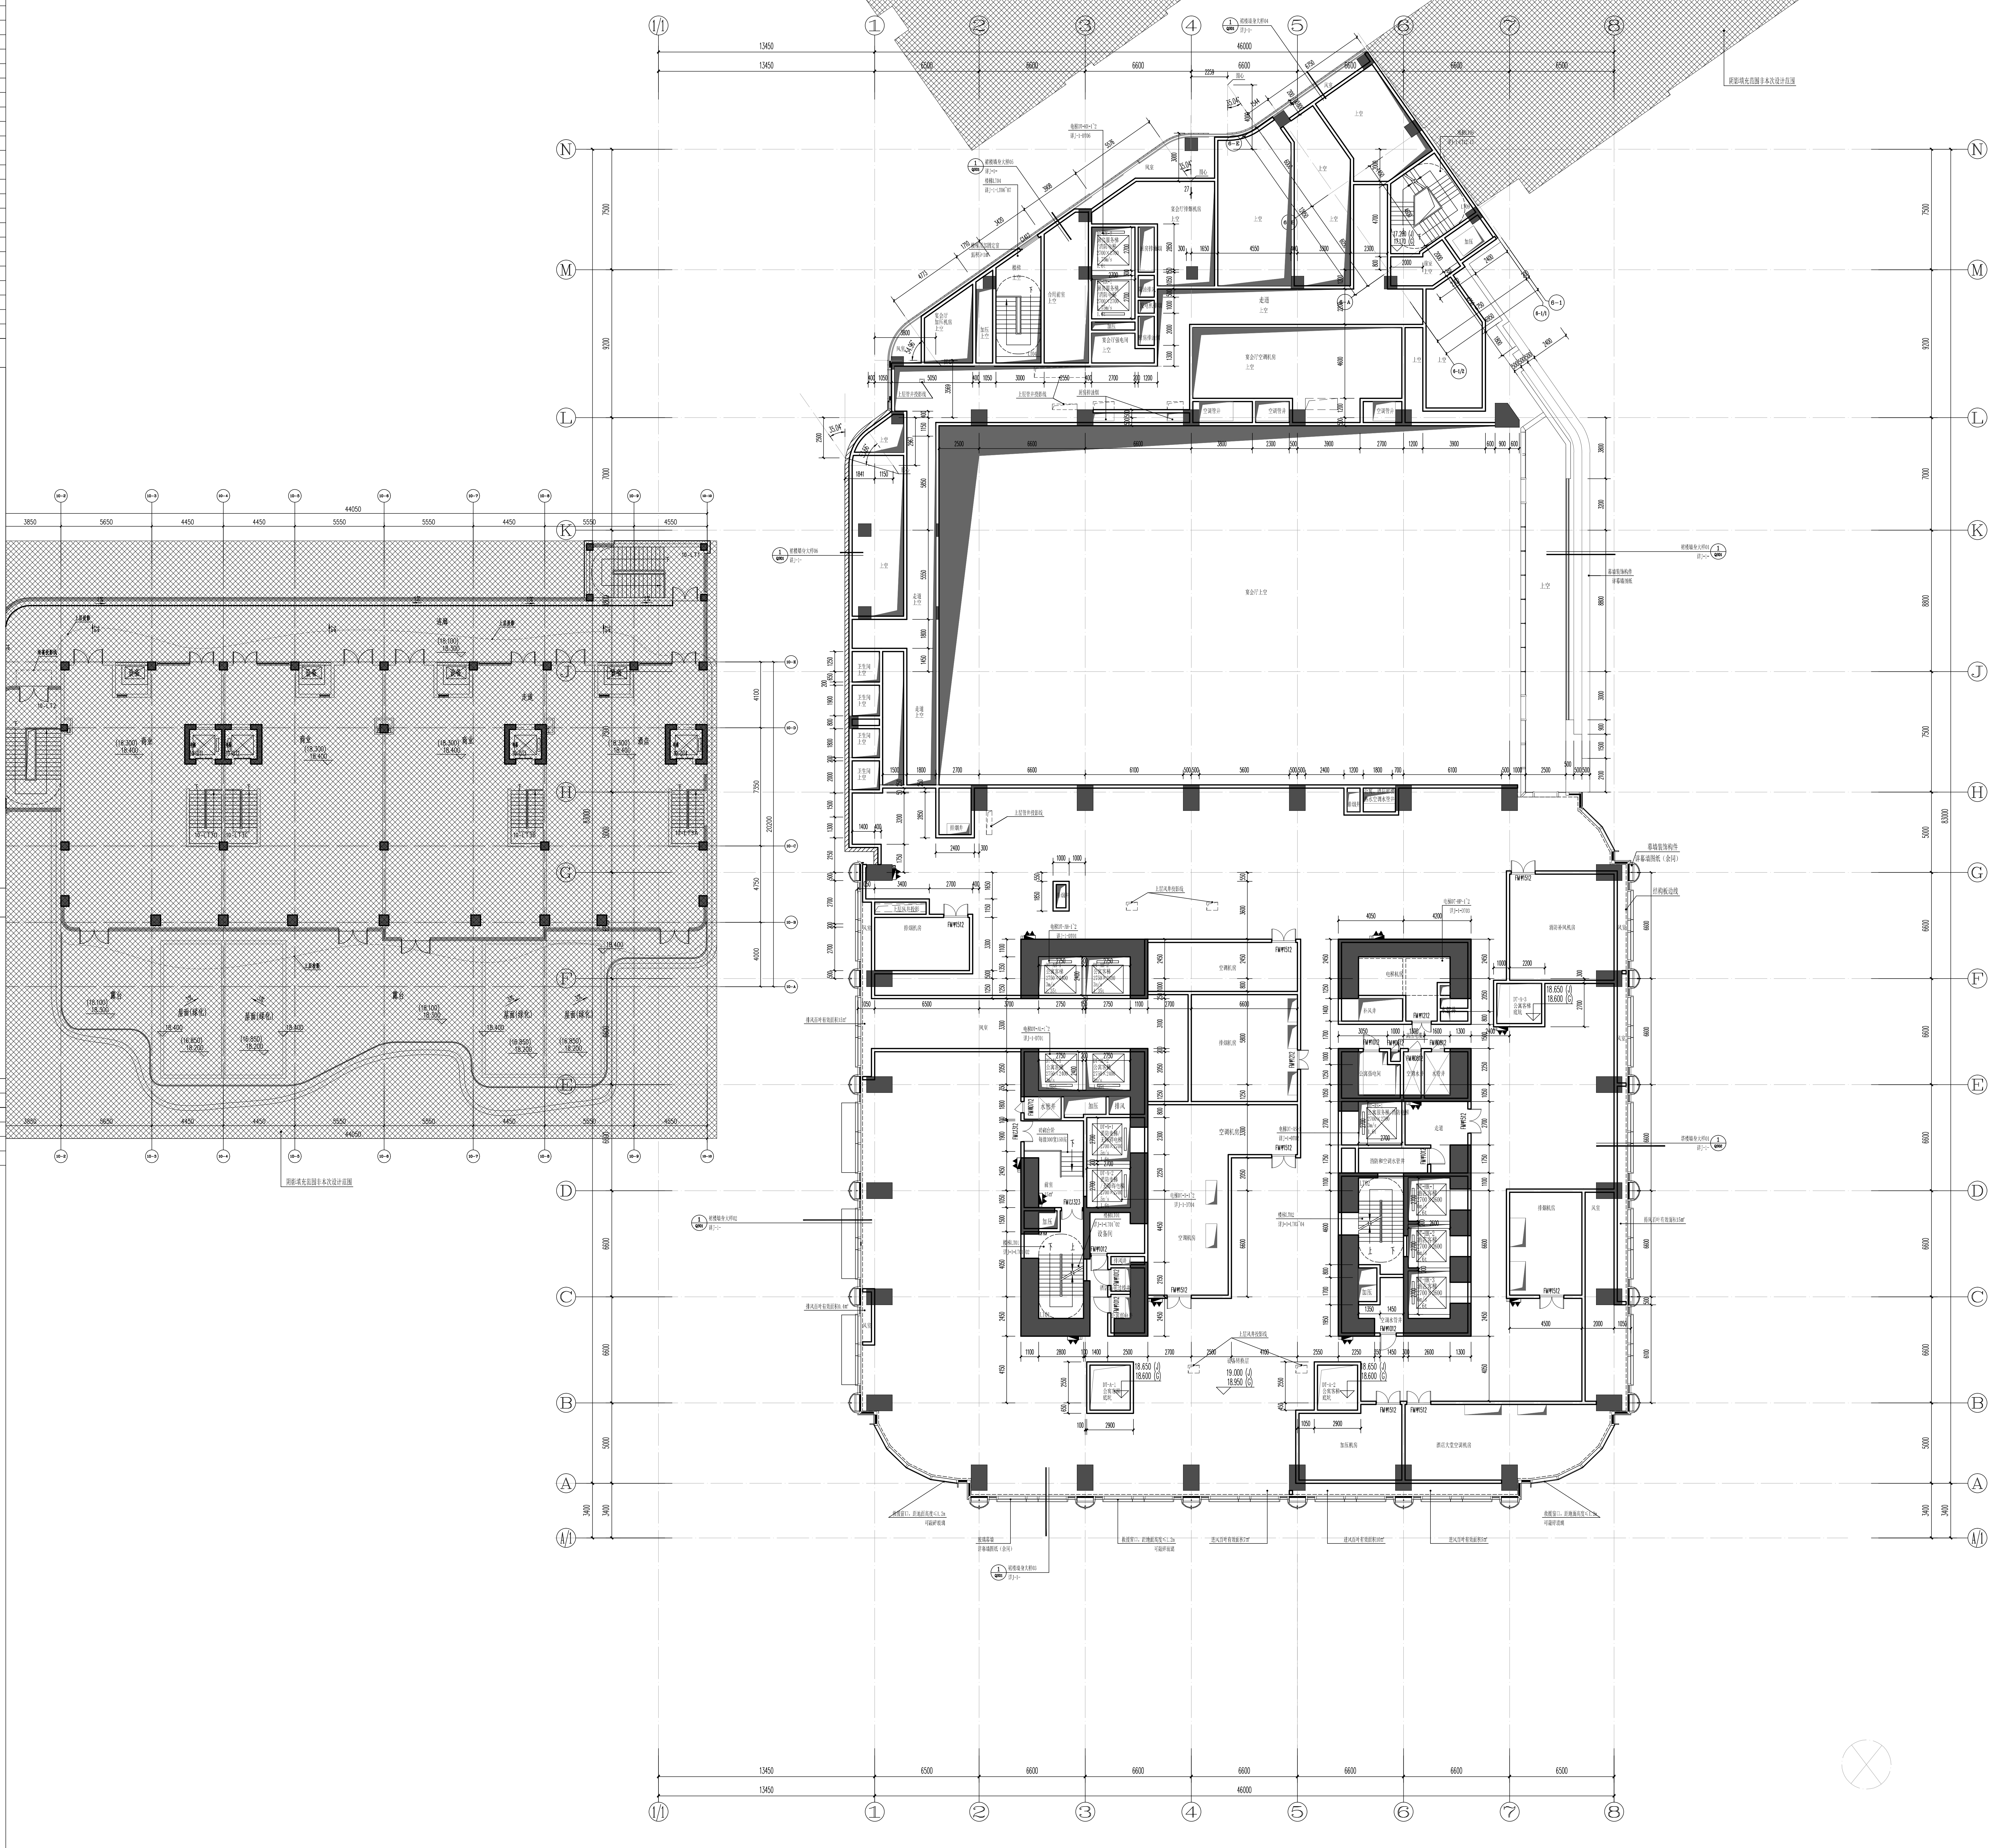

阴影填充范围非本次设计范围
宴会厅上空
宴会厅排烟机房
宴会厅空调机房
宴会厅加压机房
宴会厅强电间
合用前室
走道
上空
排烟机房
空调机房
电梯机房
补风井
公寓强电间
消防和空调水管井
消防补风机房
加压机房
酒店大堂空调机房
设备转换层
19.000 (J)
18.950 (G)
18.650 (J)
18.600 (G)
连廊
商业
酒店
露台
屋面(绿化)
幕墙装饰构件
详幕墙图纸（余同）
结构板边线
救援窗口，距地面高度≤1.2m
可敲碎玻璃
进风百叶有效面积10㎡
进风百叶有效面积7㎡
进风百叶有效面积5㎡
排风百叶有效面积15㎡
上层风井投影线
13450
46000
6500
6600
6500
(1/1)
①
②
③
④
⑤
⑥
⑦
⑧
N
M
L
K
J
H
G
F
E
D
C
B
A
A/1
83000

1 比例 1:150 设备转换层平面图

广州市设计院集团有限公司
GUANGZHOU DESIGN INSTITUTE GROUP CO., LTD.

工程设计甲级资质证书编号：A244007378
工程勘察甲级资质证书编号：B244007378

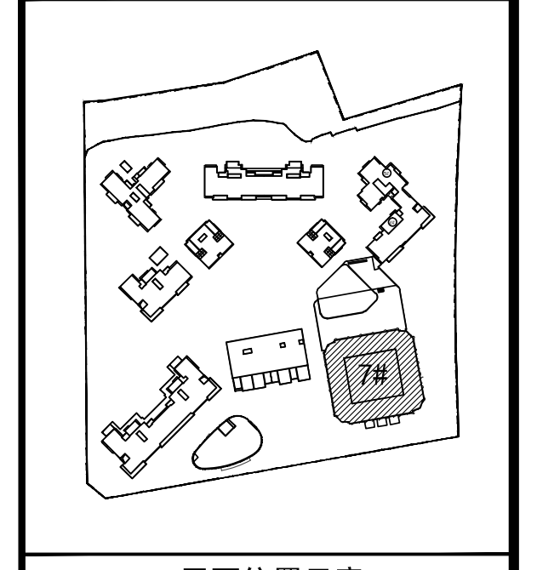

平面位置示意 Key Plan

版本号	日期	修改内容	修订者
		修订栏	

图纸条码

总工程师	赵松林	赵松林
审定	黄孝颖	黄孝颖
审核	张林汉	张林汉
设计总负责人	黄孝颖	黄孝颖
	张林汉	张林汉
专业负责人	宋延勇	宋延勇
校核	石昊洋	石昊洋
设计	胡伟航	胡伟航

建设单位	佛山市禅城区保宸置业有限公司		
工程名称	保利天珺秀台7#		
业务号	21-347	专业	建筑
设计阶段	施工图		
图纸名称	三层设备转换层平面图		
图号	J-1-PM07	版本号	
出图日期	2023.08.02	序号	

版权所有，不得复制、套用或公开。
ALL RIGHTS RESERVED.