

会 员	建 筑	宋延勇
登 记	结 构	邓艳青
栏	给 排 水	甘兆麟
	电 气	蔡泽炯

图例

厨房门550x550
 结构降板400
 结构降板100
 回填500
 回填300

建筑专业说明:

(1) 除特别注明外,“H”为楼层的建筑面标高,“h”为楼层的结构标高,结构标高和建筑面标高同时标注时,标高后加(1)表示为建筑完成面标高,标高后加(G)表示为结构面标高。

(2) 除特别注明外,所有的内墙墙厚为200mm。

(3) 除特别注明外,门框均为200mm,或门位于所在房间(或走廊)的正中。

(4) 除特别注明外,各类管井、配电间、强电间、空调机房的建筑标高为h+0.05,结构标高为h,弱电间、通讯间以及其他房间、通道、门厅对应的完成面标高为当层楼面建筑标高“H”,对应的结构标高为当层楼面结构标高“h”,卫生间的完成面标高为H+0.015,结构面标高详见平面图标注。

(5) 水管、地漏、雨水口、排水留孔的大小及具体位置以给排水专业图纸位置。

(6) 电间内的强、弱电上线井处,均设砖砌防水100(宽X100)(高)。

(7) 强电间、配电间、水管井、空调水管井、空调机房、避难楼层的加压机房及排烟机房等房间、管井设100宽C15混凝土门槛,门槛外边线内退房间端的外边线100,比房间、管井外地面完成面高200mm,门设在门槛外一侧。

(8) 建筑物内除风管井外的水管井、管道每层在楼板处按结构设置预埋,待管道安装后用同样标号的混凝土封堵,电缆井的封堵做法可参照国标GB50105《电缆防火阻燃设计与施工》第16页的做法。

(9) 所有结构剪力墙或柱尺寸均以结构施工图为准,各设备专业预留孔洞请同时详该设备专业图纸进行施工。

(10) 内墙及顶棚变化详见中南北11ZJ111(11ZJ111)④④;楼面平接变化预埋详中南北图集11ZJ111(11ZJ111)④④;外墙变形缝详幕墙专业深化设计图;原屋变形缝详专业公司深化图。

(11) 首层人行出入口位置室外高差15mm,以斜面过渡,出入口位置排水沟的雨水篦子的孔洞宽度不大于15mm。

(12) 除设备房、各类管井及核心筒内的楼梯间等部位外,室内其他区域隔墙另详二次装修深化图纸。

(13) 地下室一层及首层室外场地、各层阳台或露台、屋顶等室外区域需另详景观专业深化图纸。

(14) 外墙幕墙、屋顶采光天窗需另详幕墙专业深化图纸。建筑幕墙应在每层楼板外沿处采取符合国家相关规范规定的防火措施,幕墙与每层楼板、隔墙处的缝应应用防火封堵材料封堵。


防火分区说明

各层均设置自动喷水灭火系统和自动报警系统

图例:

消防电梯
 楼梯间
 安全口
 安全口(带门)
 防火分区界线
 疏散距离

楼型	防火分区	防火分区面积	功能	各疏散楼梯使用人数	使用人数	所需疏散宽度或面积	实际疏散宽度或面积
E十三楼	防火分区7-13-F	1819.96	服务公寓	1786.18	42	0.12	
			其他辅助	33.75			
			合计	1820.00	42	0.12	0.12

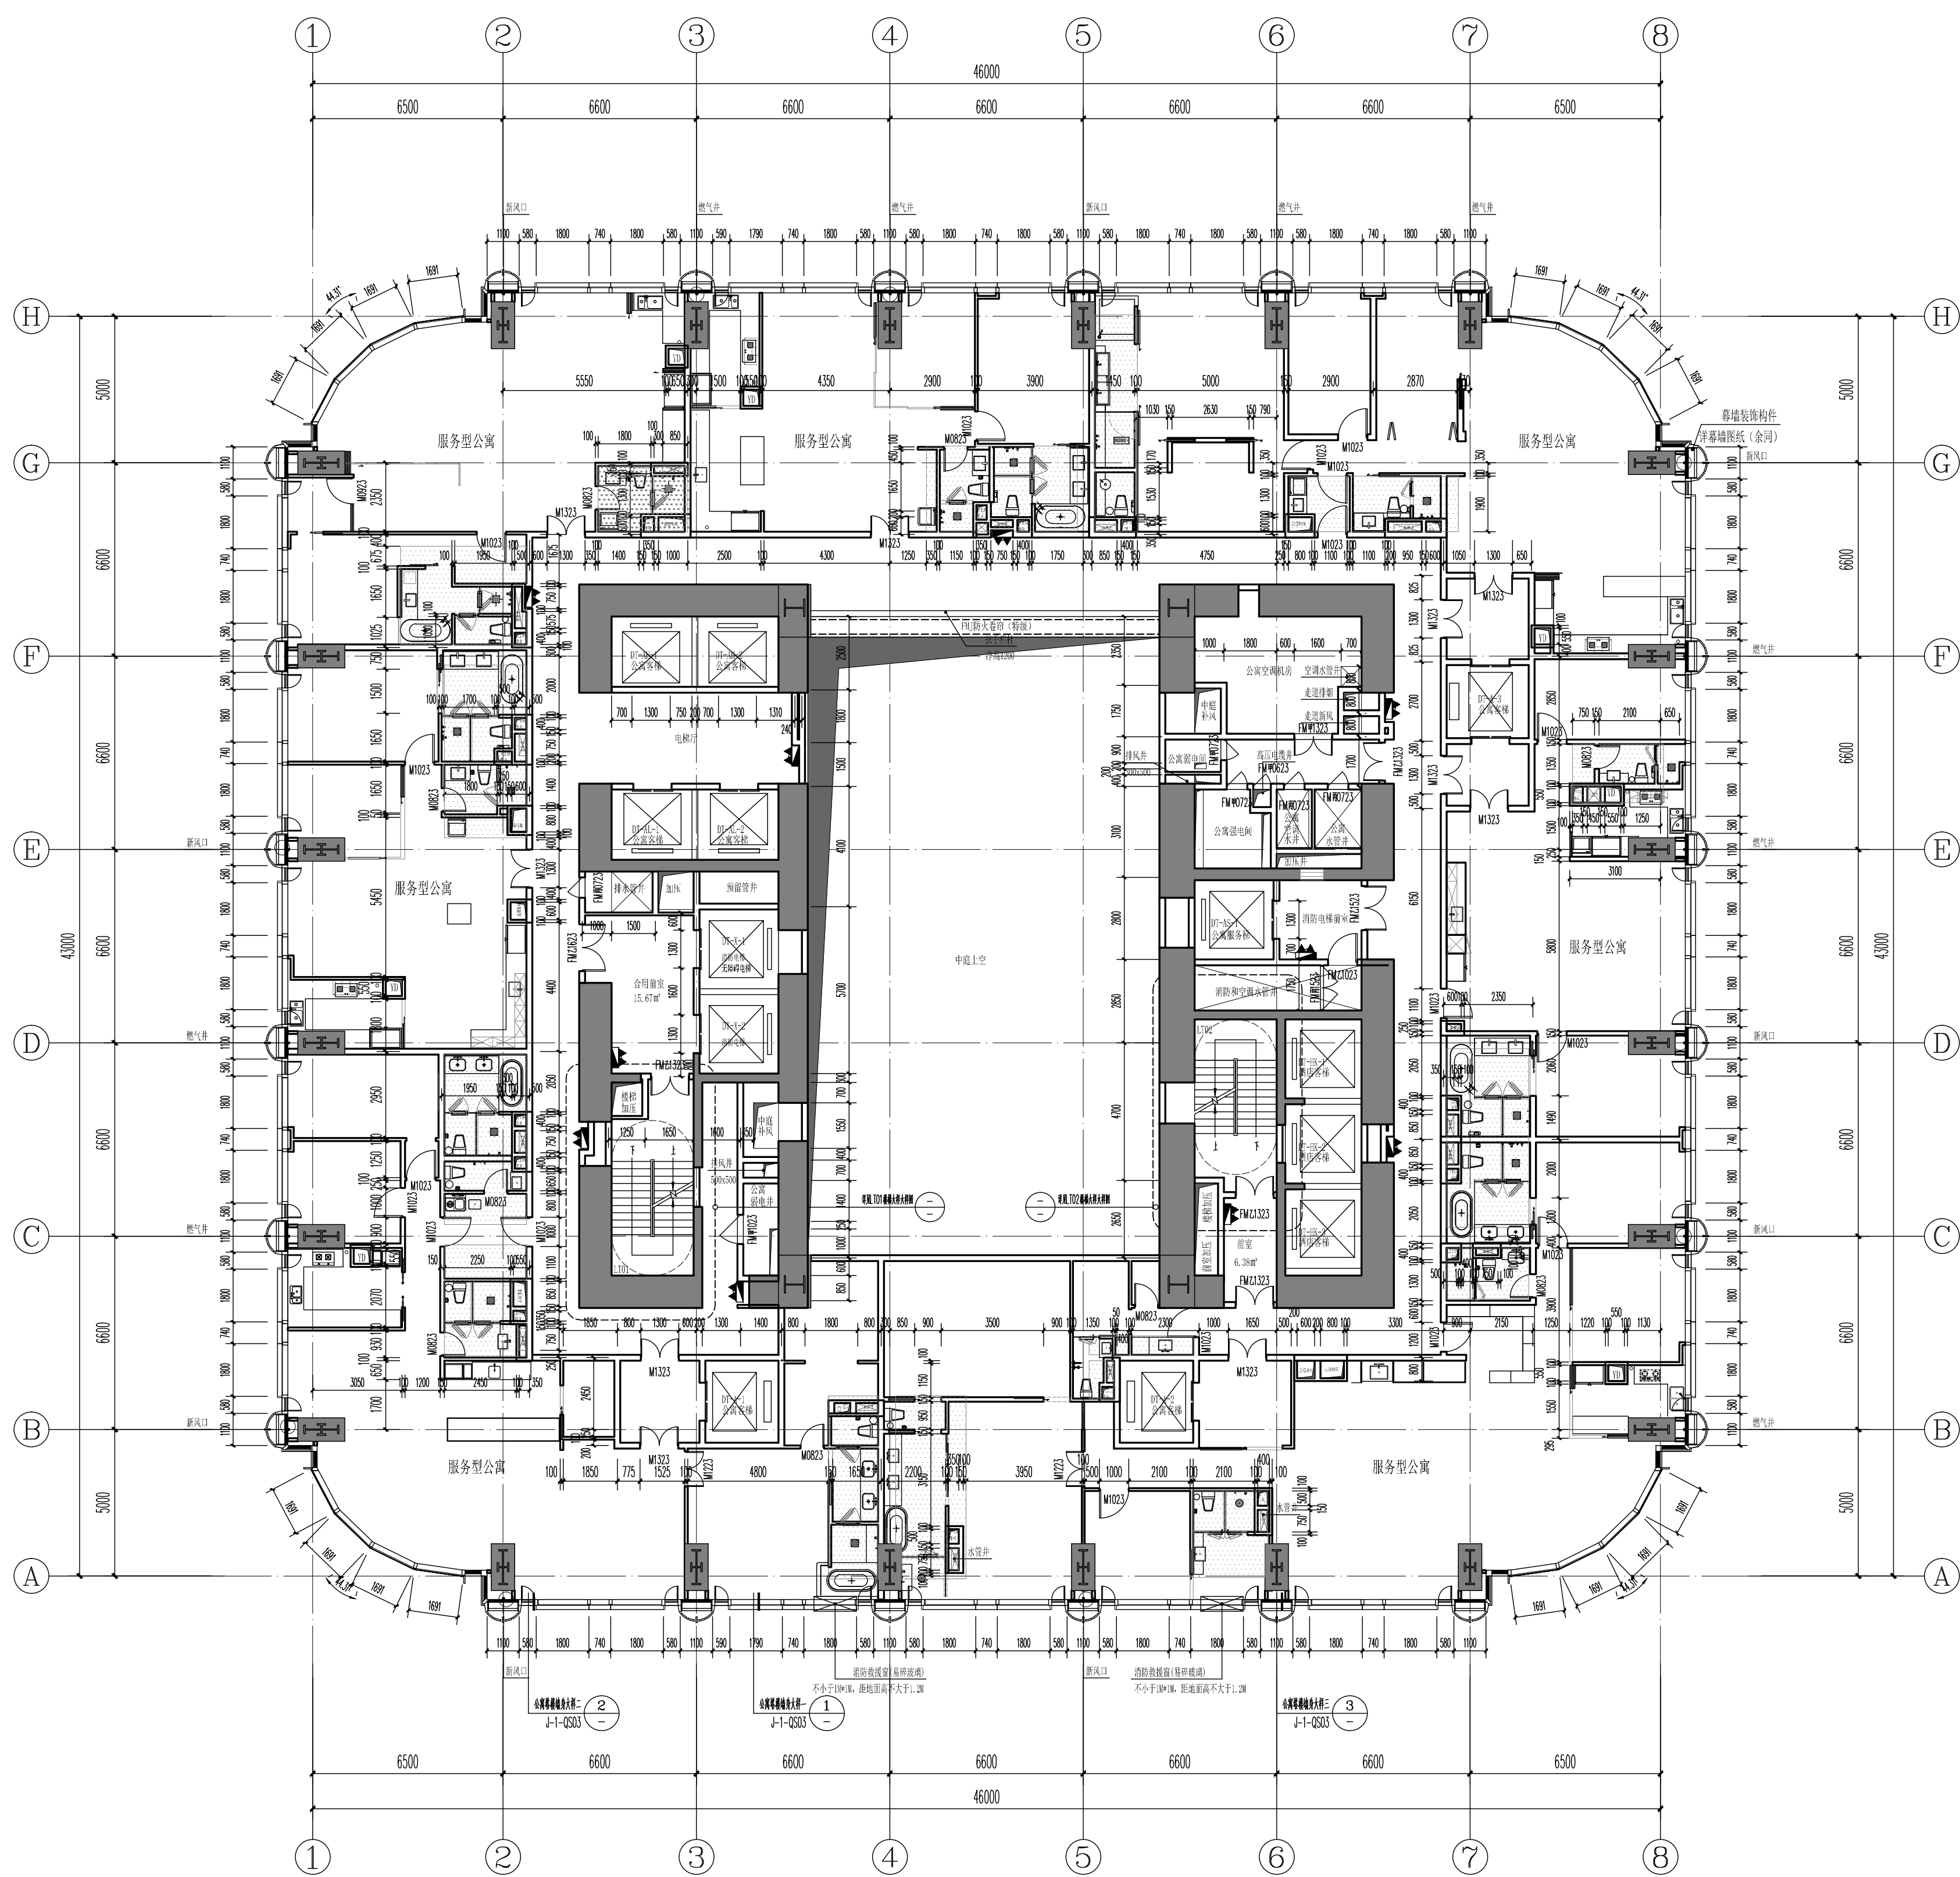

七~十三层平面图 1:150

北				广州市设计院集团有限公司 GUANGZHOU DESIGN INSTITUTE GROUP CO., LTD. 工程设计甲级资质证书编号：A244007378 工程勘察甲级资质证书编号：B244007378		
佛山保利天珺7#楼层高表				平面位置示意 Key Plan		
楼层		层高 (m)	建筑标高 (J) H	结构标高 (G) h		
屋面设备层						
屋面	屋面层		246.300	246.000		
	58F	6000	240.000	239.920		
	57F设备夹层	2150	237.850	237.800		
	57F	6000	231.850	231.800		
	56F	4300	227.550	227.470		
	55F	3800	223.750	223.670		
	54F	3800	219.950	219.870		
	53F	3800	216.150	216.070		
	52F	3800	212.350	212.270		
	51F	3800	208.550	208.470		
	50F	3800	204.750	204.670		
	49F管线层	1500	203.250	203.200		
	49F (避难层)	4200	199.050	199.000		
	48F	3800	195.250	195.170		
	47F	3800	191.450	191.370		
	46F	3800	187.650	187.570		
	45F	3800	183.850	183.770		
	44F设备夹层	2150	181.700	181.650		
	酒店	44F (酒店大堂)	7500	174.200	174.120	
		43F设备夹层	2150	172.050	172.000	
		43F	3600	168.450	168.400	
		42F	3600	164.650	164.600	
		41F	3600	161.250	161.200	
		40F	3600	157.650	157.600	
		39F管线层	1500	156.150	156.100	
		39F (避难层)	4200	151.950	151.900	
		38F	3600	148.350	148.300	
		37F	3600	144.750	144.700	
		36F	3600	141.150	141.100	
		35F	3600	137.550	137.500	
		34F	3600	133.950	133.900	
		33F	3600	130.350	130.300	
		32F	3600	126.750	126.700	
		31F	3600	123.150	123.100	
		30F	3600	119.550	119.500	
		29F	3600	115.950	115.900	
		28F	3600	112.350	112.300	
		27F	3600	108.750	108.700	
		26F管线层	1500	107.250	107.200	
		26F (避难层)	4200	103.050	103.000	
		25F	3600	99.450	99.400	
24F		3600	95.850	95.800		
23F		3600	92.250	92.200		
22F		3600	88.650	88.600		
21F		3600	85.050	85.000		
20F		3600	81.450	81.400		
19F		3600	77.850	77.800		
18F		3600	74.250	74.200		
17F		3600	70.650	70.600		
16F		3600	67.050	67.000		
15F		3600	63.450	63.400		
14F管线层		1500	61.950	61.900		
14F (避难层)		4200	57.750	57.700		
13F		3600	54.150	54.100		
12F		3600	50.550	50.500		
11F		3600	46.950	46.900		
10F		3600	43.350	43.300		
9F		3600	39.750	39.700		
8F	3600	36.150	36.100			
7F	3600	32.550	32.500			
6F	3600	28.950	28.900			
5F	3600	25.350	25.300			
公寓	4F (公寓大堂)	4200	21.150	21.100		
	3F设备夹层	2150	19.000	18.950		
	3F	5500	13.500	13.450		
	2F (酒店大堂)	5500	8.000	7.920		
裙房	1F (公寓、宴会大堂)	8000	0.000	-0.080		
	B1F (裙房后勤)	6650	-6.650	-6.750		
	B2F (局部人防区)	3500	-10.150	-10.250		
	地下室 B3F (整体人防区)	3600	-13.750	-14.000		
地下室						

版次号	日期	修改内容	修订者
		修 订 栏	
图 纸 条 码			
总 设 计 师		赵松林	赵松林
审 定	黄孝颖	黄孝颖	
审 核	张林汉	张林汉	
设 计 总 负 责 人	黄孝颖	黄孝颖	
	宋廷勇	宋廷勇	
专 业 负 责 人	石昊洋	石昊洋	
	宋廷勇	宋廷勇	
校 核	宋廷勇	宋廷勇	
设 计			
建 设 单 位	佛山市禅城区 保宸置业有限公司		
工 程 名 称	保利天珺秀台7#		
业 务 号	21-347	专业	建筑
设计阶段	施工图		
图 纸 名 称	七~十二层 平面图		
图 号	J-1-PM10	版 本 号	
出图日期	2023. 08. 02	序 号	
版权所有，不得复制、套用或公开。 ALL RIGHTS RESERVED.			