

会 员	建 筑	宋延勇
登 记	结 构	邓艳青
栏	给 排 水	甘兆麟
	电 气	蔡泽炯

建筑专业说明:

- (1)除特别注明外,“H”为楼层的建筑标高,“h”为楼层的结构标高,结构标高和建筑标高同时标出时,标高加“(J)”表示为建筑完成楼面标高,标高加“(G)”表示为结构楼面标高。
- (2)除特别注明外,所有的内墙顶均为200mm。
- (3)除特别注明外,门坎均为200mm,或门位于所在房间(或走廊)的正中。
- (4)除特别注明外,各类管井、配电间、强电间、空调机房的建筑标高为 $h+0.05$,结构标高为 h ,弱电间、通讯间以及其他房间、通道、门厅对应的完成面标高为当楼层建筑标高 h 时,对应的结构标高为当楼层结构标高 h 。卫生间间的完成面标高为 $h-0.015$,结构面标高为 h 平面图标注。
- (5)水管、地漏、水龙头、排水孔的大小及具体位置以给排水专业图纸位置。
- (6)电线管的强、弱电线上排,均按砌砖反水(墙)X100(高)。
- (7)强电间、配电间、水管、空调水管、空调机房、避难楼层的加压机房及排烟机房等房间,并设置100X30混凝土门框,门框外边线位于房间墙体的外边线100,内墙面、管井外边线完成面高200mm,门设在门框外侧。
- (8)建筑物内除风管井外的水管井、管道每层在楼板上按结构设钢箍,待管道安装后用同样标号的混凝土封填,封堵后的封堵做法可参照国标650105《电线防火封堵设计与施工》第16页的做法。
- (9)所有结构梁、墙或柱尺寸均以结构施工图为准,各设备专业预留孔洞请同时详该设备专业图纸进行施工。
- (10)《地下室及地下室建筑详见中南标11Z111》(图例):楼面板变形缝做法详中南标图集11Z111(图例),外檐变形缝详建筑专业深化设计图,屋顶变形缝详专业公司深化图。


(11)首层行人出入口位置室外高差15mm,以斜面过渡;出入口位置排水沟的雨水篦子的孔洞宽度不大于15mm

(12)设备用房、各类管井及核心区域内的楼梯间等部位,室外其他区域另详二次装修深化图。


(13)地下二层及首层室外场地、各层平台或露台、屋顶等室外区域另详景观专业深化图。

(14)外挑楼梯、屋顶露台、大堂前厅另详建筑专业深化图纸。建筑幕墙应在建筑幕墙外饰处采取符合国家相关规范规定的防火措施,幕墙与每层楼板、隔墙处的缝应采用防火封堵材料封堵。

防火分区说明

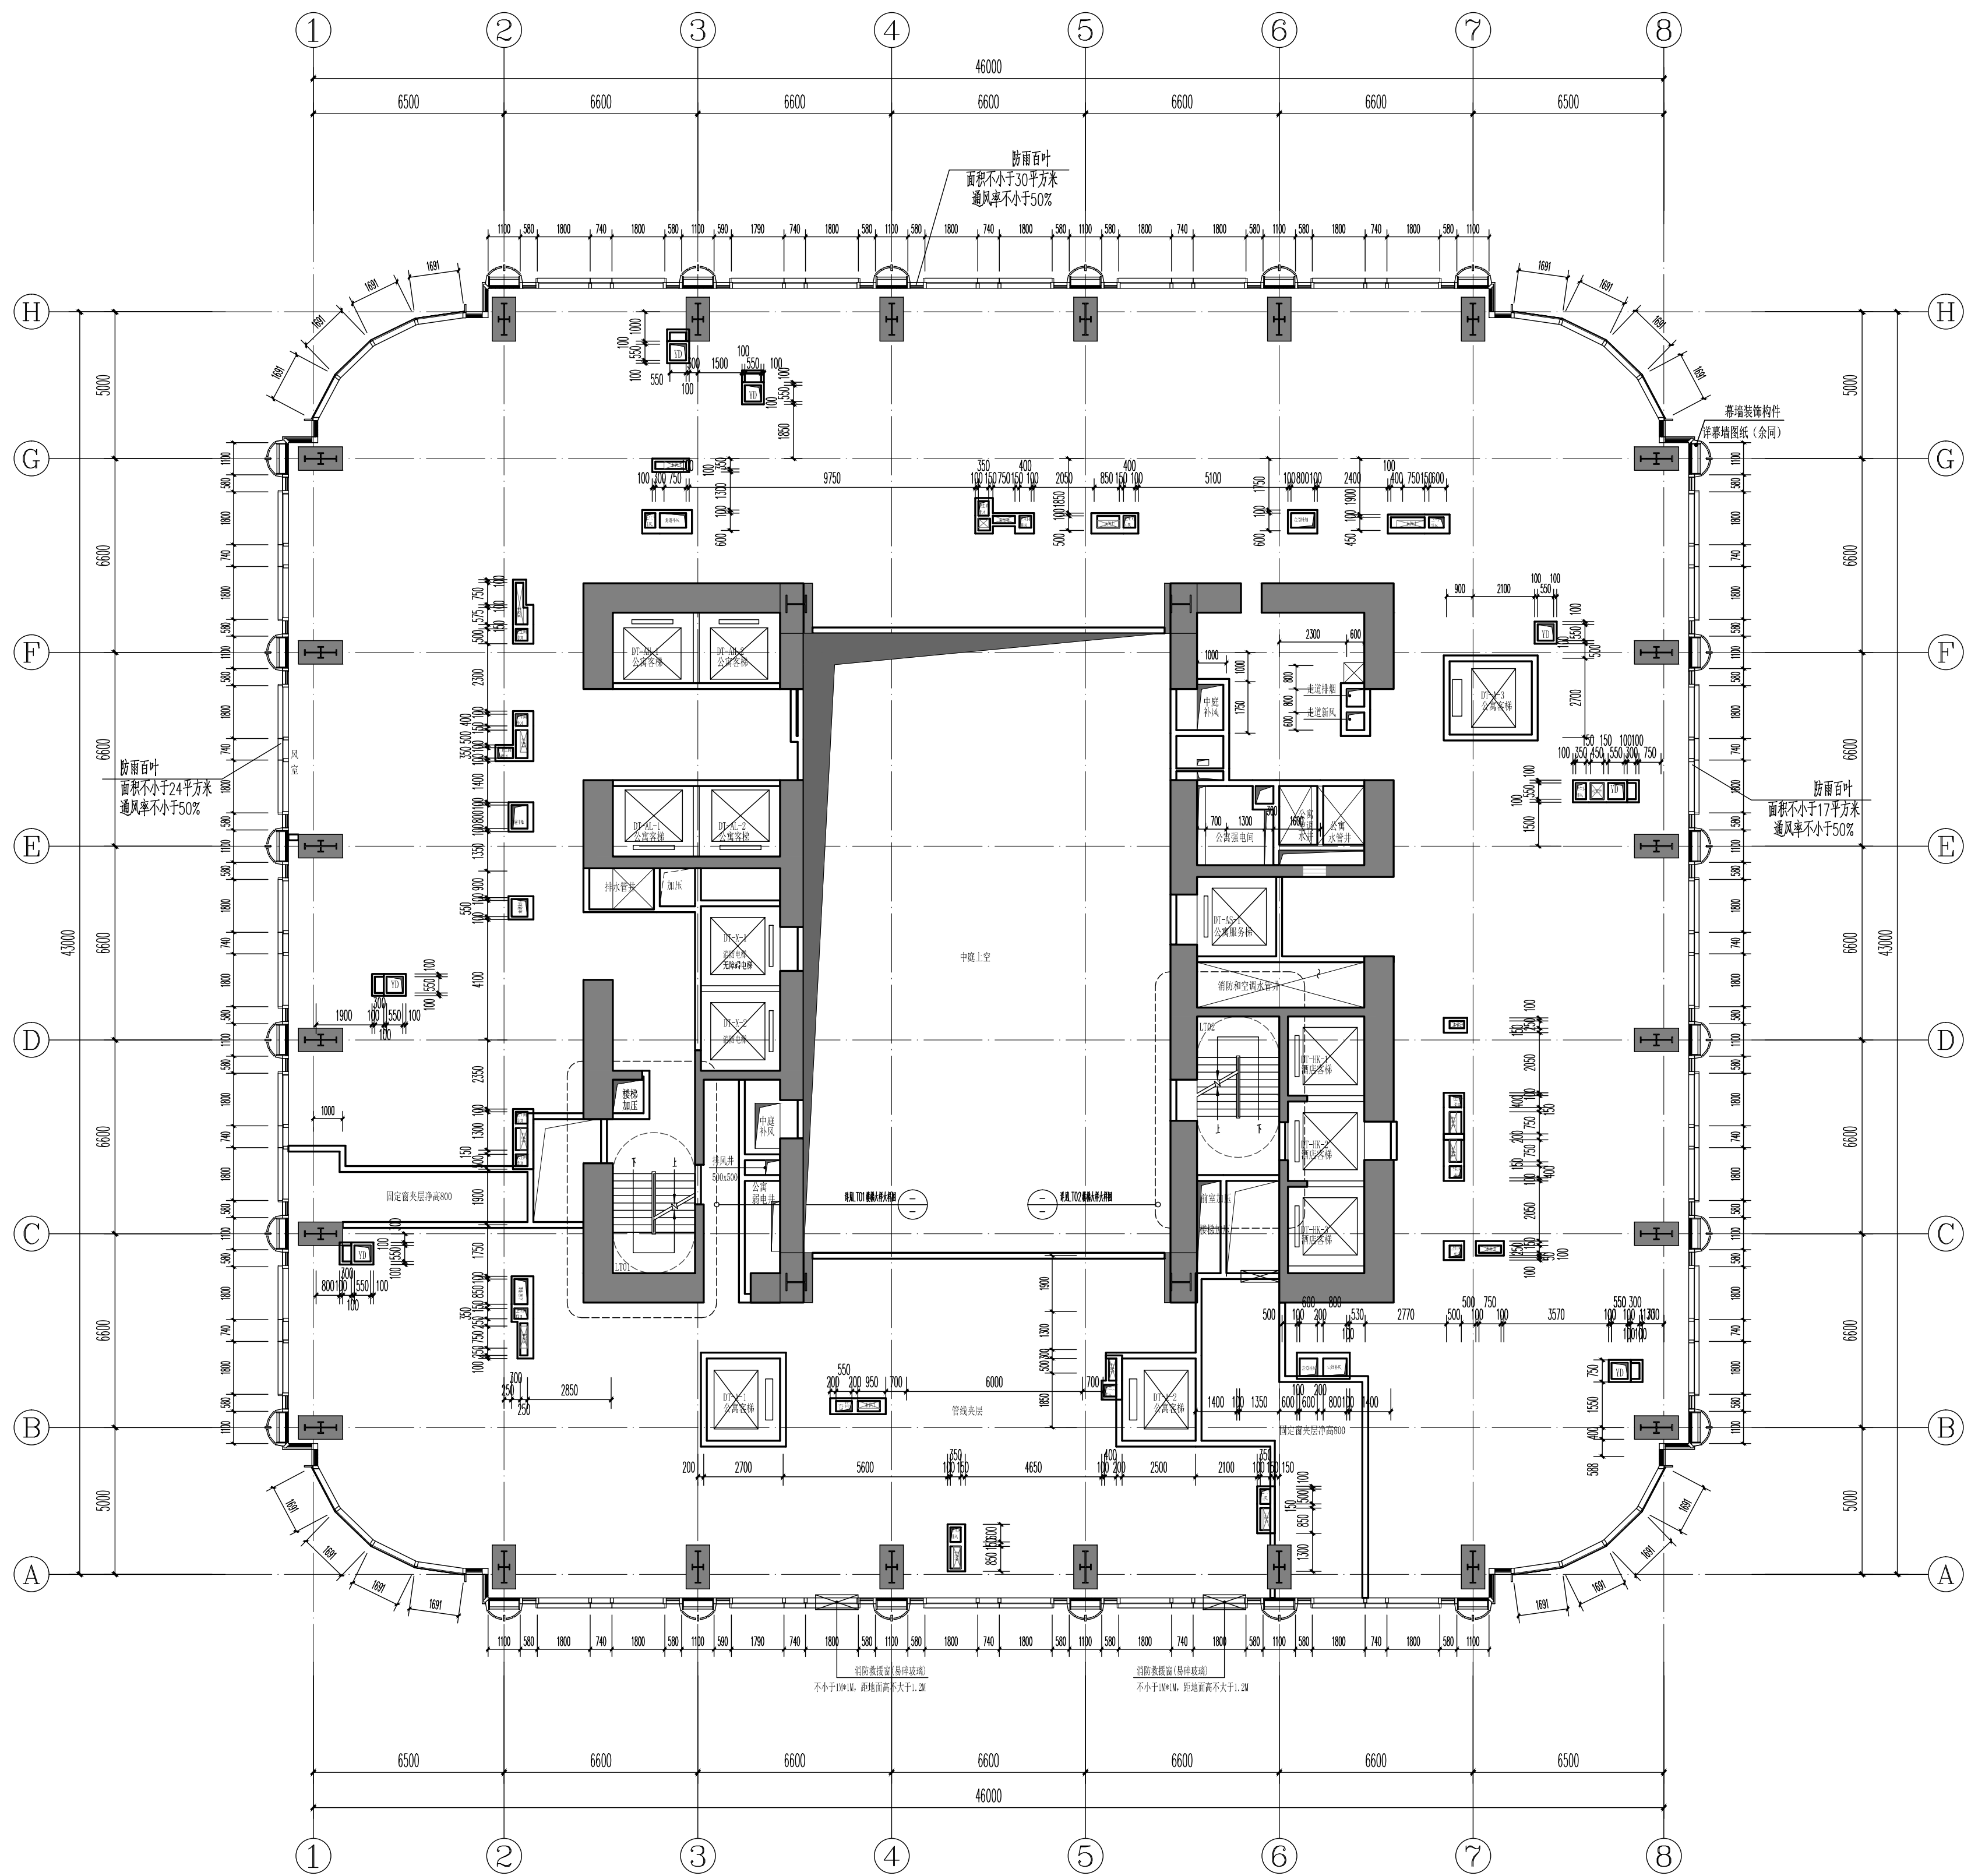

十四夹层平面图 1:150

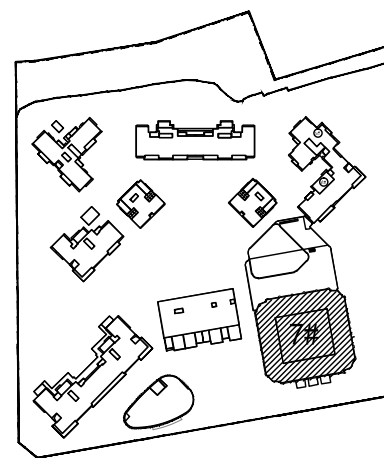北					广州市设计院集团有限公司 GUANGZHOU DESIGN INSTITUTE GROUP CO., LTD. 工程设计甲级资质证书编号：A240007378 工程勘察甲级资质证书编号：B240007378  平面位置示意 Key Plan				
佛山保利天珺T#楼层高表									
	楼层	层高 (m)	建筑标高 (J) H	结构标高 (G) h					
屋面	屋面设备层								
	屋面层		246.300	246.000					
	58F	6000	240.000	239.920					
酒店	57F设备夹层	2150	237.850	237.800					
	57F	6000	231.850	231.800					
	56F	4300	227.550	227.470					
	55F	3800	223.750	223.670					
	54F	3800	219.950	219.870					
	53F	3800	216.150	216.070					
	52F	3800	212.350	212.270					
	51F	3800	208.550	208.470					
	50F	3800	204.750	204.670					
	49F管线层	1500	203.250	203.200					
	49F（避难层）	4200	199.050	199.000					
	48F	3800	195.250	195.170					
	47F	3800	191.450	191.370					
	46F	3800	187.650	187.570					
	45F	3800	183.850	183.770					
	44F设备夹层	2150	181.700	181.650					
	44F（酒店大堂）	7500	174.200	174.120					
	43F设备夹层	2150	172.050	172.000					
	43F	3600	168.450	168.400					
	42F	3600	164.650	164.600					
	41F	3600	161.250	161.200					
	40F	3600	157.650	157.600					
	39F管线层	1500	156.150	156.100					
	39F（避难层）	4200	151.950	151.900					
	38F	3600	148.350	148.300					
	37F	3600	144.750	144.700					
	36F	3600	141.150	141.100					
	35F	3600	137.550	137.500					
	34F	3600	133.950	133.900					
	33F	3600	130.350	130.300					
32F	3600	126.750	126.700						
31F	3600	123.150	123.100						
30F	3600	119.550	119.500						
29F	3600	115.950	115.900						
28F	3600	112.350	112.300						
27F	3600	108.750	108.700						
26F管线层	1500	107.250	107.200						
26F（避难层）	4200	103.050	103.000						
25F	3600	99.450	99.400						
24F	3600	95.850	95.800						
23F	3600	92.250	92.200						
22F	3600	88.650	88.600						
21F	3600	85.050	85.000						
20F	3600	81.450	81.400						
19F	3600	77.850	77.800						
18F	3600	74.250	74.200						
17F	3600	70.650	70.600						
16F	3600	67.050	67.000						
15F	3600	63.450	63.400						
14F管线层	1500	61.950	61.900						
14F（避难层）	4200	57.750	57.700						
13F	3600	54.150	54.100						
12F	3600	50.550	50.500						
11F	3600	46.950	46.900						
10F	3600	43.350	43.300						
9F	3600	39.750	39.700						
8F	3600	36.150	36.100						
7F	3600	32.550	32.500						
6F	3600	28.950	28.900						
5F	3600	25.350	25.300						
公寓	4F（公寓大堂）	4200	21.150	21.100					
裙房	3F设备夹层	2150	19.000	18.950					
	3F	5500	13.500	13.450					
	2F（酒店大堂）	5500	8.000	7.920					
	1F（公寓、宴会大堂）	8000	0.000	-0.080					
地下室	B1F（酒店后勤）	6650	-6.650	-6.750					
	B2F（局部人防区）	3500	-10.150	-10.250					
	B3F（整体人防区）	3600	-13.750	-14.000					