广州市设计院集团有限公司
GUANGZHOU DESIGN INSTITUTE GROUP CO., LTD.
工程设计甲级资质证书编号：A244007378
工程勘察甲级资质证书编号：B244007378

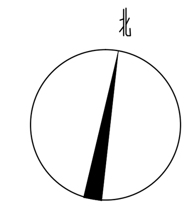

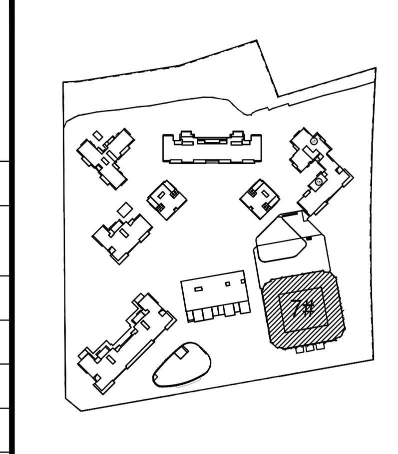

平面位置示意 Key Plan

图例

YD	厨房烟道550x550
	结构降板400
	结构降板100
	回填500
	回填300

建筑专业说明:

(1)除特别注明外，“H”为楼层的建筑面标高，“h”为楼层的结构标高。结构标高和建筑面标高同时标注时，标高后加（J）表示为建筑完成面标高，标高后加（G）表示为结构面标高。
(2)除特别注明外，所有的内墙墙厚为200mm。
(3)除特别注明外，门垛均为200mm,或门位于所在房间(或走廊)的正中。
(4)除特别注明外，各类管井、配电间、强电间、空调机房的建筑标高为h+0.05，结构标高为h。弱电间、通讯间以及其他房间、通道、门厅对应的完成面标高为当层楼面建筑标高“H”，对应的结构标高为当层楼面结构标高“h”。卫生间的完成面标高为H-0.015,结构面标高详平面图标注。
(5)水管、地漏、雨水口、排水留孔的大小及具体位置以给排水专业图纸位置。
(6)电间内的强、弱电上线井边，均设砖砌反水100(宽)X100(高)。
(7)强电间、配电间、水管井、空调水管井、空调机房、避难楼层的加压机房及排烟机房等房间、管井设100宽C15混凝土门槛，门槛外边线内退房间墙的外边线100，比房间、管井外地面完成面高200mm，门设在门槛外侧。
(8)建筑物内除风管井外的水管井、管道井每层在楼板处按结构铺设钢筋，待管道安装后用同样标号的混凝土封堵,电缆井的封堵做法可参照国标06D105《电缆防火阻燃设计与施工》第16页的做法。
(9)所有结构剪力墙或柱尺寸均以结构施工图为准,各设备专业预留孔洞请同时详该设备专业图纸进行施工。
(10)内墙及顶棚变形缝详见中南标11ZJ111 (9/A-4) (10/A-4)；楼面平接变形缝做法详中南标图集11ZJ111 (2/A-8) (10/A-9)；外墙变形缝详幕墙专业深化设计图；屋顶变形缝另详专业公司深化图。
(11)首层人行出入口位置室内外高差15mm，以斜面过渡；出入口位置排水沟的雨水箅子的孔洞宽度不大于15mm
(12)除设备房、各类管井及核心筒内的楼梯间等部位外，室内其他区域需另详二次装修深化图纸。
(13)地下一层及首层室外场地、各层阳台或露台、屋顶等室外区域需另详景观专业深化图纸。
(14)外墙幕墙、屋顶采光天窗需另详幕墙专业深化图纸。建筑幕墙应在每层楼板外沿处采取符合国家相关规范规定的防火措施，幕墙与每层楼板、隔墙处的缝隙应采用防火封堵材料封堵。

防火分区说明

各层均设置自动喷水灭火系统和自动报警系统

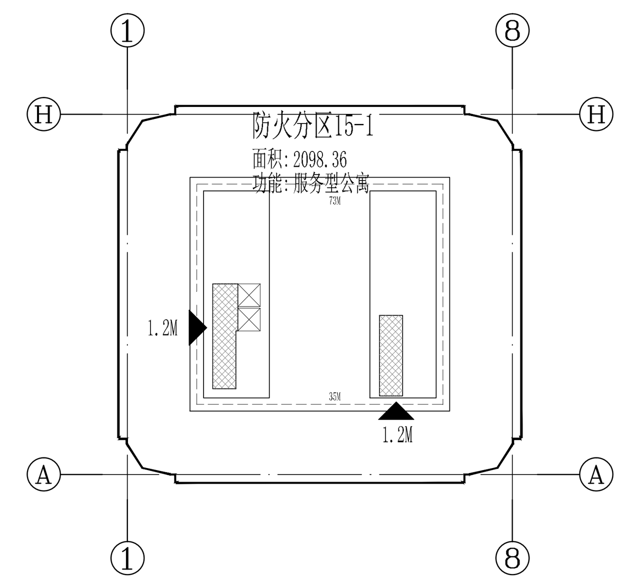

图例:						
	☒	消防电梯	▲	安全口	▭	防火分区界线
	▨	楼梯间	△	安全口(借口)	----	疏散距离

楼层	防火分区	防火分区面积	功能	各功能用房使用面积	使用人数计算公式	使用人数	需要设置疏散宽度	实际设置疏散净宽度
十五层	防火分区15-1	1819.96	服务型公寓	1786.18	每户/3.2人	42	0.42	
			其他辅助	33.78				
			合计	1819.96		42	0.42	2.40

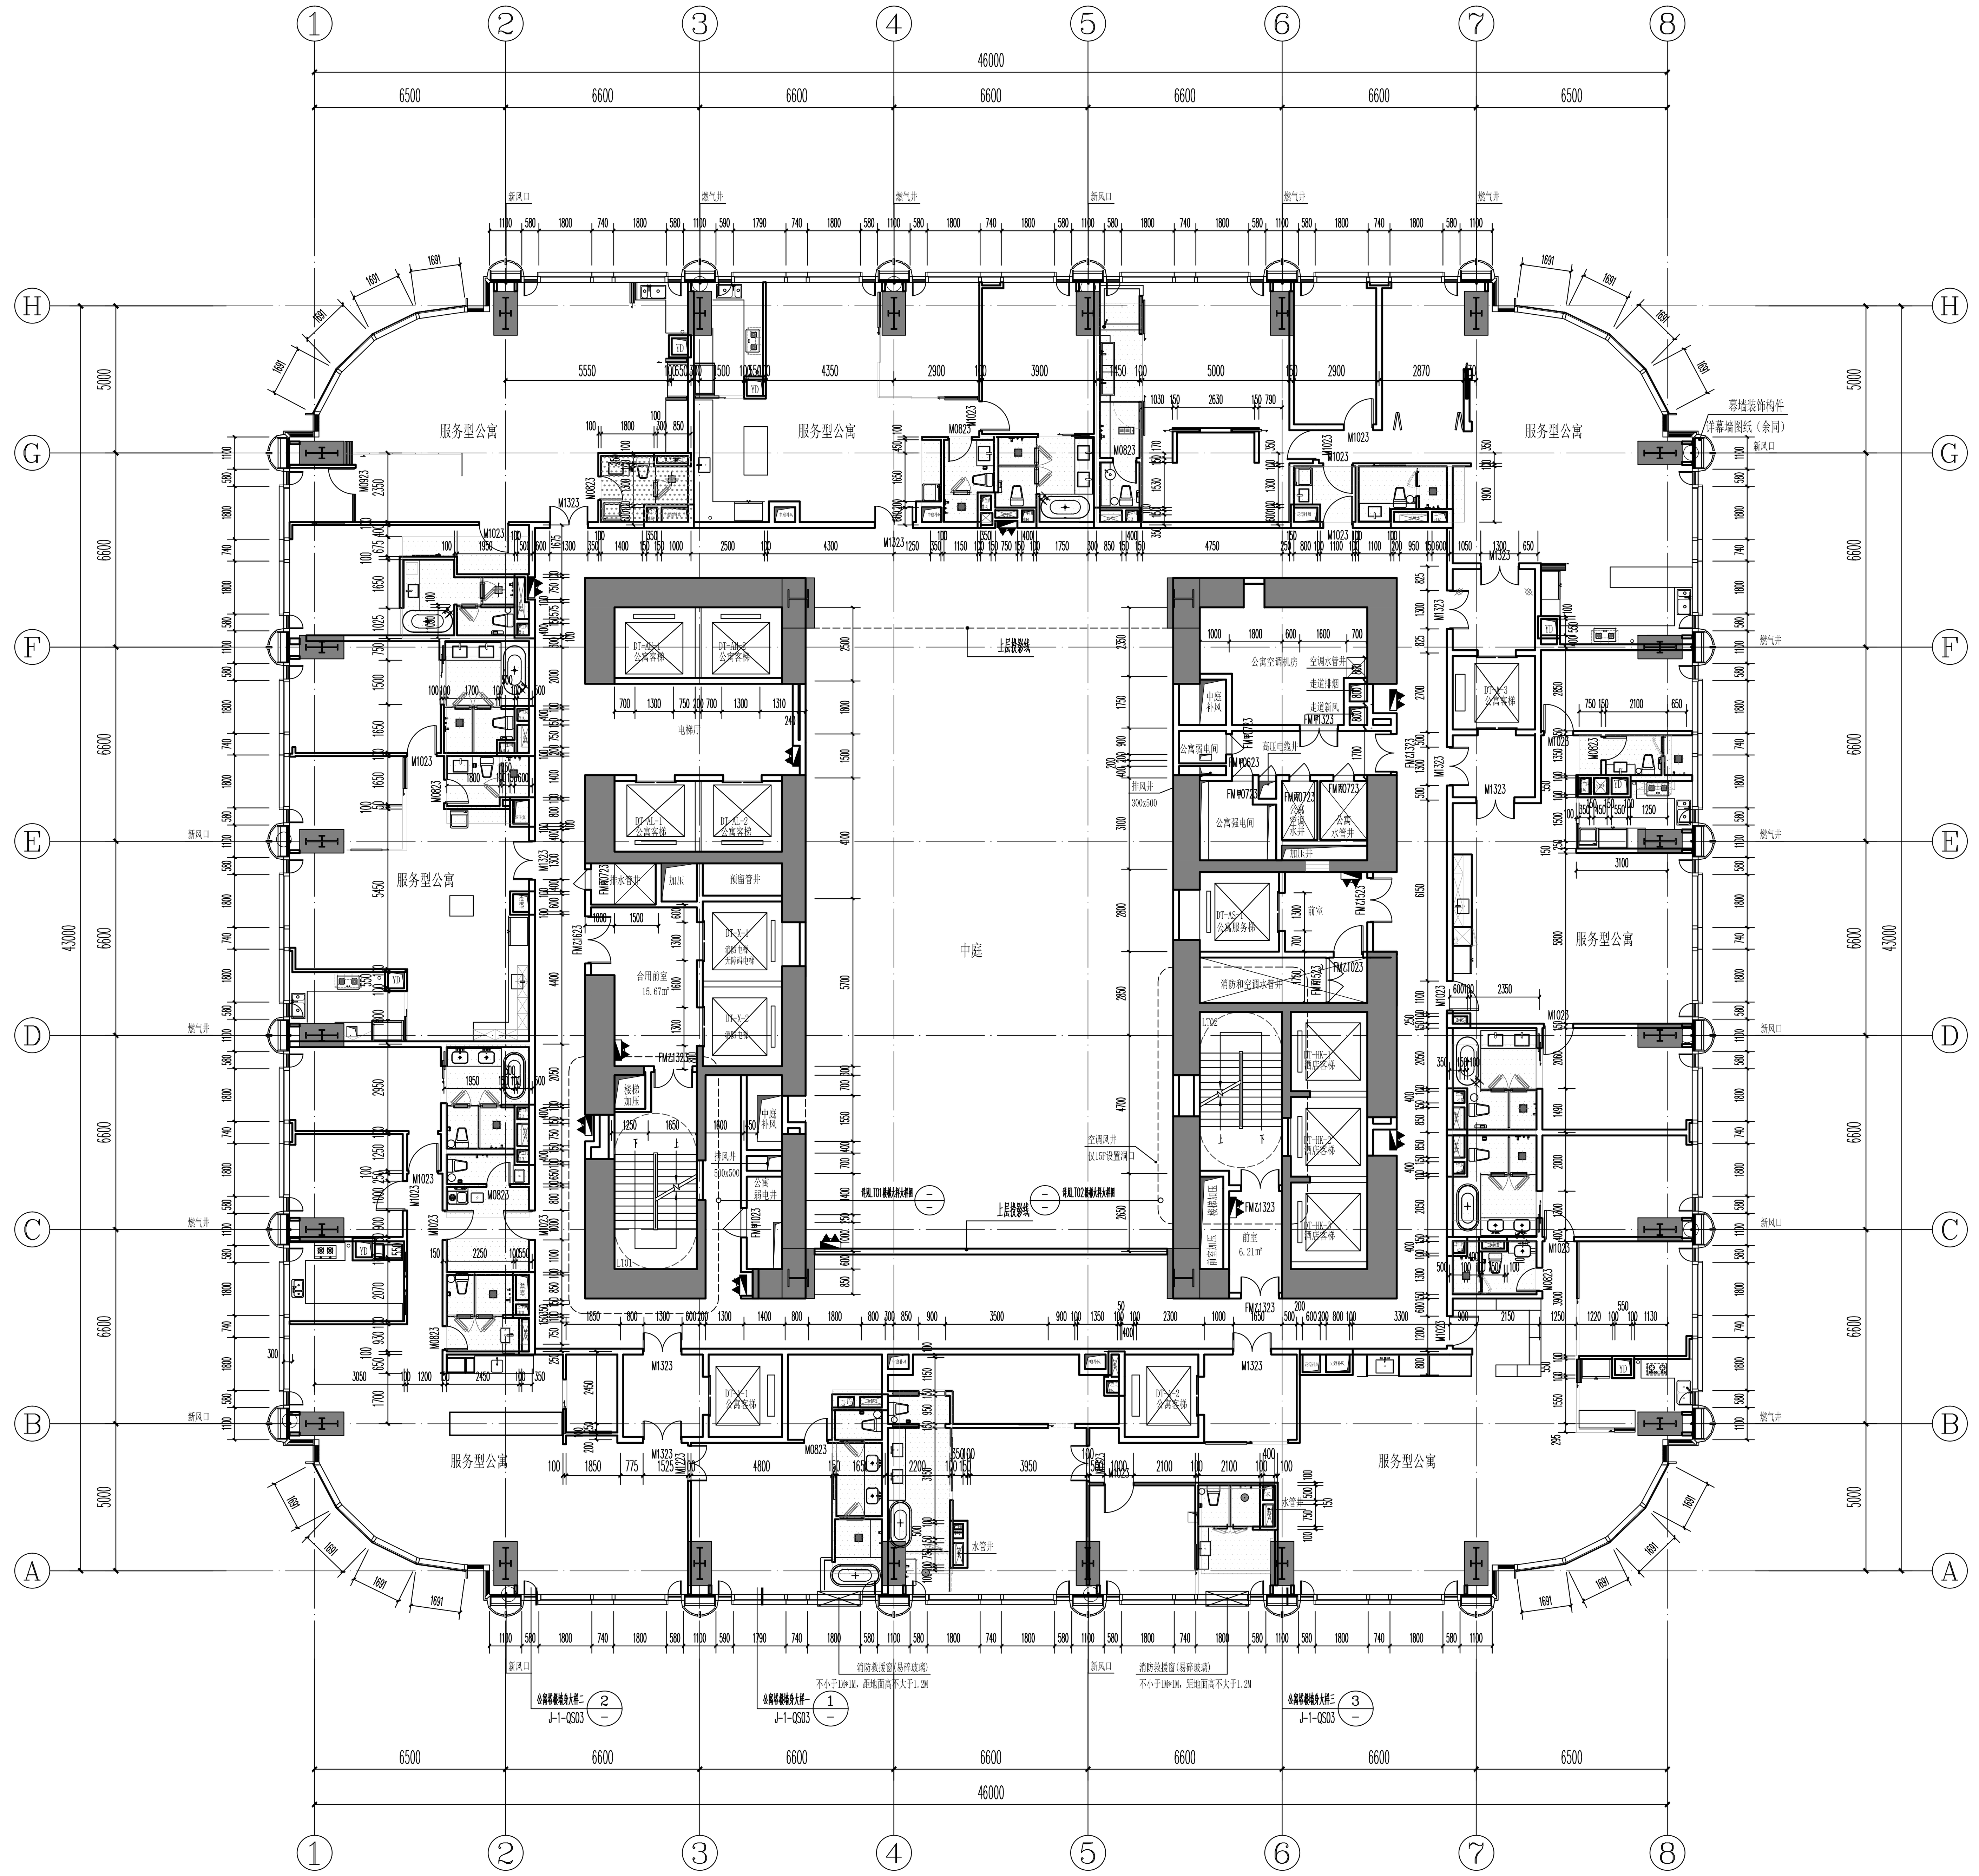

十三层、十五层平面图 1:150

佛山保利天珺7#楼层高表

	楼层	层高(mm)	建筑标高（J）H	结构标高（G）h
屋面	屋面设备层			
	屋面层		246.300	246.000
酒店	58F	6000	240.000	239.920
	57F设备夹层	2150	237.850	237.800
	57F	6000	231.850	231.800
	56F	4300	227.550	227.470
	55F	3800	223.750	223.670
	54F	3800	219.950	219.870
	53F	3800	216.150	216.070
	52F	3800	212.350	212.270
	51F	3800	208.550	208.470
	50F	3800	204.750	204.670
	49F管线层	1500	203.250	203.200
	49F（避难层）	4200	199.050	199.000
	48F	3800	195.250	195.170
	47F	3800	191.450	191.370
	46F	3800	187.650	187.570
	45F	3800	183.850	183.770
	44F设备夹层	2150	181.700	181.650
	44F（酒店大堂）	7500	174.200	174.120
公寓	43F设备夹层	2150	172.050	172.000
	43F	3600	168.450	168.400
	42F	3600	164.850	164.800
	41F	3600	161.250	161.200
	40F	3600	157.650	157.600
	39F管线层	1500	156.150	156.100
	39F（避难层）	4200	151.950	151.900
	38F	3600	148.350	148.300
	37F	3600	144.750	144.700
	36F	3600	141.150	141.100
	35F	3600	137.550	137.500
	34F	3600	133.950	133.900
	33F	3600	130.350	130.300
	32F	3600	126.750	126.700
	31F	3600	123.150	123.100
	30F	3600	119.550	119.500
	29F	3600	115.950	115.900
	28F	3600	112.350	112.300
	27F	3600	108.750	108.700
	26F管线层	1500	107.250	107.200
	26F（避难层）	4200	103.050	103.000
	25F	3600	99.450	99.400
	24F	3600	95.850	95.800
	23F	3600	92.250	92.200
	22F	3600	88.650	88.600
	21F	3600	85.050	85.000
	20F	3600	81.450	81.400
	19F	3600	77.850	77.800
	18F	3600	74.250	74.200
	17F	3600	70.650	70.600
	16F	3600	67.050	67.000
	15F	3600	63.450	63.400
	14F管线层	1500	61.950	61.900
	14F（避难层）	4200	57.750	57.700
	13F	3600	54.150	54.100
	12F	3600	50.550	50.500
	11F	3600	46.950	46.900
	10F	3600	43.350	43.300
	9F	3600	39.750	39.700
	8F	3600	36.150	36.100
	7F	3600	32.550	32.500
	6F	3600	28.950	28.900
	5F	3600	25.350	25.300
	4F（公寓大堂）	4200	21.150	21.100
裙房	3F设备夹层	2150	19.000	18.950
	3F	5500	13.500	13.450
	2F（酒店大堂）	5500	8.000	7.920
	1F（公寓、宴会大堂）	8000	0.000	-0.080
地下室	B1F（酒店后勤）	6650	-6.650	-6.750
	B2F（局部人防区）	3500	-10.150	-10.250
	B3F(整体人防区)	3600	-13.750	-14.000

本图仅供施工图审查使用

版本号	日期	修改内容	修订者
		修订栏	

图纸条码

总工程师	赵松林	
审定	黄孝颖	
审核	张林汉	
设计总负责人	黄孝颖	
专业负责人	宋延勇	
校核	石昊洋	
设计	宋延勇	

建设单位	佛山市禅城区 保宸置业有限公司
工程名称	保利天珺秀台7#
业务号	21-347 专业 建筑
设计阶段	施工图
图纸名称	十五层平面图
图号	J-1-PM12
出图日期	2023.08.02

版权所有，不得复制、套用或公开。
ALL RIGHTS RESERVED.