

会 员	建 筑	宋延勇
登 记	结 构	邓艳青
栏	给 排 水	甘兆麟
	电 气	蔡泽炯

图例

厨房排烟350x350

结构降板400

结构降板100

回填500

回填300

建筑专业说明:

(1)除特别注明外，“H”为楼层的建筑面标高，“h”为楼层的结构标高，结构标高和建筑面标高等同时标注时，标高后加（I）表示为建筑完成面标高，标高后加（G）表示为结构面标高。

(2)除特别注明外，所有的内墙厚度为200mm。

(3)除特别注明外，门框均为200mm，或门位于所在房间（或走廊）的正中。

(4)除特别注明外，各类管井、配电间、强电间、空调机房的建筑标高为h+0.05，结构标高为h。弱电间、通讯间以及其他房间、通道、门厅对应的完成面标高为当层楼面建筑标高“H”，对应的结构标高为当层楼面结构标高“h”。卫生间的完成面标高为h+0.015，结构面标高详见平面图注。

(5)水管、地漏、雨水口、排水留孔的大小及具体位置以给排水专业图纸位置。

(6)电间内的强、弱电上线并设，均设砖砌防水100（高X100）高。

(7)强电间、配电间、水管井、空调水管井、空调机房、避难楼层的加压机房及排烟机房等房间、管井设100宽C15混凝土门槛，门槛外边线内退房间墙的外边线100，比房间、管井外地面完成面高200mm，门设在门槛外侧。

(8)建筑物内防风管井外的水管井、管道井每层在楼板处按结构图集设置，待管道安装后用同样标号的混凝土封堵，电缆井的封堵做法可参照国标06D105《电缆防火阻燃设计与施工》第16页的做法。

(9)所有结构剪力墙或柱尺寸均以结构设计图为准，各设备专业预留孔洞请同时详该设备专业图纸进行施工。

(10)内墙及顶棚变化详见中南标11ZJ111(④)(⑤)；楼面平接变形缝做法详中南标图集11ZJ111(⑥)(⑦)，外墙变形缝详幕墙专业深化设计图；原顶变形缝详专业公司深化图。

(11)首层人行出入口位置室外高低15mm，以斜面过渡，由出入口位置排水沟的雨水篦子的孔洞宽度不大于15mm。

(12)除设备房、各类管井及核心筒内的楼梯间等部位外，室内其他区域需另详二次装修深化图纸。

(13)地下室一层及首层室外场地、各层阳台或露台、屋顶等室外区域需另详景观专业深化图纸。

(14)外墙幕墙、屋顶采光天窗需另详幕墙专业深化图纸。建筑幕墙应在每层楼体外沿处采取符合国家相关规范规定的防火措施，幕墙与每层楼板、隔墙处的缝隙应采用防火封堵材料封堵。

防火分区16' 17-1'

面积: 1819.96

周长: 176.18

消防控制室

物业办公室


1.2m

1.2m

图例:

	消防电梯		安全口		防火分区分界线
	楼梯间		安全口(门)		疏散距离

楼型	防火分区	防火分区面积	功能	各功能用房使用面积	使用人数计算方式	使用人数	所需灭火器数量	实际配置灭火器数量	
十六~十七层	防火分区16-17-1	1819.96	服务用房公寓	176.18	每户2人	42	4	4	
			其他辅助						
			合计			33.75			
			合计			1819.96		42	4

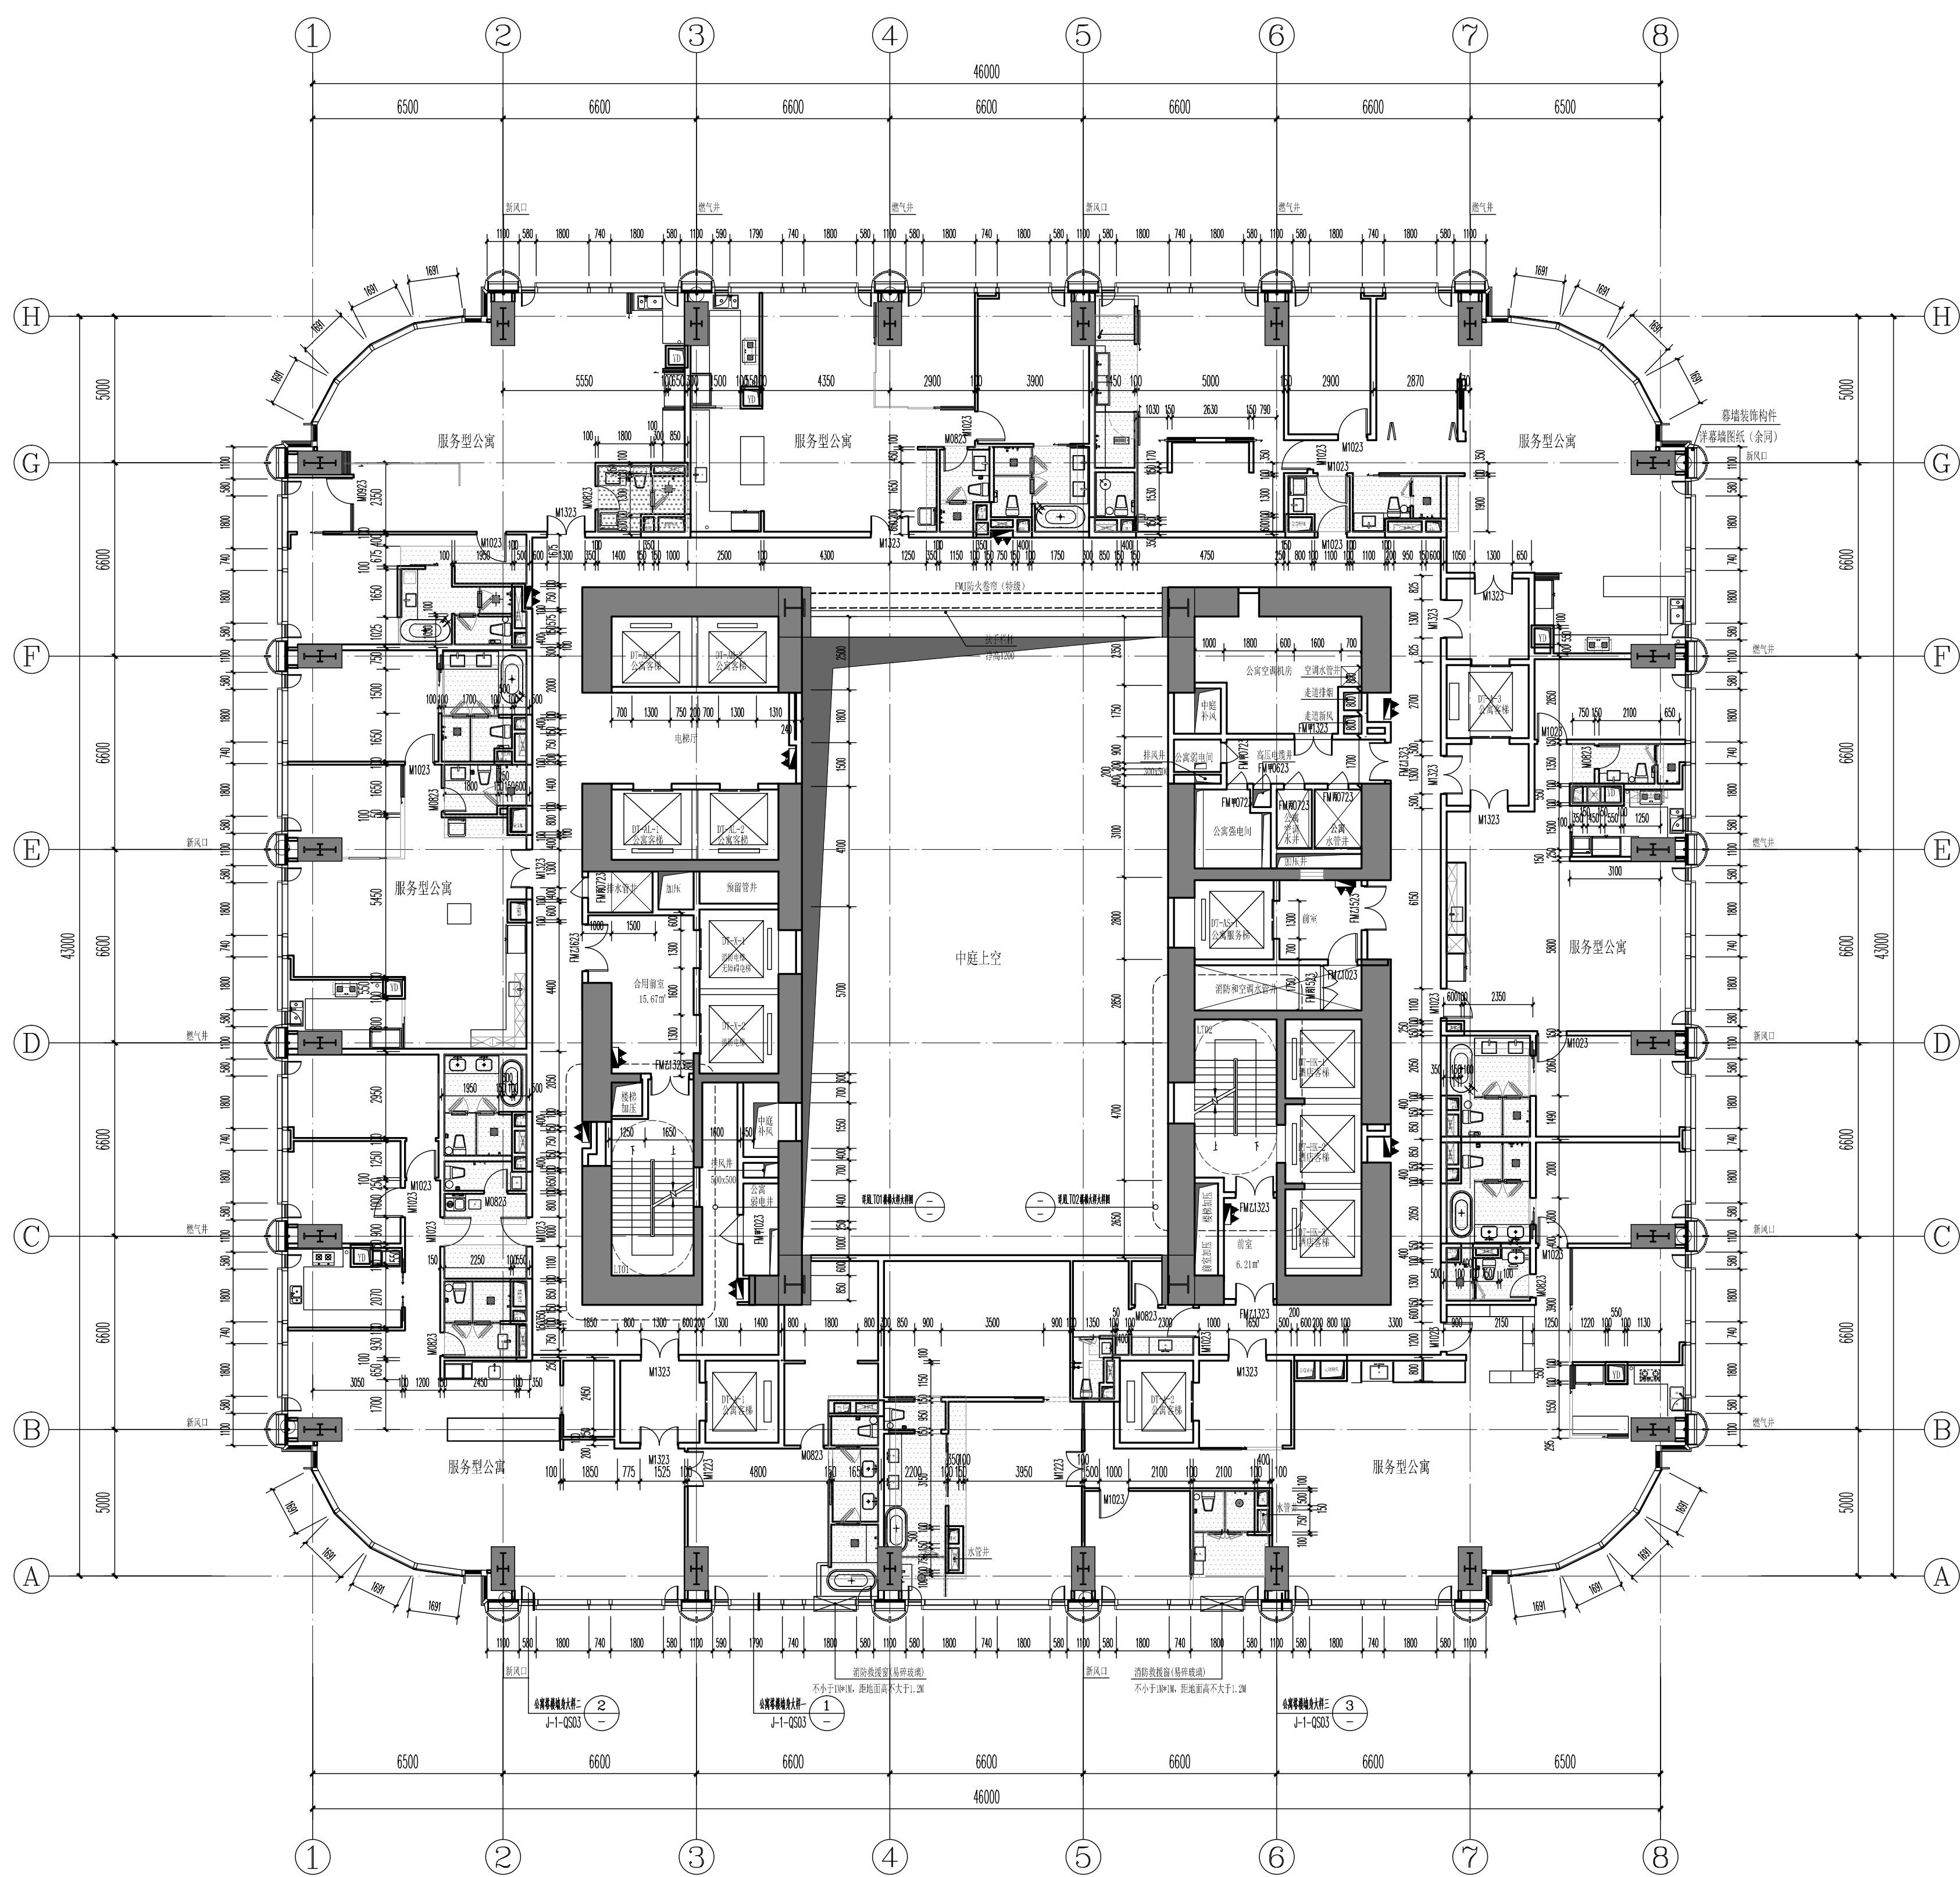

十六~十七层平面图 1:150

北				广州市设计院集团有限公司 GUANGZHOU DESIGN INSTITUTE GROUP CO., LTD. 工程设计甲级资质证书编号：A244007378 工程勘察甲级资质证书编号：B244007378			
佛山保利天珺7#楼层高表				平面位置示意 Key Plan			
楼层		层高 (m)	建筑标高 (J) H	结构标高 (G) h			
屋面	屋面层		246.300	246.000			
酒店	58F	6000	240.000	239.920			
	57F设备夹层	2150	237.850	237.800			
	57F	6000	231.850	231.800			
	56F	4300	227.550	227.470			
	55F	3800	223.750	223.670			
	54F	3800	219.950	219.870			
	53F	3800	216.150	216.070			
	52F	3800	212.350	212.270			
	51F	3800	208.550	208.470			
	50F	3800	204.750	204.670			
	49F管线层	1500	203.250	203.200			
	49F (避难层)	4200	199.050	199.000			
	48F	3800	195.250	195.170			
	47F	3800	191.450	191.370			
	46F	3800	187.650	187.570			
	45F	3800	183.850	183.770			
	44F设备夹层	2150	181.700	181.650			
	44F (酒店大堂)	7500	174.200	174.120			
	43F设备夹层	2150	172.050	172.000			
	43F	3600	168.450	168.400			
	42F	3600	164.650	164.600			
	41F	3600	161.250	161.200			
	40F	3600	157.650	157.600			
	39F管线层	1500	156.150	156.100			
	39F (避难层)	4200	151.950	151.900			
	38F	3600	148.350	148.300			
	37F	3600	144.750	144.700			
	36F	3600	141.150	141.100			
	35F	3600	137.550	137.500			
	34F	3600	133.950	133.900			
	33F	3600	130.350	130.300			
	32F	3600	126.750	126.700			
	31F	3600	123.150	123.100			
	30F	3600	119.550	119.500			
	29F	3600	115.950	115.900			
	28F	3600	112.350	112.300			
27F	3600	108.750	108.700				
26F管线层	1500	107.250	107.200				
26F (避难层)	4200	103.050	103.000				
25F	3600	99.450	99.400				
24F	3600	95.850	95.800				
23F	3600	92.250	92.200				
22F	3600	88.650	88.600				
21F	3600	85.050	85.000				
20F	3600	81.450	81.400				
19F	3600	77.850	77.800				
18F	3600	74.250	74.200				
17F	3600	70.650	70.600				
16F	3600	67.050	67.000				
15F	3600	63.450	63.400				
14F管线层	1500	61.950	61.900				
14F (避难层)	4200	57.750	57.700				
13F	3600	54.150	54.100				
12F	3600	50.550	50.500				
11F	3600	46.950	46.900				
10F	3600	43.350	43.300				
9F	3600	39.750	39.700				
8F	3600	36.150	36.100				
7F	3600	32.550	32.500				
6F	3600	28.950	28.900				
5F	3600	25.350	25.300				
4F (公寓大堂)	4200	21.150	21.100				
3F设备夹层	2150	19.000	18.950				
3F	5500	13.500	13.450				
2F (酒店大堂)	5500	8.000	7.920				
裙房	1F (公寓、宴会大堂)	8000	0.000	-0.080			
	81F (酒店后勤)	6650	-6.650	-6.750			
	82F (局部人防区)	3500	-10.150	-10.250			
	83F (整体人防区)	3300	-13.750	-14.000			
地下室							