

会 建	筑	宋延勇
登 结	构	邓艳青
栏 给	水	甘兆麟
	电 气	蔡泽炯

图例:

厨房烟道350x350

结构降板400

结构降板100

回填500

回填300

建筑专业说明:

(1) 除特别注明外,“H”为楼层的建筑面标高,“h”为楼层的结构标高,结构标高和建筑面标高同时标注时,标高后加(1)表示为建筑完成面标高,标高后加(G)表示为结构面标高。

(2) 除特别注明外,所有的内墙厚度为200mm。

(3) 除特别注明外,门框均为200mm,或门位于所在房间(或走廊)的正中。

(4) 除特别注明外,各类管井、配电间、强电间、空调机房的建筑标高为h+0.05,结构标高为h。弱电间、通讯间以及其他房间、通道、门厅对应的完成面标高为当楼层面建筑标高“H”,对应的结构标高为当楼层面结构标高“h”。卫生间的完成面标高为h+0.015,结构面标高详见平面图注。

(5) 水管、地漏、雨水口、排水立管的大小及具体位置以给排水专业图纸位置。

(6) 电间内的强、弱电上线井处,均设砖砌防水100(宽)X100(高)。

(7) 强电间、配电间、水管井、空调水管井、空调机房、避难楼层的加压机房及排烟机房等房间、管井设100宽C15混凝土门框,门框外边线内退房间墙的外边线100,比房间、管井外地面完成面高200mm,门设在门框外框。

(8) 建筑物内除风管井外的水管井、管道井每层在楼板处按结构图集设隔扇,待管道安装后用同样标号的混凝土封堵,电缆井的封堵做法可参照国标GB50105《电缆防火阻燃设计与施工》第16页的做法。

(9) 所有结构剪力墙或柱尺寸均以结构施工图为准,各设备专业预留孔洞请同时详该设备专业图纸进行施工。

(10) 内墙及顶棚变形缝详见中南标11ZJ111(图例);楼面平接处变形缝做法详中南标图集11ZJ111(图例);外墙变形缝详幕墙专业深化设计图;原顶棚变形缝详专业专业深化图。

(11) 首层人行出入口位置室外高15mm,以斜面过渡;出入口位置排水沟的雨水篦子的孔洞宽度不大于15mm

(12) 设施设备房、各类管井及核心区域内的楼梯间等部位外,室内其他区域再另详二次装修深化图纸。


(13) 地下室一层及首层室外地库、各层门台或露台、屋顶等室外区域需另详景观专业深化图纸。

区域内外墙幕墙、顶棚采用天窗需另详幕墙专业深化图纸。建筑幕墙应在每层楼板外沿处采取符合国家相关规范规定的防火措施,幕墙与每层楼板、隔墙处的缝隙应采用防火封堵材料封堵。

防火分区说明

各层均设置自动喷水灭火系统和自动报警系统

楼层	防火分区		面积	疏散人数	疏散宽度	疏散距离
	防火分区	防火分区				
二十七层	防火分区 27-1	防火分区 27-2	1819.36	1765.58	33.29	42
			合计	1819.36	33.29	42

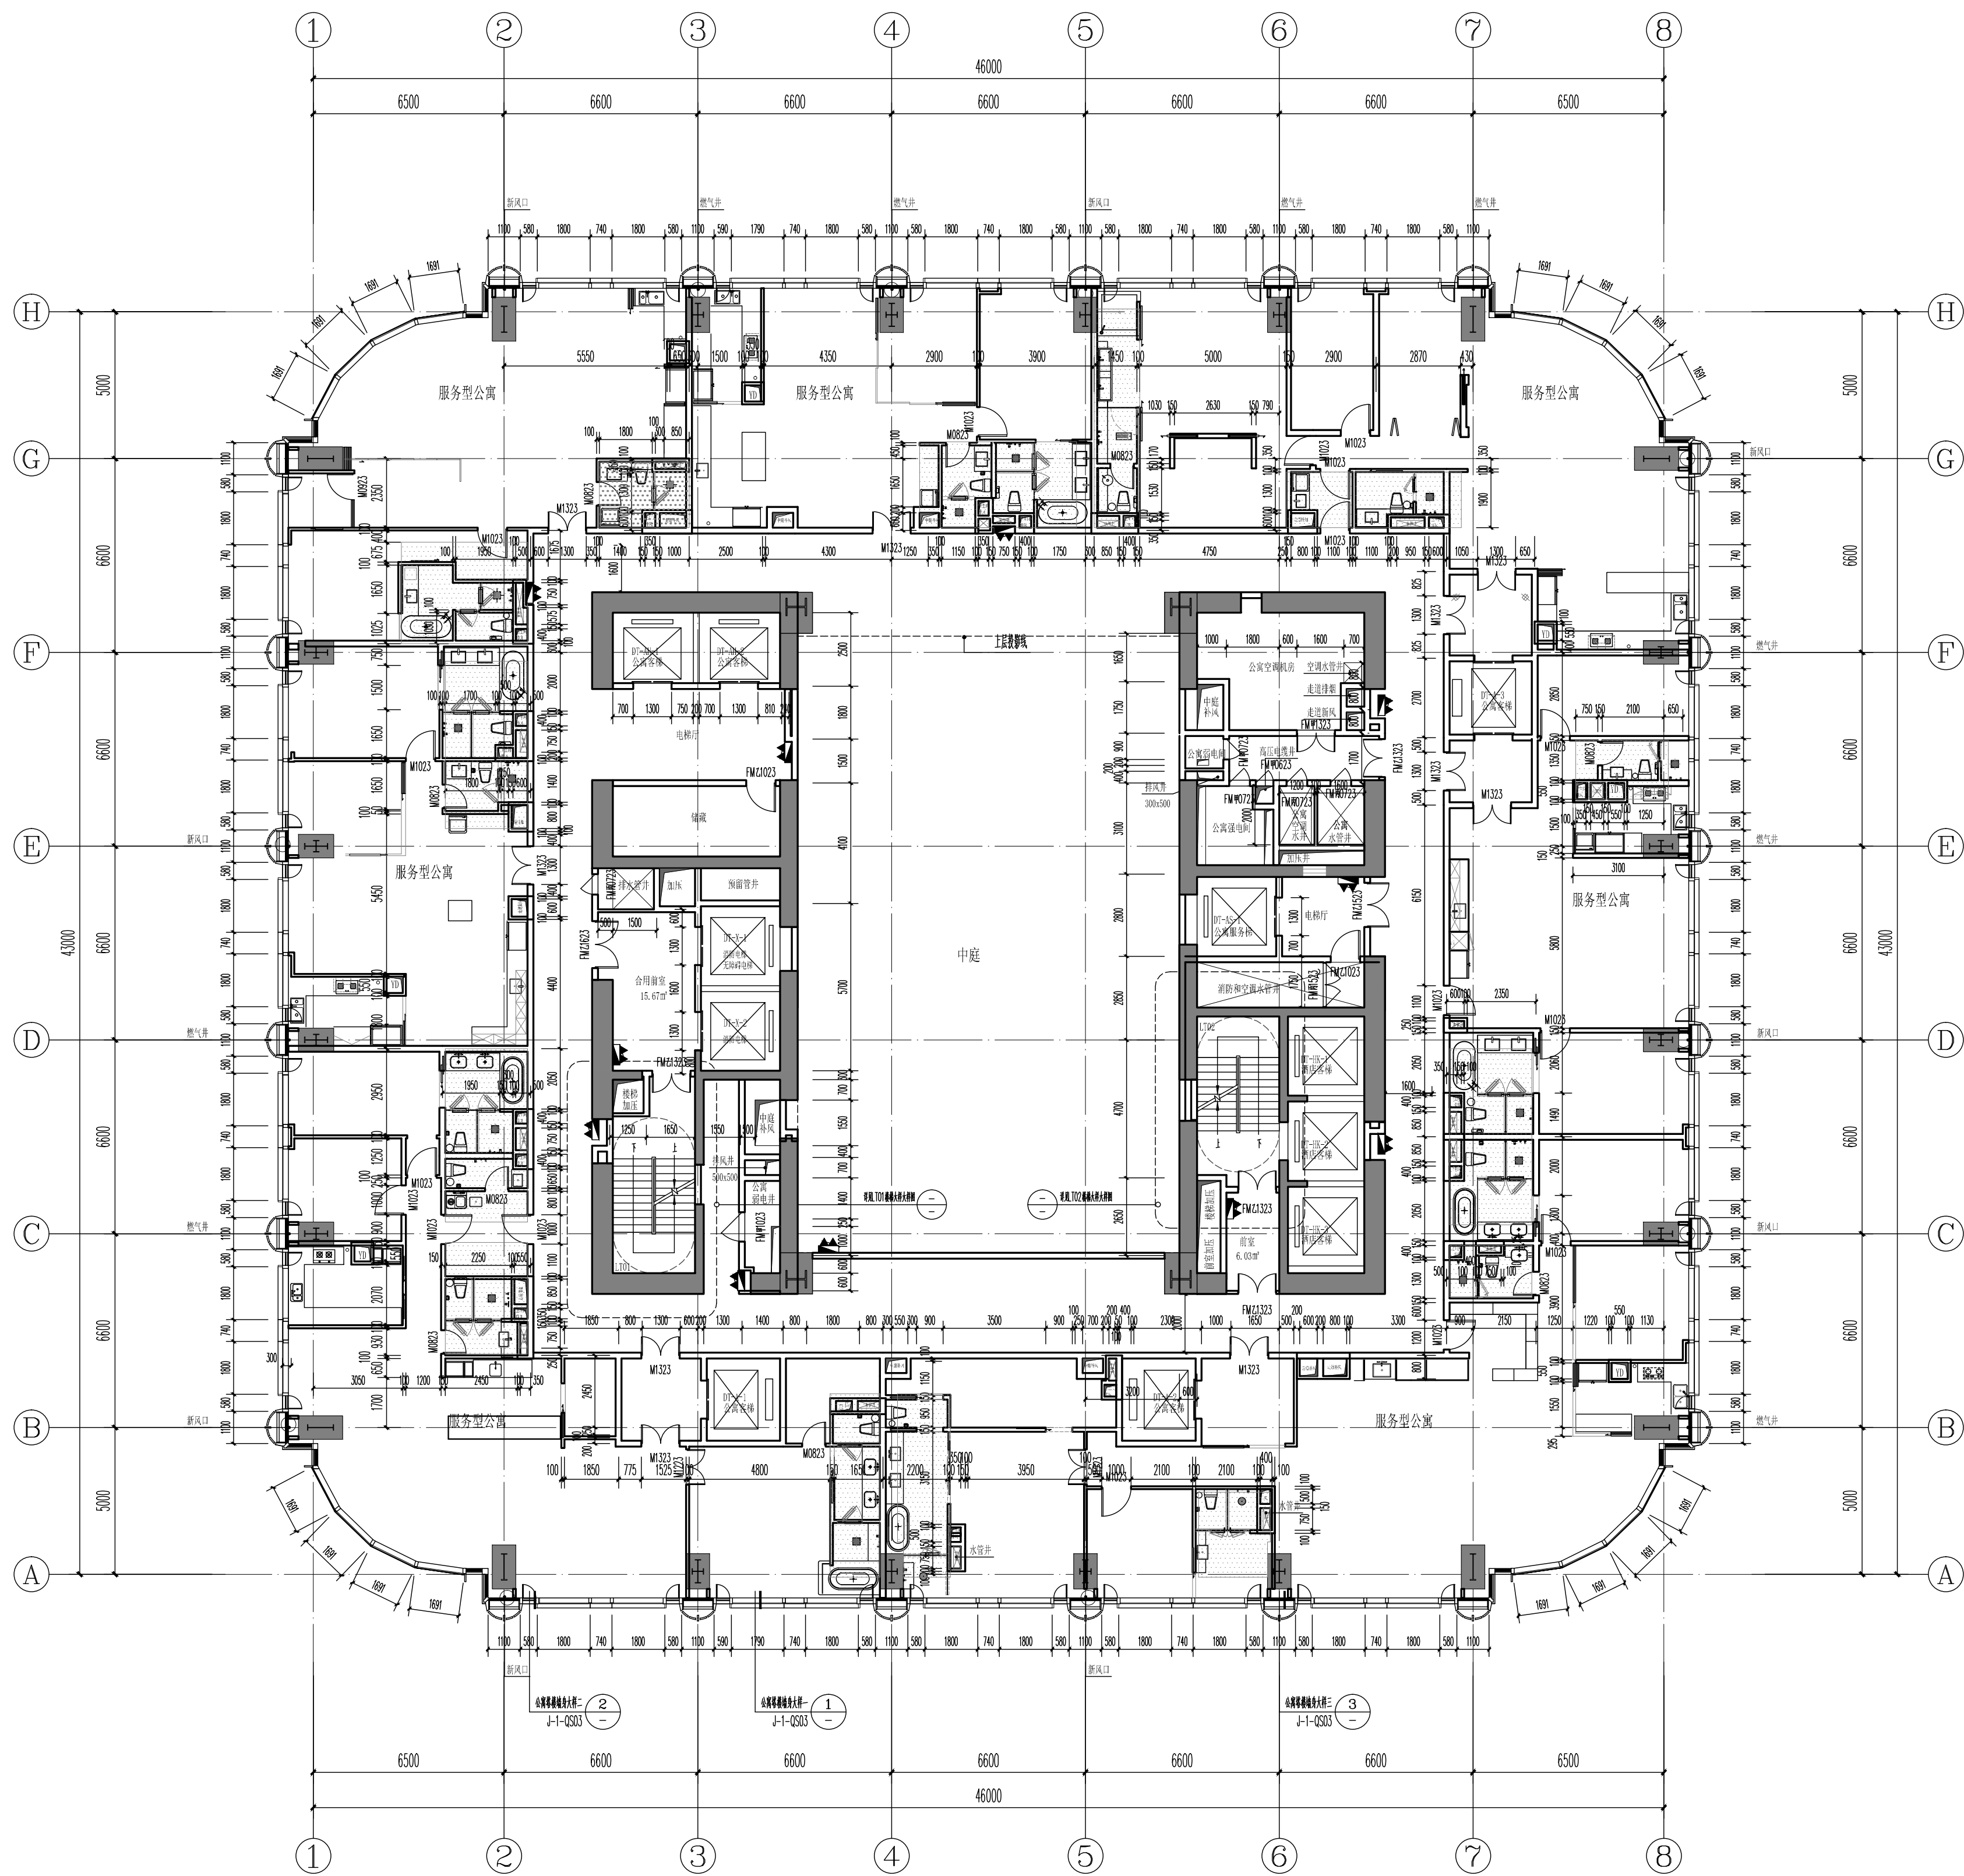

二十七层平面图 1:150

北				广州市设计院集团有限公司 GUANGZHOU DESIGN INSTITUTE GROUP CO., LTD. 工程设计甲级资质证书编号：A240007378 工程勘察甲级资质证书编号：B240007378			
佛山保利天珺7#楼层高表				平面位置示意 Key Plan			
		楼层	层高 (m)	建筑标高 (J) H	结构标高 (G) h		
屋面		屋面设备层					
		屋面层		246.300	246.000		
酒店		58F	6000	240.000	238.920		
		57F设备夹层	2150	237.850	237.800		
		57F	6000	231.850	231.800		
		56F	4300	227.550	227.470		
		55F	3800	223.750	223.670		
		54F	3800	219.950	219.870		
		53F	3800	216.150	216.070		
		52F	3800	212.350	212.270		
		51F	3800	208.550	208.470		
		50F	3800	204.750	204.670		
		49F管线层	1500	203.250	203.200		
		49F (避难层)	4200	199.050	199.000		
		48F	3800	195.250	195.170		
		47F	3800	191.450	191.370		
		46F	3800	187.650	187.570		
		45F	3800	183.850	183.770		
酒店		44F设备夹层	2150	181.700	181.650		
		44F (酒店大堂)	7500	174.300	174.120		
		43F设备夹层	2150	172.050	172.000		
		43F	3600	168.450	168.400		
		42F	3600	164.650	164.600		
		41F	3600	161.250	161.200		
		40F	3600	157.650	157.600		
		39F管线层	1500	156.150	156.100		
		39F (避难层)	4200	151.950	151.900		
		38F	3600	148.350	148.300		
		37F	3600	144.750	144.700		
		36F	3600	141.150	141.100		
		35F	3600	137.550	137.500		
		34F	3600	133.950	133.900		
		33F	3600	130.350	130.300		
		32F	3600	126.750	126.700		
公寓		31F	3600	123.150	123.100		
		30F	3600	119.550	119.500		
		29F	3600	115.950	115.900		
		28F	3600	112.350	112.300		
		27F	3600	108.750	108.700		
		26F管线层	1500	107.250	107.200		
		26F (避难层)	4200	103.050	103.000		
		25F	3600	99.450	99.400		
		24F	3600	95.850	95.800		
		23F	3600	92.250	92.200		
		22F	3600	88.650	88.600		
		21F	3600	85.050	85.000		
		20F	3600	81.450	81.400		
		19F	3600	77.850	77.800		
		18F	3600	74.250	74.200		
		17F	3600	70.650	70.600		
公寓		16F	3600	67.050	67.000		
		15F	3600	63.450	63.400		
		14F管线层	1500	61.950	61.900		
		14F (避难层)	4200	57.750	57.700		
		13F	3600	54.150	54.100		
		12F	3600	50.550	50.500		
		11F	3600	46.950	46.900		
		10F	3600	43.350	43.300		
		9F	3600	39.750	39.700		
		8F	3600	36.150	36.100		
		7F	3600	32.550	32.500		
		6F	3600	28.950	28.900		
		5F	3600	25.350	25.300		
		4F (公寓大堂)	4200	21.150	21.100		
		3F设备夹层	2150	19.000	18.950		
		3F	5500	13.500	13.450		
裙房		2F (酒店大堂)	5500	8.000	7.920		
		1F (公寓、宴会大堂)	8000	0.000	-0.080		
		B1F (酒店后勤)	6650	-6.650	-6.750		
地下室		B2F (局部人防区)	3500	-10.150	-10.250		
		B3F (整体人防区)	3600	-13.750	-14.000		
				图 纸 条 码			
				总 工 程 师 赵松林			
				审 定 黄孝颖			
				审 核 张林汉			
				设 计 黄孝颖			
				总 负 责 人 宋延勇			
				专 业 负 责 人 石昊洋			
				校 核 宋延勇			
				设 计 宋延勇			
建设单位				佛山市禅城区 保宸置业有限公司			
工程名称				保利天珺秀台7#			
业务号				21-347		专业	建筑
设计阶段				施工图			
图纸名称				二十七层 平面图			
图号				J-1-PM16		版本号	
出图日期				2023. 08. 02		序号	
				版权所有，不得复制、套用或公开。 ALL RIGHTS RESERVED.			