

会 员	建 筑	宋延勇
登 记	结 构	邓艳青
栏	给 排 水	甘兆麟
	电 气	蔡泽炯

图例

	厨房烟道350x350
	结构降板400
	结构降板100
	回填500
	回填300

建筑专业说明:

- (1) 除特别注明外，“H”为楼层的建筑面标高，“h”为楼层的结构标高，结构标高和建筑面标同时标注时，标高后加（I）表示为建筑完成面标高，标高后加（G）表示为结构面标高。
- (2) 除特别注明外，所有的内墙厚度均为200mm。
- (3) 除特别注明外，门底均为200mm，或门位于所在房间(或走廊)的正中。
- (4) 除特别注明外，各类管井、配电间、强电间、空调机房的建筑标高为h+0.05，结构标高为h。弱电间、通讯间以及其他房间、通道、门厅对应的完成面标高为当层楼面建筑标高“H”，对应的结构标高为当层楼面结构标高“h”。卫生间的完成面标高为h+0.015，结构面标高详见平面图注。
- (5) 水管、地漏、雨水口、排水留孔的大小及具体位置以给排水专业图纸位置。
- (6) 电间内的强、弱电上线并设，均设砖砌防水100（宽X100高）。
- (7) 强电间、配电间、水管井、空调水管井、空调机房、避难楼层的加压机房及排烟机房等房间、管井设100宽C15混凝土门槛，门槛外边线内退房间墙的外边线100，比房间、管井外地面完成面高200mm，门设在门槛外框。
- (8) 建筑物内防风管井外的水管井、管道井每层在楼板处按结构图集设隔，待管道安装后用同样标号的混凝土封堵，电缆井的封堵做法可参照国标06D105《电缆防火阻燃设计与施工》第16页的做法。
- (9) 所有结构剪力墙或柱尺寸均以结构施工图为准，各设备专业预留孔洞请同时详该设备专业图纸进行施工。
- (10) 内墙及顶棚变形缝详见中南标11ZJ111④⑤⑥；楼面平接处变形缝做法详中南标图集11ZJ111⑦⑧⑨；外墙变形缝详幕墙专业深化设计图；原屋盖变形缝详专业公司深化图。
- (11) 首层人行出入口位置室外内外高差15mm，以斜面过渡，由入口处设置排水沟的雨水篦子的孔洞宽度不大于15mm。
- (12) 除设备房、各类管井及核心筒内的楼梯间等部位外，室内其他区域需另二次装修深化图纸。
- (13) 地下室一层及首层室外场地、各层阳台或露台、屋顶等室外区域需另详景观专业深化图纸。
- (14) 外墙幕墙、屋顶采光天窗需另详幕墙专业深化图纸。建筑幕墙应在每层楼体外沿处采取符合国家相关规范规定的防火措施，幕墙与每层楼板、隔墙处的缝隙应采用防火封堵材料封堵。

防火分区说明

防火分区28'34-1
面积: 1819.36
功能: 服务式公寓


1.2M

1.2M

图例:

图例:	消防电梯	安全口	防火分区界线

楼型	防火分区	防火分区名称	功能	各楼栋单元使用面积	住宅人数计算方式	使用人数	耐火等级或耐火极限	实际疏散距离符合性
二十八~三十层	梯架区	1819.36	服务式公寓	1783.58	每户2人	42	0.12	
			其他辅助	33.75				
			合计	1818.36		42	0.12	合格

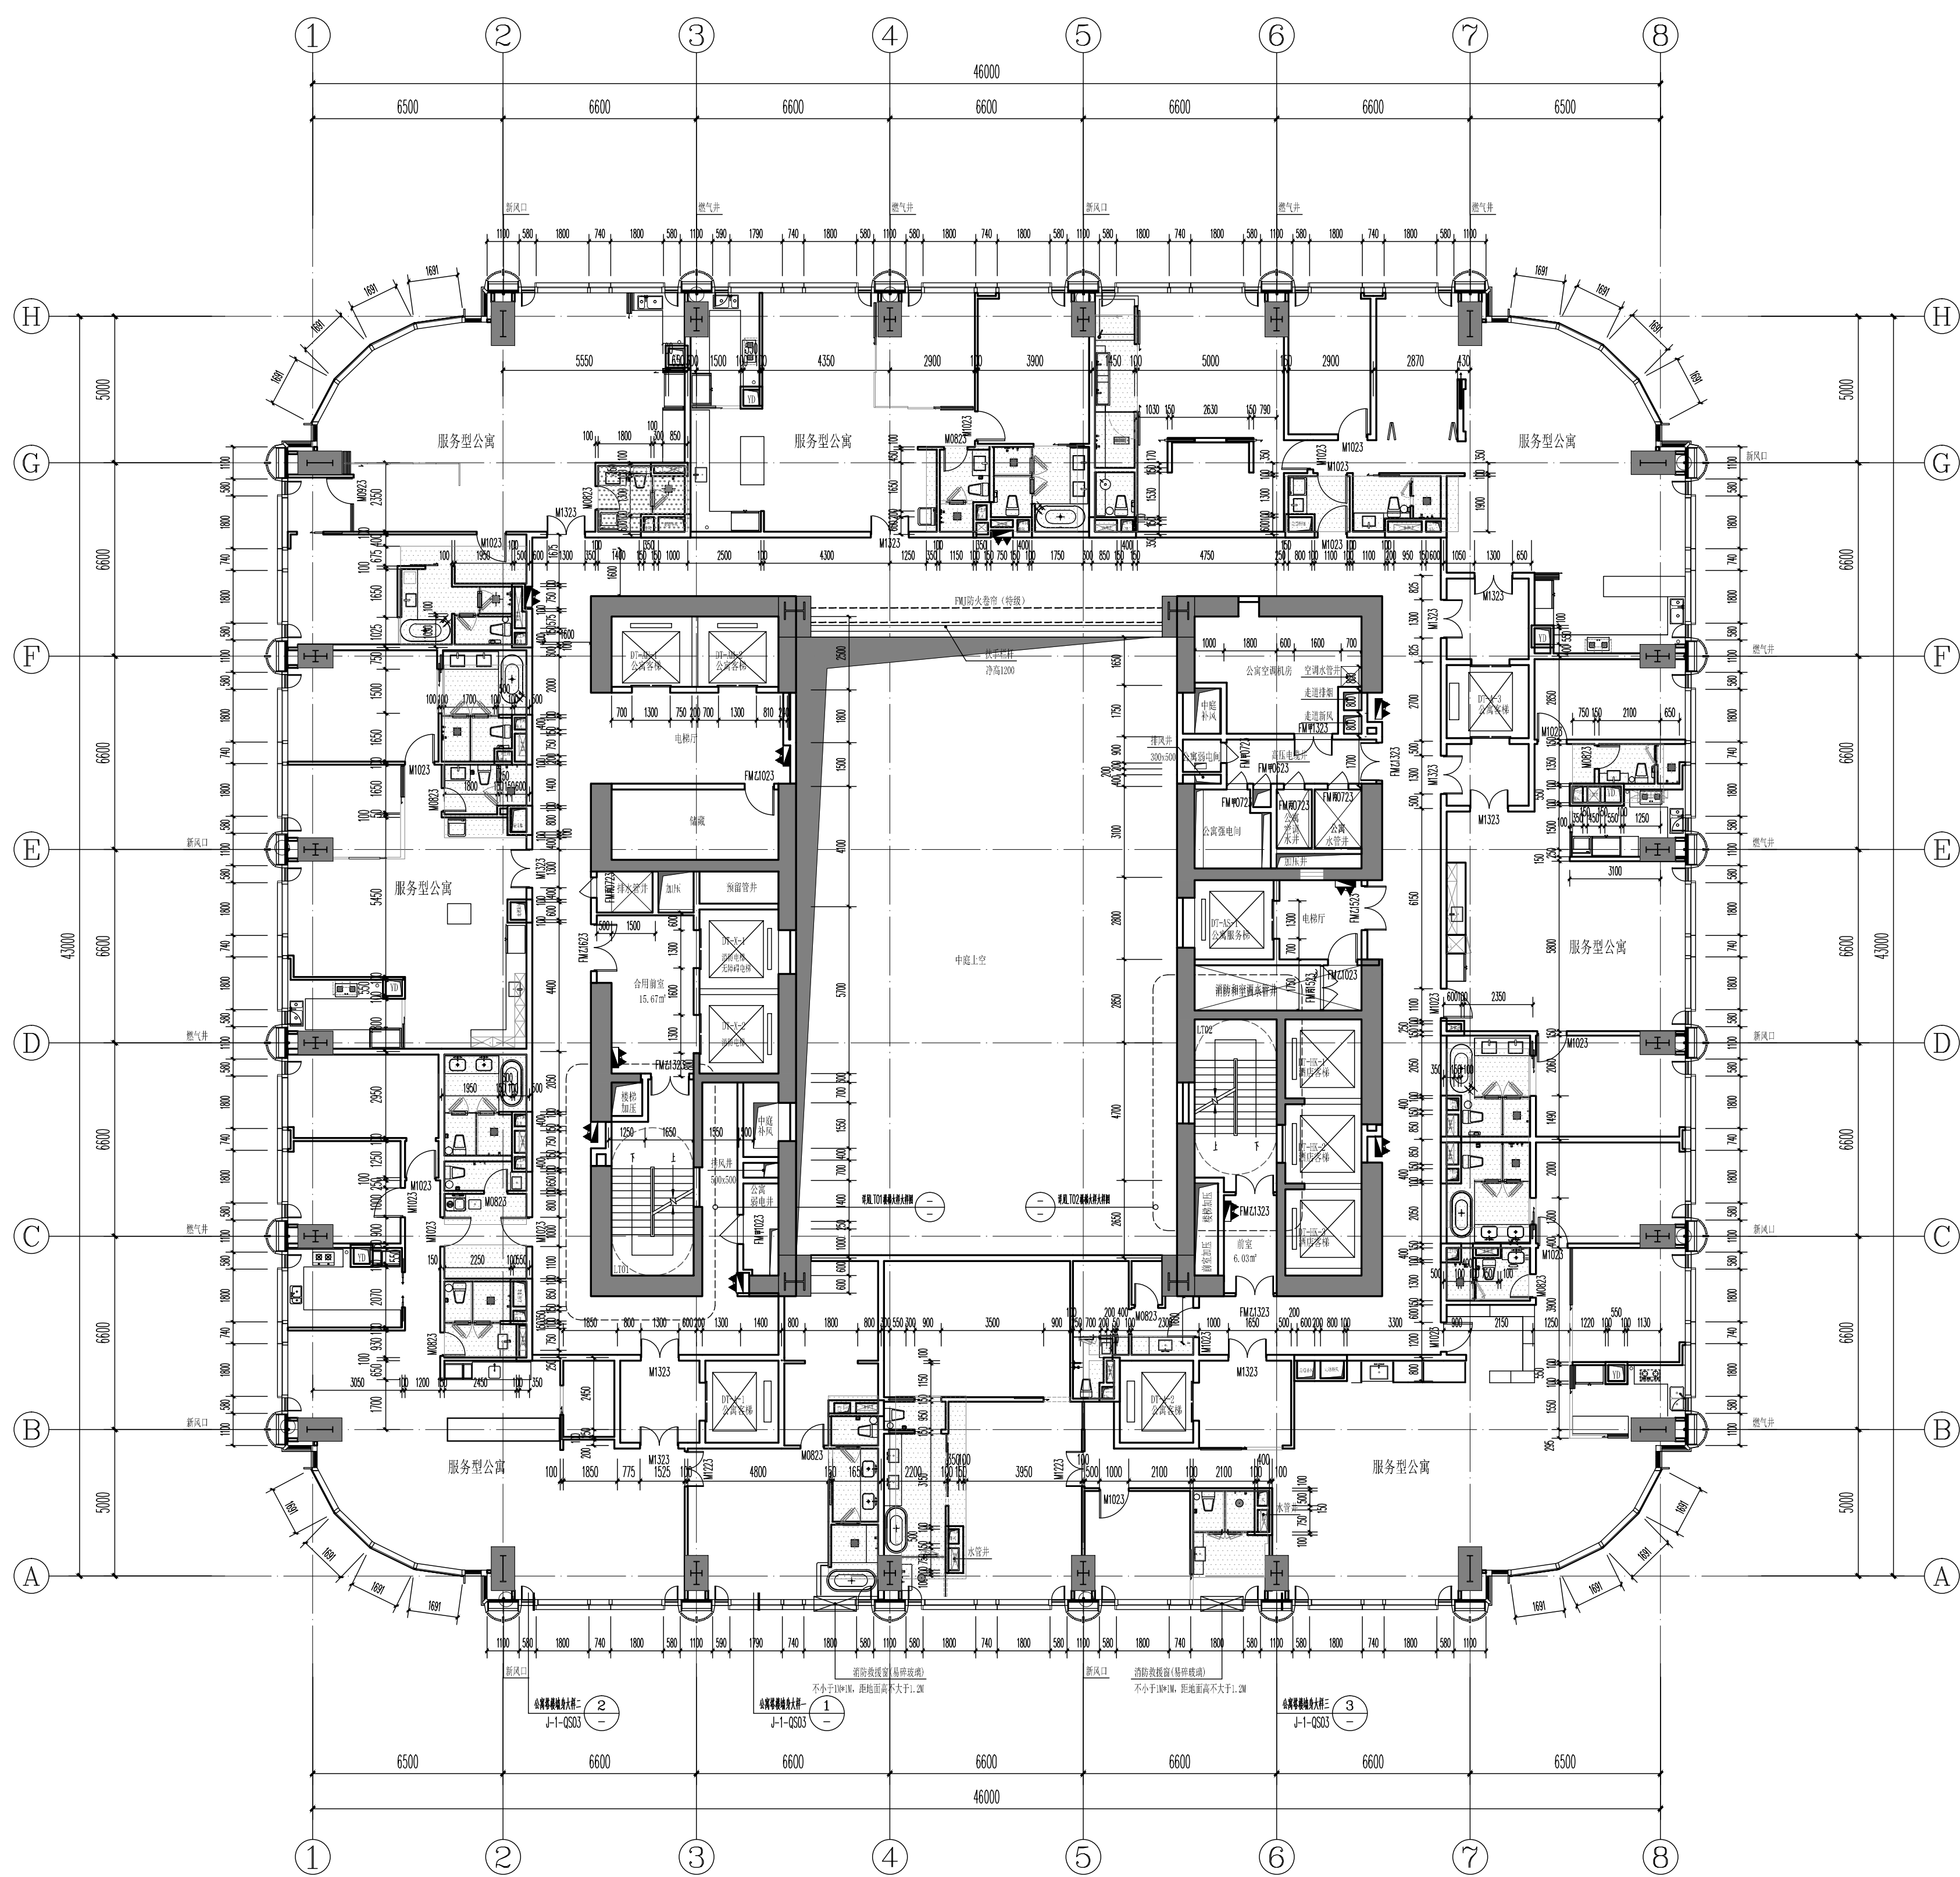

二十八~三十四层平面图 1:150

北				广州市设计院集团有限公司 GUANGZHOU DESIGN INSTITUTE GROUP CO., LTD. 工程设计甲级资质证书编号：A240007378 工程勘察甲级资质证书编号：B240007378	
佛山保利天珺7#楼层高表					
		楼层	层高 (m)	建筑标高 (J) H	结构标高 (G) h
屋面		屋面层		246.300	246.000
酒店	58F	6000	240.000	239.920	
	57F设备夹层	2150	237.850	237.800	
	57F	6000	231.850	231.800	
	56F	4300	227.550	227.470	
	55F	3800	223.750	223.670	
	54F	3800	219.950	219.870	
	53F	3800	216.150	216.070	
	52F	3800	212.350	212.270	
	51F	3800	208.550	208.470	
	50F	3800	204.750	204.670	
	49F管线层	1500	203.250	203.200	
	49F(避难层)	4200	199.050	199.000	
	48F	3800	195.250	195.170	
	47F	3800	191.450	191.370	
	46F	3800	187.650	187.570	
	45F	3800	183.850	183.770	
	44F设备夹层	2150	181.700	181.650	
	44F(酒店大堂)	7500	174.200	174.120	
	43F设备夹层	2150	172.050	172.000	
	43F	3600	168.450	168.400	
	42F	3600	164.650	164.600	
	41F	3600	161.250	161.200	
	40F	3600	157.650	157.600	
	39F管线层	1500	156.150	156.100	
	39F(避难层)	4200	151.950	151.900	
	38F	3600	148.350	148.300	
	37F	3600	144.750	144.700	
	36F	3600	141.150	141.100	
	35F	3600	137.550	137.500	
	34F	3600	133.950	133.900	
	33F	3600	130.350	130.300	
	32F	3600	126.750	126.700	
	31F	3600	123.150	123.100	
	30F	3600	119.550	119.500	
	29F	3600	115.950	115.900	
	28F	3600	112.350	112.300	
	27F	3600	108.750	108.700	
	26F管线层	1500	107.250	107.200	
	26F(避难层)	4200	103.050	103.000	
25F	3600	99.450	99.400		
24F	3600	95.850	95.800		
23F	3600	92.250	92.200		
22F	3600	88.650	88.600		
21F	3600	85.050	85.000		
20F	3600	81.450	81.400		
19F	3600	77.850	77.800		
18F	3600	74.250	74.200		
17F	3600	70.650	70.600		
16F	3600	67.050	67.000		
15F	3600	63.450	63.400		
14F管线层	1500	61.950	61.900		
14F(避难层)	4200	57.750	57.700		
13F	3600	54.150	54.100		
12F	3600	50.550	50.500		
11F	3600	46.950	46.900		
10F	3600	43.350	43.300		
9F	3600	39.750	39.700		
8F	3600	36.150	36.100		
7F	3600	32.550	32.500		
6F	3600	28.950	28.900		
5F	3600	25.350	25.300		
公寓	4F(公寓大堂)	4200	21.150	21.100	
	3F设备夹层	2150	19.000	18.950	
	3F	5500	13.500	13.450	
	2F(酒店大堂)	5500	8.000	7.920	
裙房	1F(公寓、宴会大堂)	8000	0.000	-0.080	
	B1F(酒店后勤)	6650	-6.650	-6.750	
	B2F(局部人防区)	3500	-10.150	-10.250	
地下室	B3F(整体人防区)	3600	-13.750	-14.000	

平面位置示意 Key Plan			