

会 员	建 筑	宋延勇
登 记	结 构	邓艳青
栏	给 排 水	甘兆麟
	电 气	蔡泽炯

图例

厨房烟道350x350

结构降板400

结构降板100

回填500

回填300

建筑专业说明:

(1) 除特别注明外,“H”为楼层的建筑面标高,“h”为结构的标高,结构标高和建筑面标高同时标注时,标高后加(1)表示为建筑完成面标高,标高后加(G)表示为结构面标高。

(2) 除特别注明外,所有的内墙墙厚为200mm。

(3) 除特别注明外,门底均为200mm,或门位于所在房间(或走廊)的正中。

(4) 除特别注明外,各类管井、配电间、强电间、空调机房的建筑标高为h+0.05,结构标高为h,弱电间、通讯间以及其他房间、通道、门厅对应的完成面标高为当层楼面建筑标高“H”,对应的结构标高为当层楼面结构标高“h”,卫生间的完成面标高为h+0.015,结构面标高详见平面图注。

(5) 水管、地漏、雨水口、排水留孔的大小及具体位置以给排水专业图纸位置。

(6) 电间内的强、弱电上线并边,均设砖砌防水100(宽)X100(高)。

(7) 强电间、配电间、水管井、空调水管、空调机房、避难楼层的加压机房及排烟机房等房间、管井设100宽C15混凝土门槛,门槛外边线内退房间的外边线100,比房间、管井外地面完成面高200mm,门设在门槛外侧。

(8) 建筑物内除风管井外的水管井、管道井每层在楼板处按结构设刚性圈,待管道安装后用同样标号的混凝土封堵,电缆井的封堵做法可参照国标GB50105《电缆防火阻燃设计与施工》第16页的做法。

(9) 所有结构剪力墙或柱尺寸均以结构施工图为准,各设备专业预留孔洞请同时详该设备专业图纸进行施工。

(10) 内墙及顶棚变化详见中南北11ZJ111(④④);楼面平接变形缝做法详中南北图集11ZJ111(④④);外墙变形缝详幕墙专业深化设计图;原顶棚变形缝详专业深化图。

(11) 首层人行出入口位置室外高差15mm,以斜面过渡,由出入口位置排水沟的雨水篦子的孔洞宽度不大于15mm

(12) 除设备房、各类管井及核心筒内的楼梯间等部位外,室内其他区域需另详二次装修深化图纸。


(13) 地下室一层及首层室外场地、各层阳台或露台、屋顶等室外区域需另详景观专业深化图纸。

(14) 外墙幕墙、屋顶采光天窗需另详幕墙专业深化图纸。建筑幕墙应在每层楼板外沿处采取符合国家相关规范规定的防火措施,幕墙与每层楼板、隔墙处的缝应应用防火封堵材料封堵。

防火分区说明

各层均设置自动喷水灭火系统和自动报警系统

楼型	防火分区	防火分区名称	功能	各疏散楼梯使用面积		使用人数	所需避难室数量或面积		实际避难室数量或面积
				单元型公寓	其他公寓		单元型公寓	其他公寓	
住宅一/四十三层	防火分区43-1	1819.96	单元型公寓	1786.19	每户3.2人	42	0	42	
			其他公寓	33.75					
			合计	1820.00		42	0	42	0

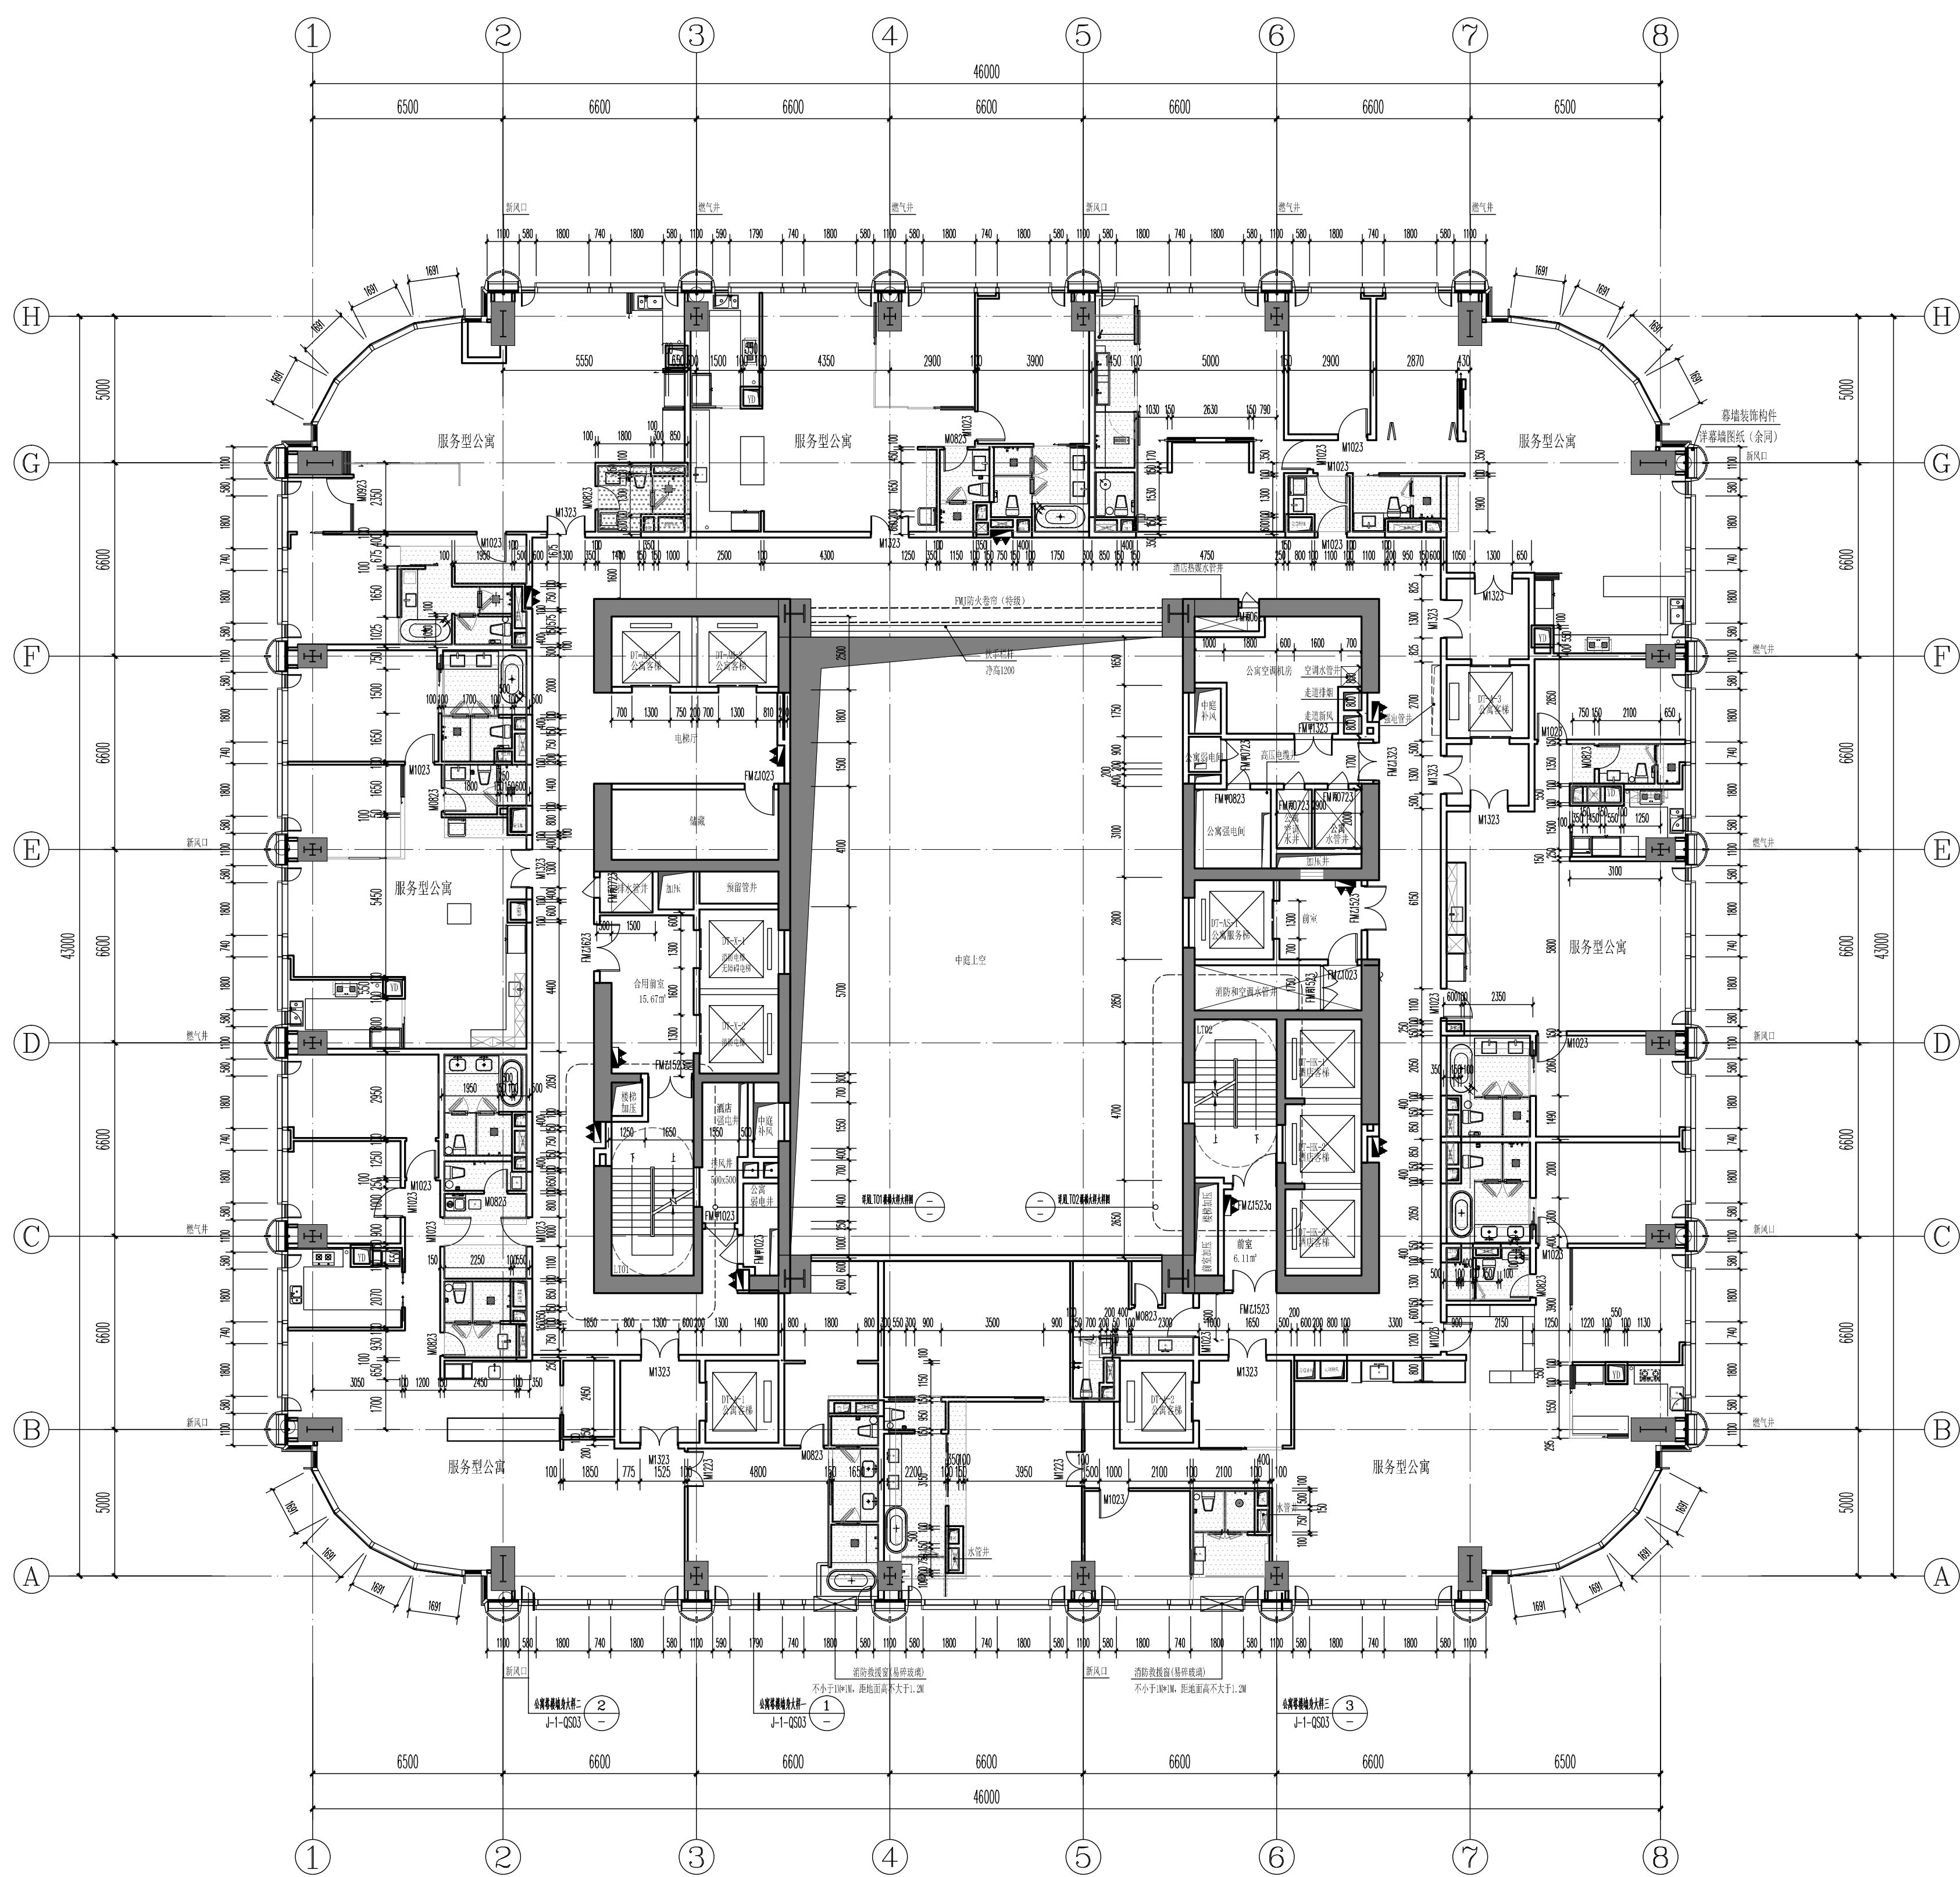

四十一~四十三层层平面图 1:150

北				广州市设计院集团有限公司 GUANGZHOU DESIGN INSTITUTE GROUP CO., LTD. 工程设计甲级资质证书编号：A244007378 工程勘察甲级资质证书编号：B244007378		
佛山保利天珺7#楼层高表				平面位置示意 Key Plan		
		楼层	层高 (m)	建筑标高 (J) H	结构标高 (G) h	
屋面		屋面层		246.300	246.000	
		58F	6000	240.000	239.920	
		57F设备夹层	2150	237.850	237.800	
		57F	6000	231.850	231.800	
		56F	4300	227.550	227.470	
		55F	3800	223.750	223.670	
		54F	3800	219.950	219.870	
		53F	3800	216.150	216.070	
		52F	3800	212.350	212.270	
		51F	3800	208.550	208.470	
		50F	3800	204.750	204.670	
		49F管线层	1500	203.250	203.200	
		49F (避难层)	4200	199.050	199.000	
		48F	3800	195.250	195.170	
		47F	3800	191.450	191.370	
		46F	3800	187.650	187.570	
		45F	3800	183.850	183.770	
		44F设备夹层	2150	181.700	181.650	
		酒店	44F (酒店大堂)	7500	174.200	174.120
		43F设备夹层	2150	172.050	172.000	
		43F	3600	168.450	168.400	
42F	3600	164.850	164.800			
41F	3600	161.250	161.200			
40F	3600	157.650	157.600			
39F管线层	1500	156.150	156.100			
39F (避难层)	4200	151.950	151.900			
38F	3600	148.350	148.300			
37F	3600	144.750	144.700			
36F	3600	141.150	141.100			
35F	3600	137.550	137.500			
34F	3600	133.950	133.900			
33F	3600	130.350	130.300			
32F	3600	126.750	126.700			
31F	3600	123.150	123.100			
30F	3600	119.550	119.500			
29F	3600	115.950	115.900			
28F	3600	112.350	112.300			
27F	3600	108.750	108.700			
26F管线层	1500	107.250	107.200			
26F (避难层)	4200	103.050	103.000			
25F	3600	99.450	99.400			
24F	3600	95.850	95.800			
23F	3600	92.250	92.200			
22F	3600	88.650	88.600			
21F	3600	85.050	85.000			
20F	3600	81.450	81.400			
19F	3600	77.850	77.800			
18F	3600	74.250	74.200			
17F	3600	70.650	70.600			
16F	3600	67.050	67.000			
15F	3600	63.450	63.400			
14F管线层	1500	61.950	61.900			
14F (避难层)	4200	57.750	57.700			
13F	3600	54.150	54.100			
12F	3600	50.550	50.500			
11F	3600	46.950	46.900			
10F	3600	43.350	43.300			
9F	3600	39.750	39.700			
8F	3600	36.150	36.100			
7F	3600	32.550	32.500			
6F	3600	28.950	28.900			
5F	3600	25.350	25.300			
公寓	4F (公寓大堂)	4200	21.150	21.100		
	3F设备夹层	2150	19.000	18.950		
	3F	5500	13.500	13.450		
	2F (酒店大堂)	5500	8.000	7.920		
裙房	1F (公寓、宴会大堂)	8000	0.000	-0.080		
	81F (酒店后勤)	6650	-6.650	-6.750		
	82F (局部人防区)	3500	-10.150	-10.250		
	83F (整体人防区)	3600	-13.750	-14.000		
地下室						

版次		日	修 改 内 容		修 订 者
版次		期	修 订 栏		
图 纸 条 码					
总 设 计 师		赵松林		赵松林	
审 定		黄孝颖		黄孝颖	
审 核		张林汉		张林汉	
设 计		黄孝颖		黄孝颖	
总负责人				宋廷勇	
专业负责人				宋廷勇	
校 核		石昊洋		石昊洋	
设 计		宋廷勇		宋廷勇	
建 设 单 位 佛山市禅城区 保宸置业有限公司					
工 程 名 称 保利天珺秀台7#					
业 务 号		21-347		专 业	建筑
设计阶段		施工图			
图 纸 名 称 四十一~四十三层 平面图					
图 号		J-1-PM21		版 本 号	
出图日期		2023. 08. 02		序 号	
版权所有，不得复制、套用或公开。 ALL RIGHTS RESERVED.					