会签栏								
	建　筑	宋延勇			暖　通	陈少玲		
	结　构	邓艳青						
	给排水	甘兆麟						
	电　气	蔡泽炯						

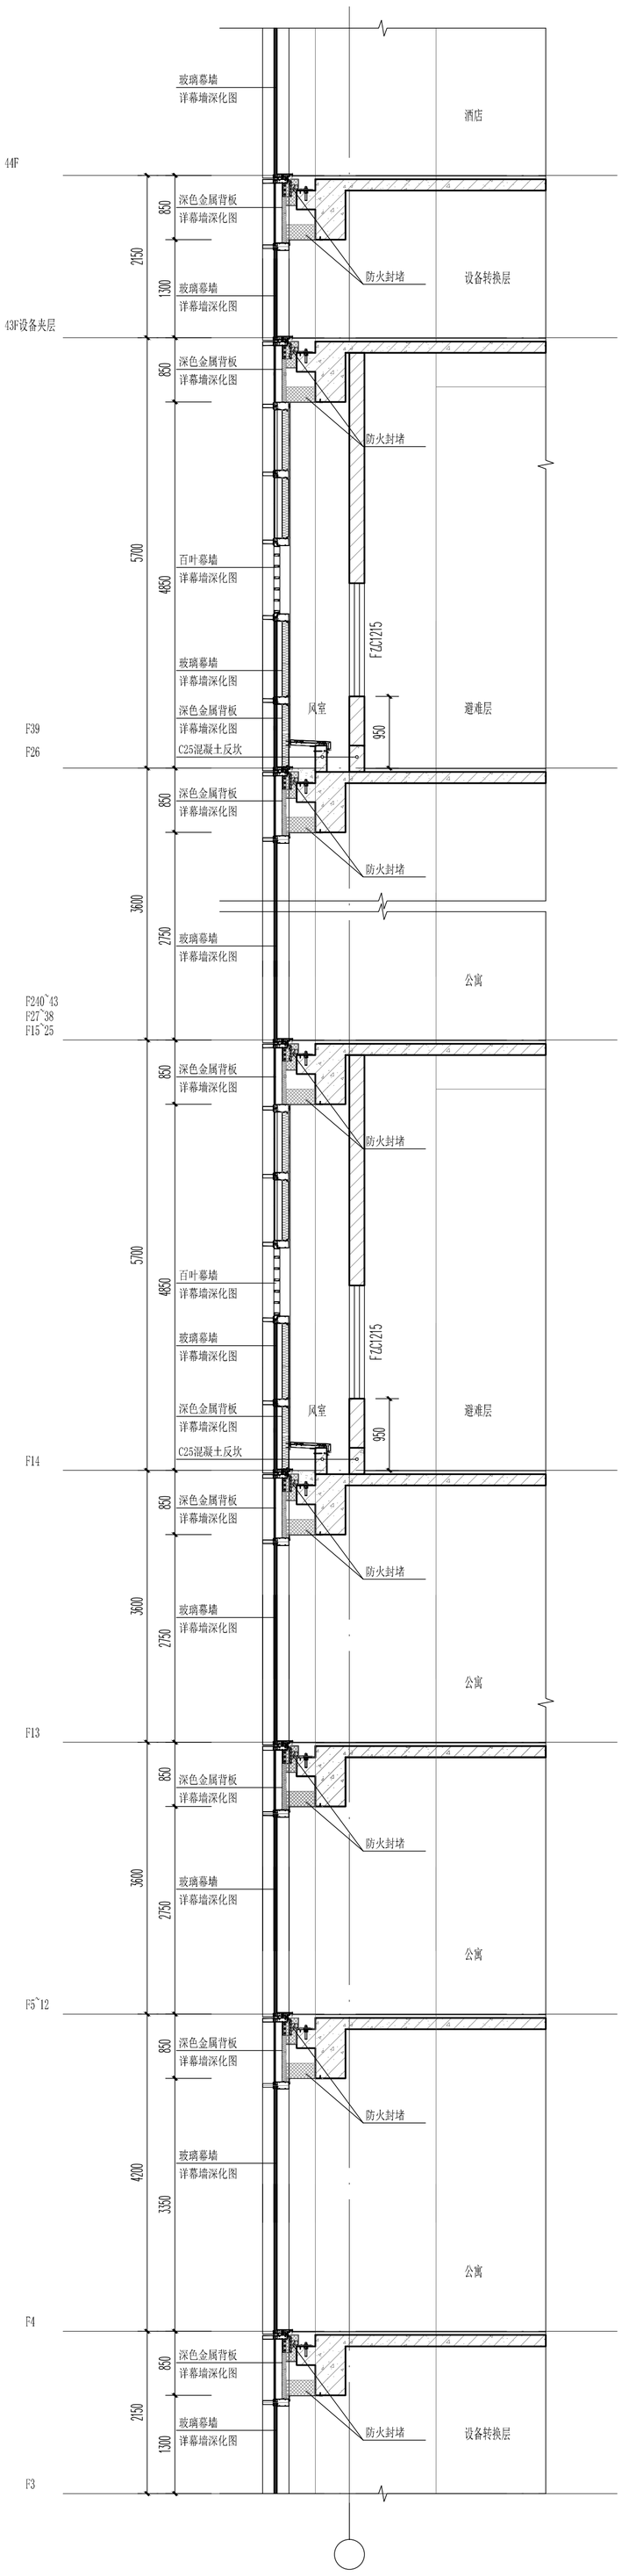

1　比例 1:50　公寓塔楼墙身大样一

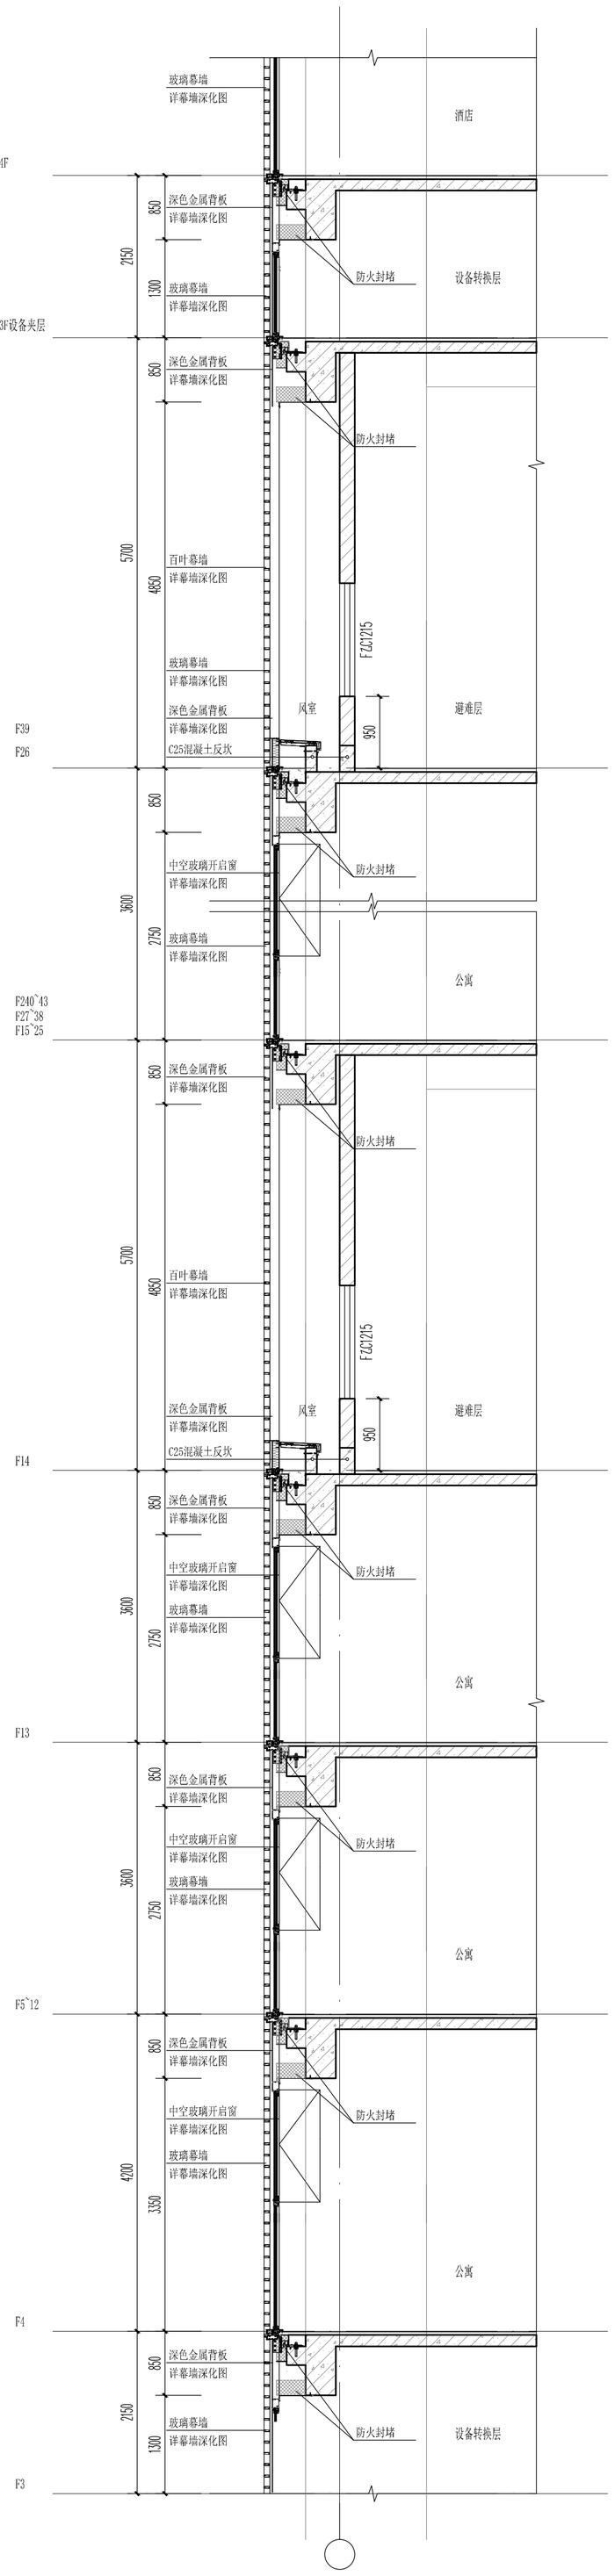

2　比例 1:50　公寓塔楼墙身大样二

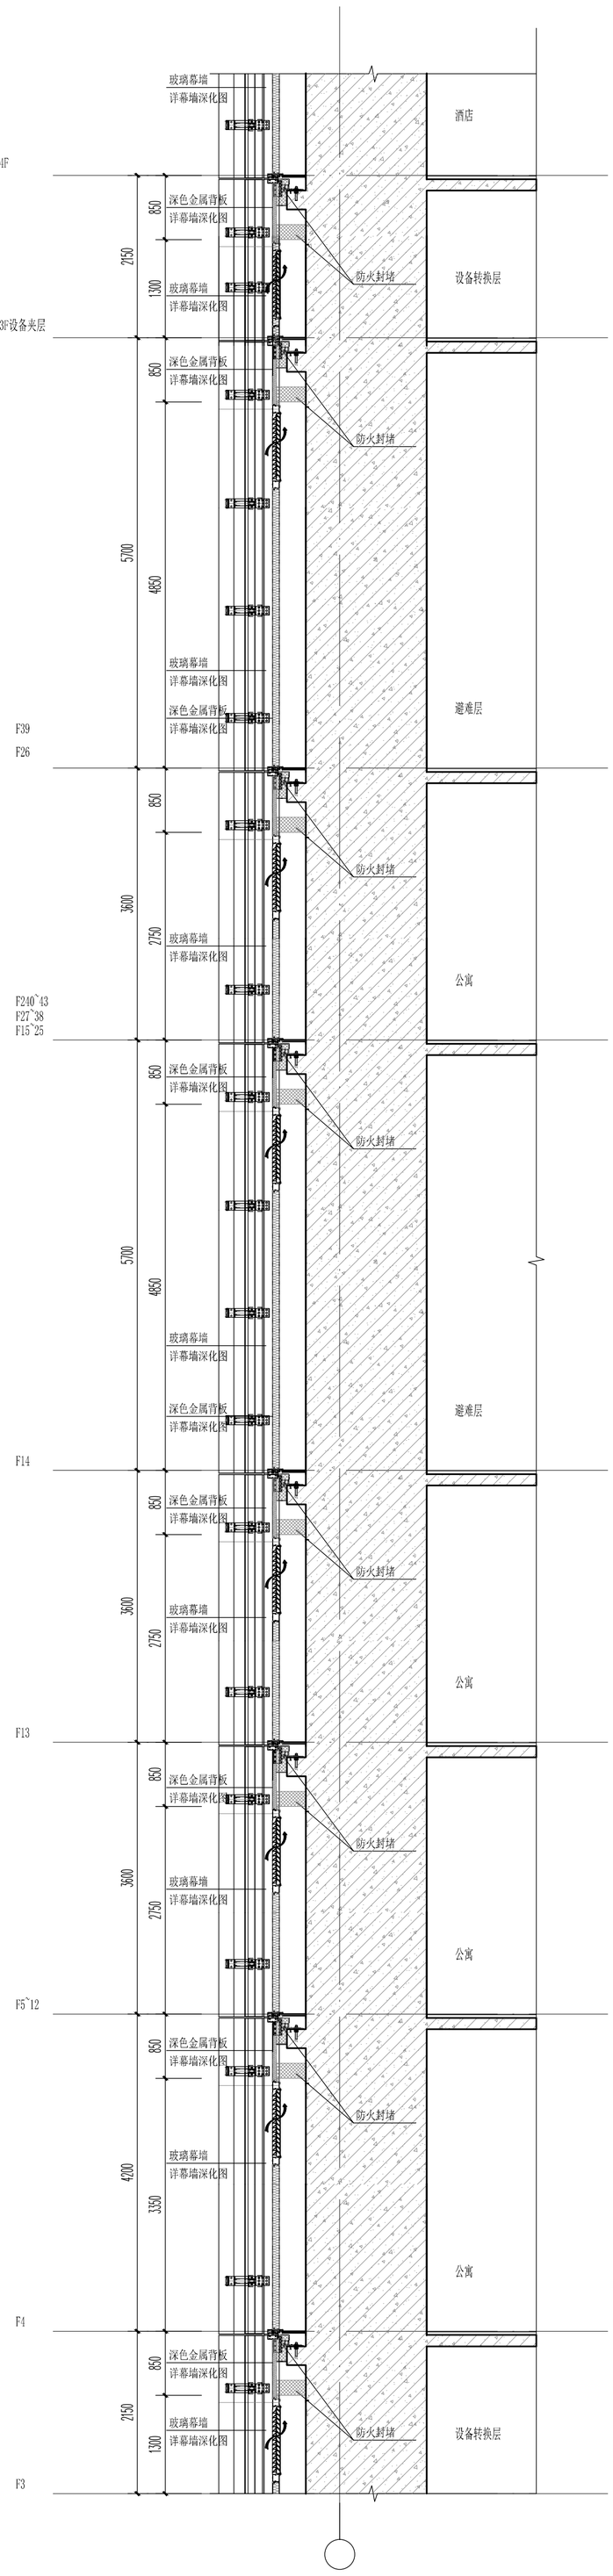

3　比例 1:50　公寓塔楼墙身大样三

院总工程师	赵松林
审　定	黄孝颖
审　核	张林汉
设　计 总负责人	黄孝颖
专业负责人	宋延勇
校　核	石昊洋
设　计	宋延勇

图纸条码

版本号	日期	修改内容修订栏	修订者

平面位置示意 Key Plan

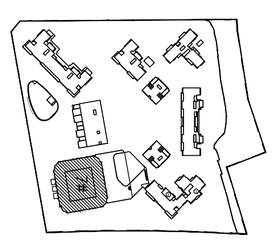

广州市设计院集团有限公司
GUANGZHOU DESIGN INSTITUTE GROUP CO.,LTD.
工程设计甲级资质证书编号：A214007378
工程勘察甲级资质证书编号：B214007378

建设单位	佛山市禅城区保宸置业有限公司
工程名称	保利天珺秀台7#
业务号	21-347
专业	建筑
设计阶段	施工图
图纸名称	塔楼墙身大样图三
图号	J-1-QS03
版本号	
出图日期	2023.08.02
序号	

版权所有，不得复制、套用或公开。
ALL RIGHTS RESERVED.